

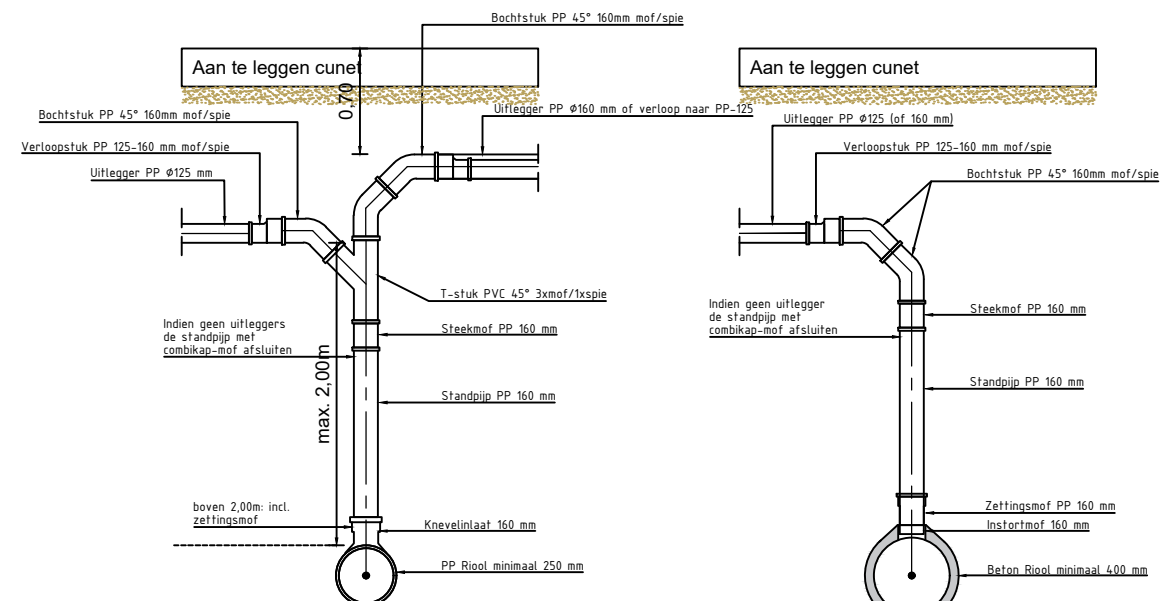


Uitstroombak HWA
Schaal 1:100

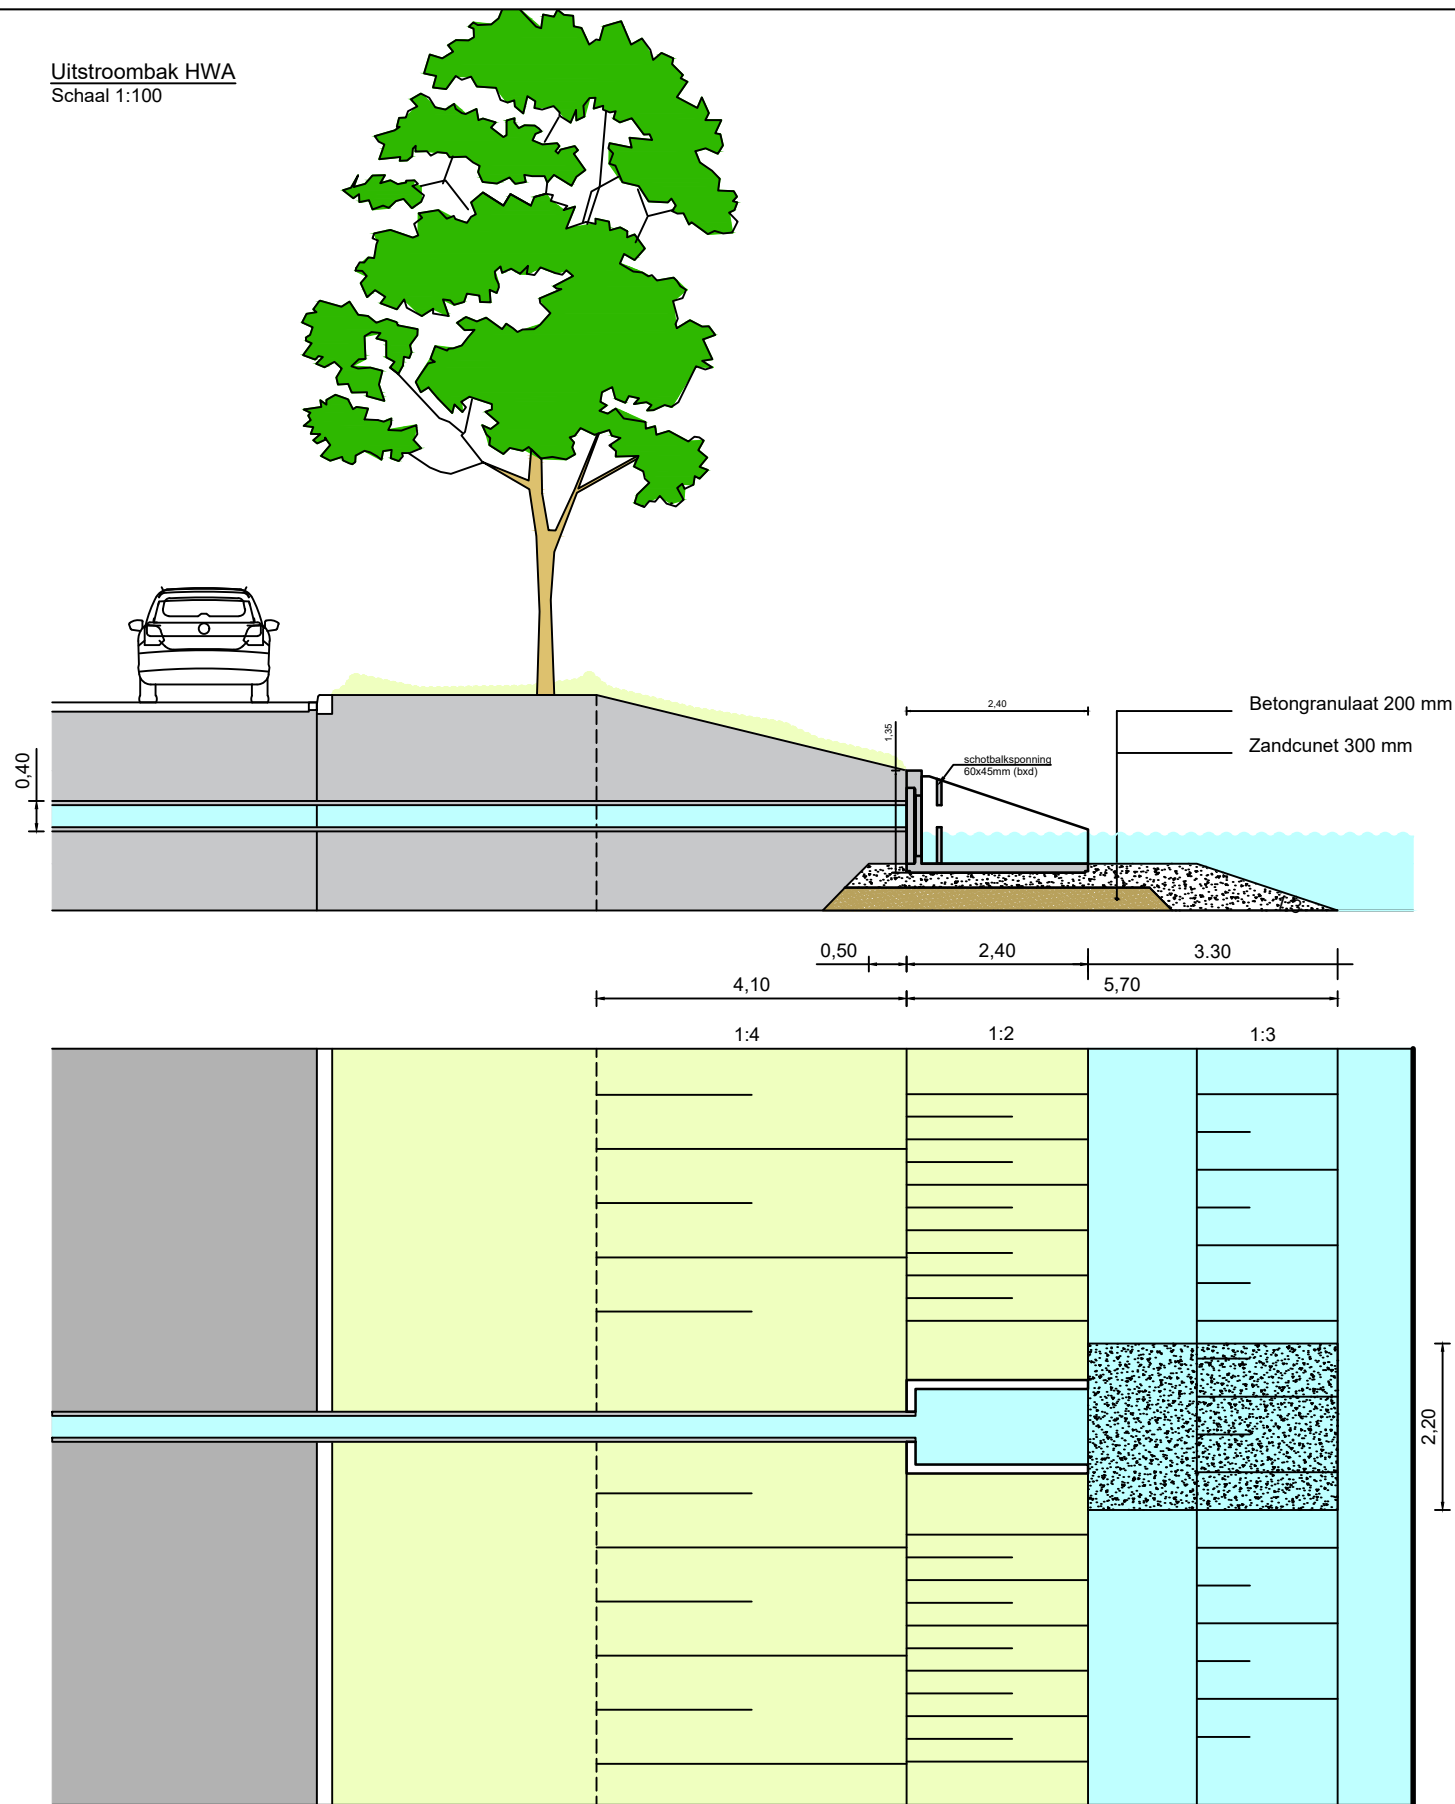


HWA huisaansluiting
Schaal 1:50

DWA huisaansluiting
Schaal 1:50

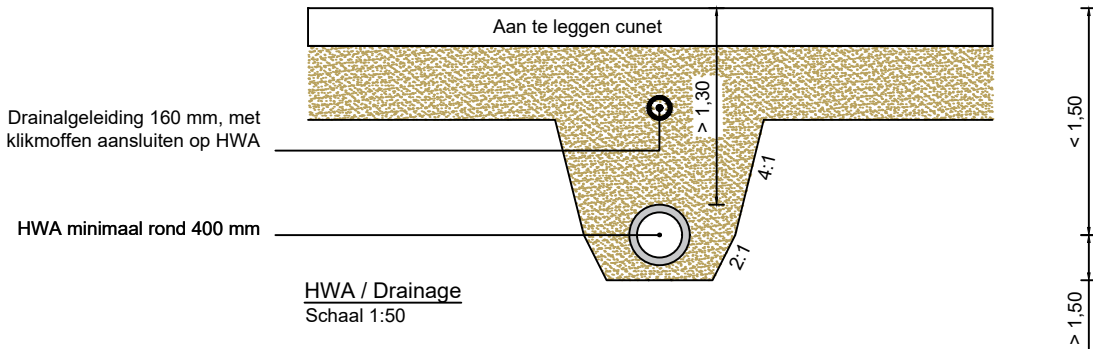


HWA / Drainage
Schaal 1:50

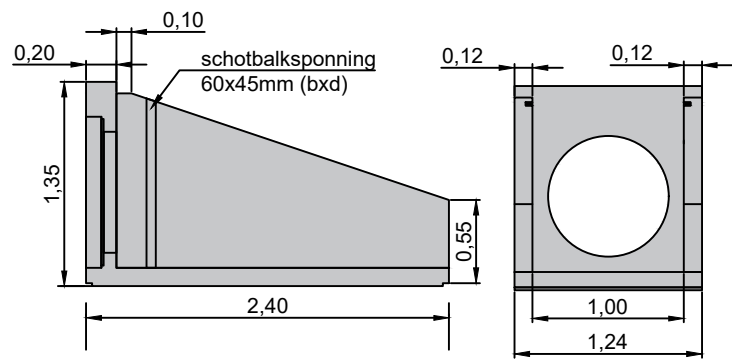


Detail 1: uitstroombak HWA
Schaal 1:50


Drainagekoffer
Schaal 1:50

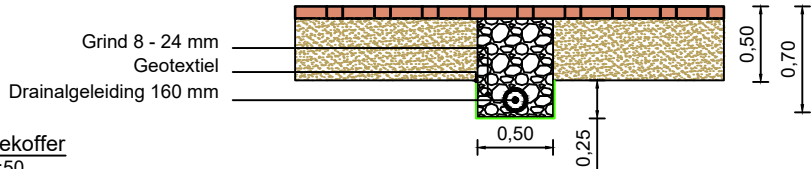


Drainagesleuf openbaar groen
Schaal 1:50

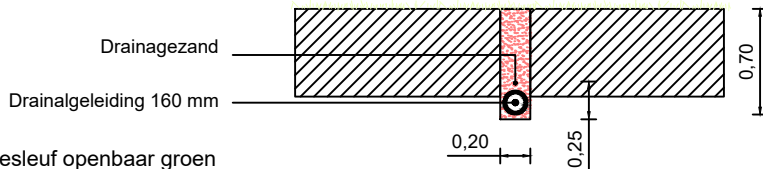


Doorspuitput drainage
Schaal 1:50

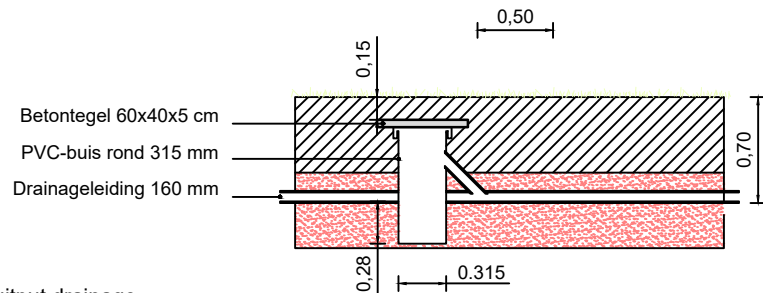


Detail: vuilwaterput
Schaal 1:50

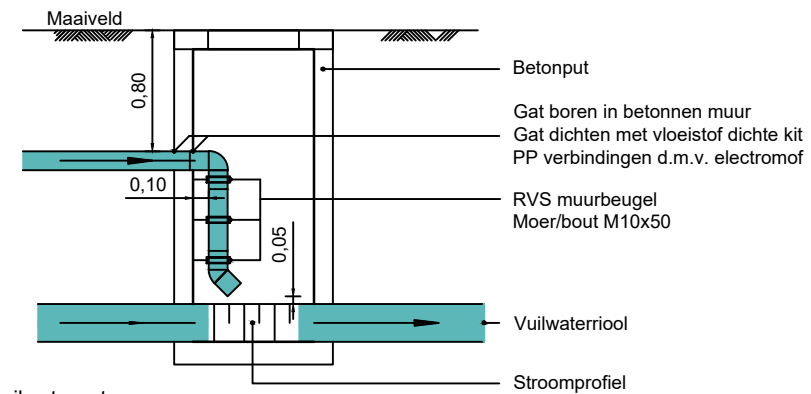


Rioolgemaal
Schaal 1:50

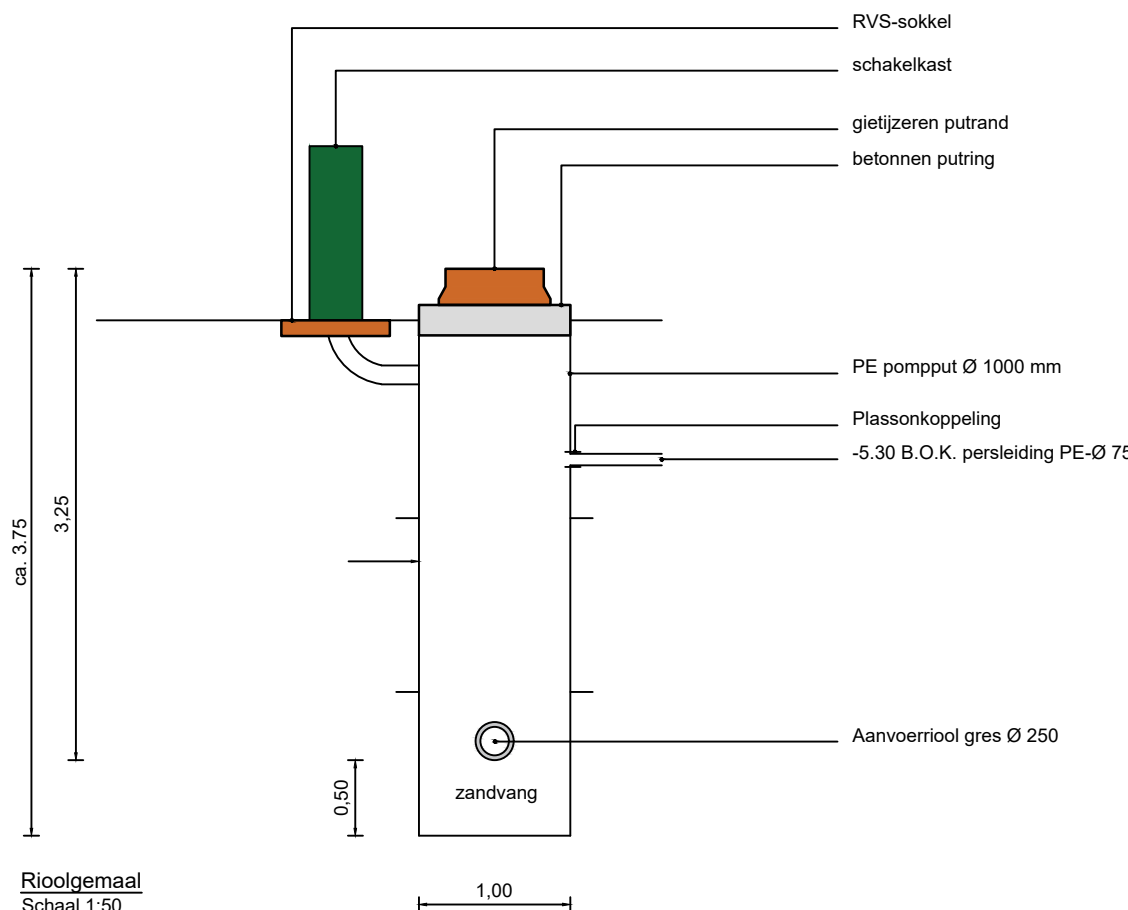



Bushalte trottoirkolke
Schaal 1:20

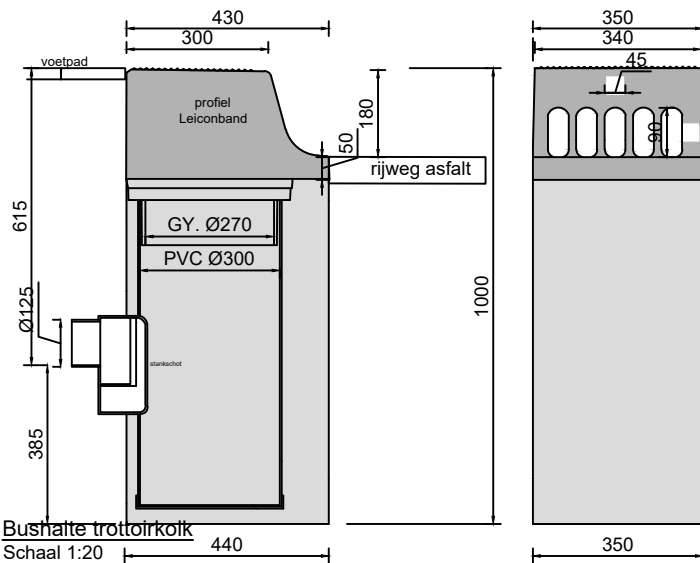

Straatkolk STR-9737 TBS Soest
Schaal 1:20

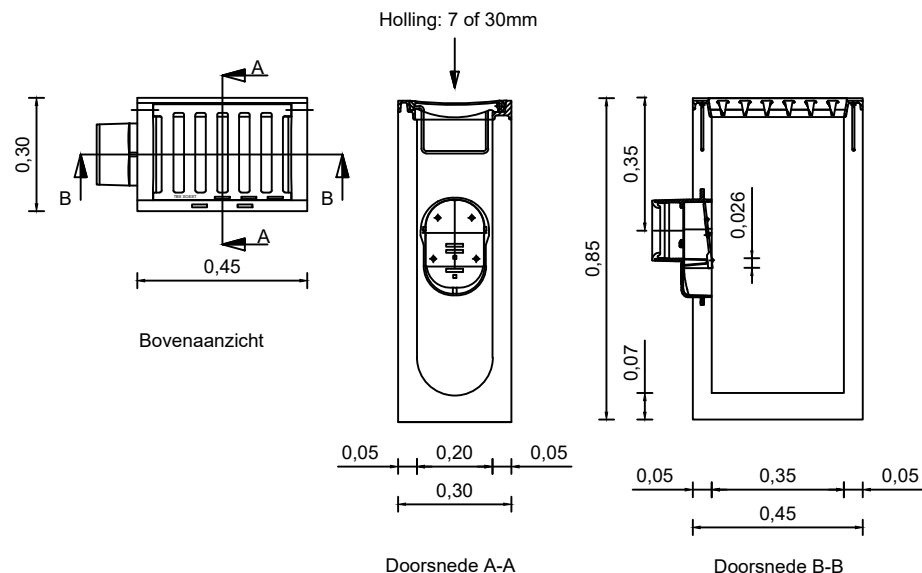

Straatkolk TRK-4717 TBS Soest
Schaal 1:20

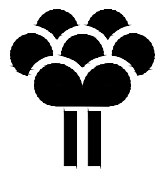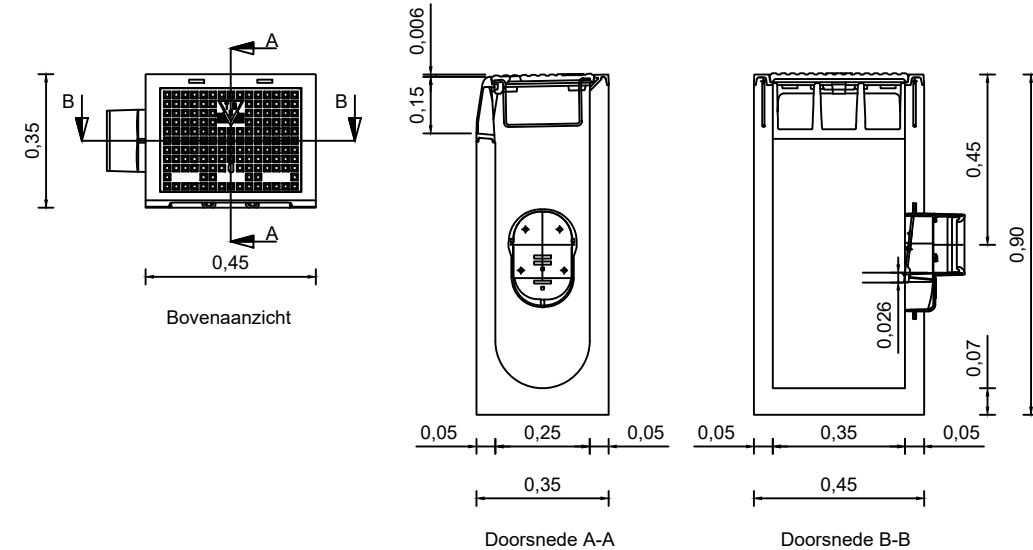




Gemeente
Zoetermeer

Drainage, pompputten, kolken en rioolgemaal

getekend: Gemeente Zoetermeer
gewijzigd: 3-4-2026
datum: formaat: A3
schaal: 1:50/1:20
volgnummer: 1-2

Stadsbeheer 2026

Deze tekening heeft geen juridische werking, zodat daaraan geen rechten ontleend kunnen worden. Wijzigingen voorbehouden.

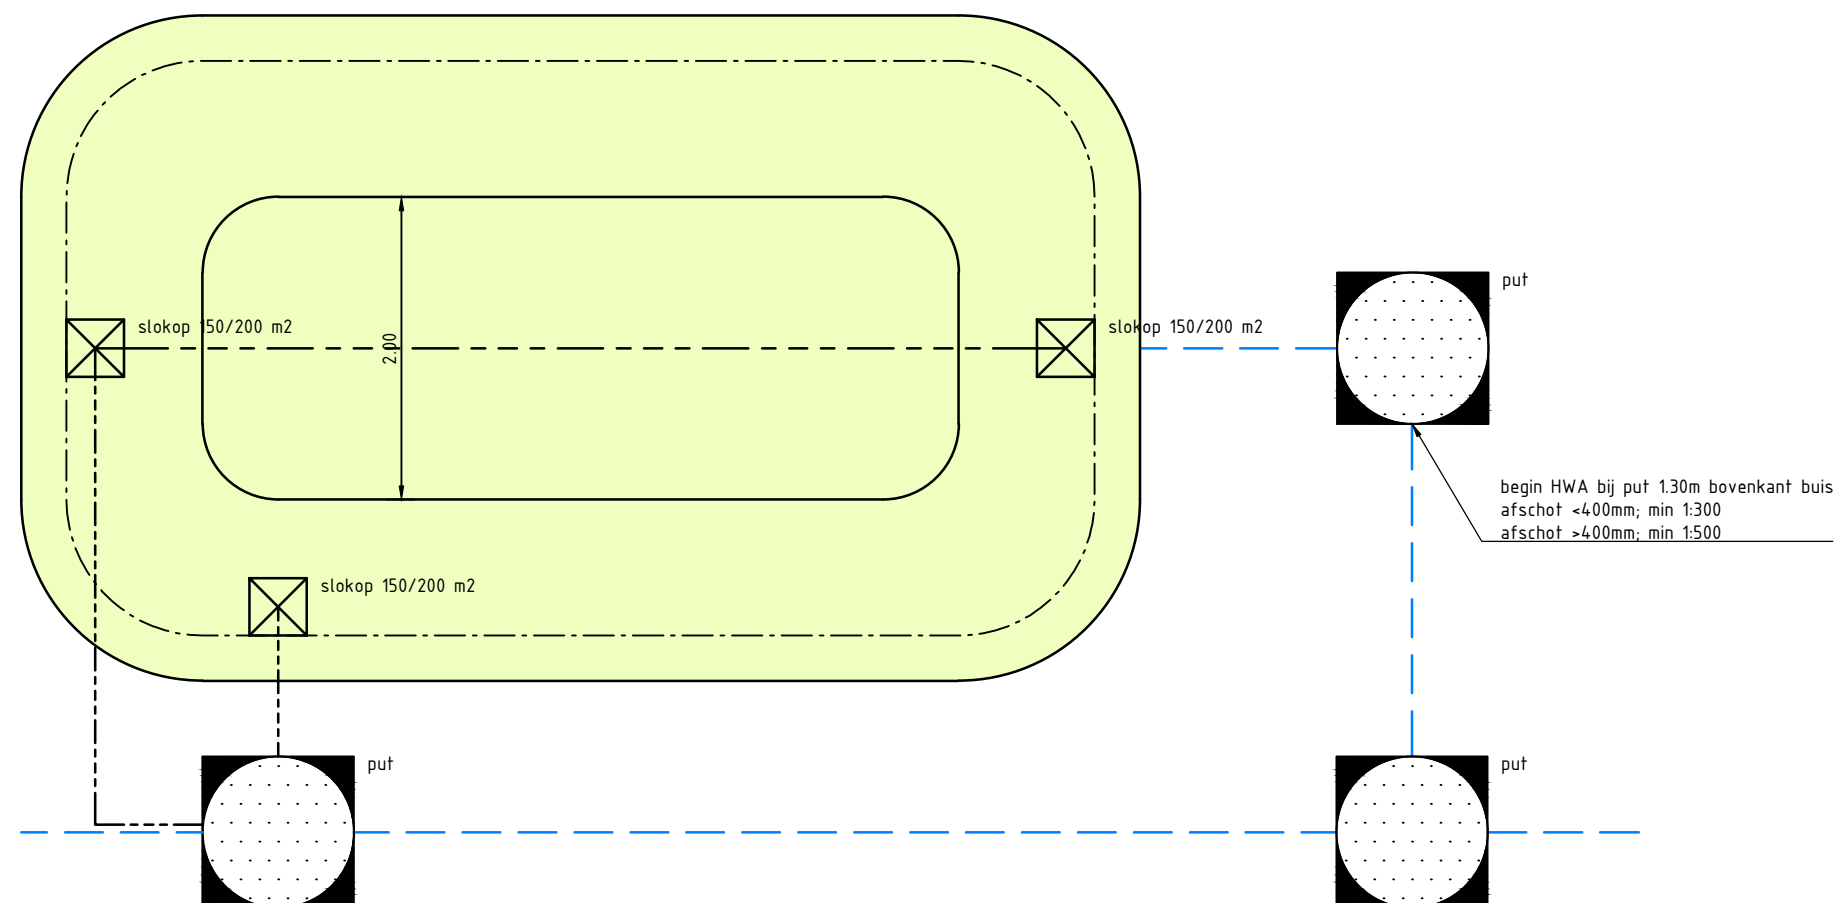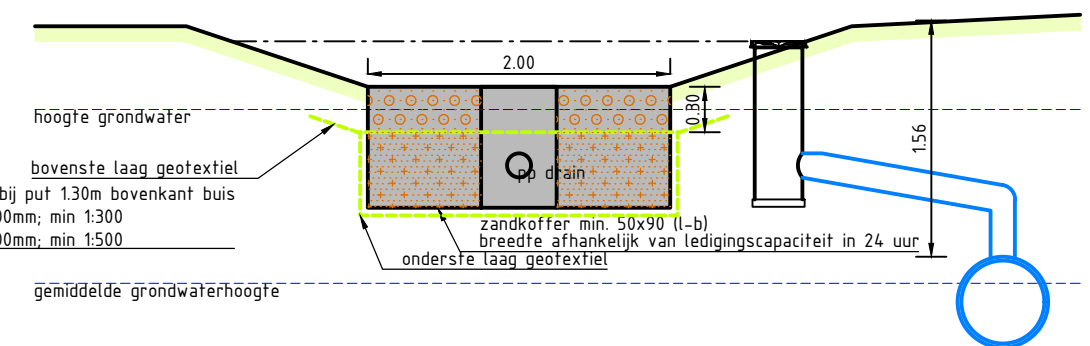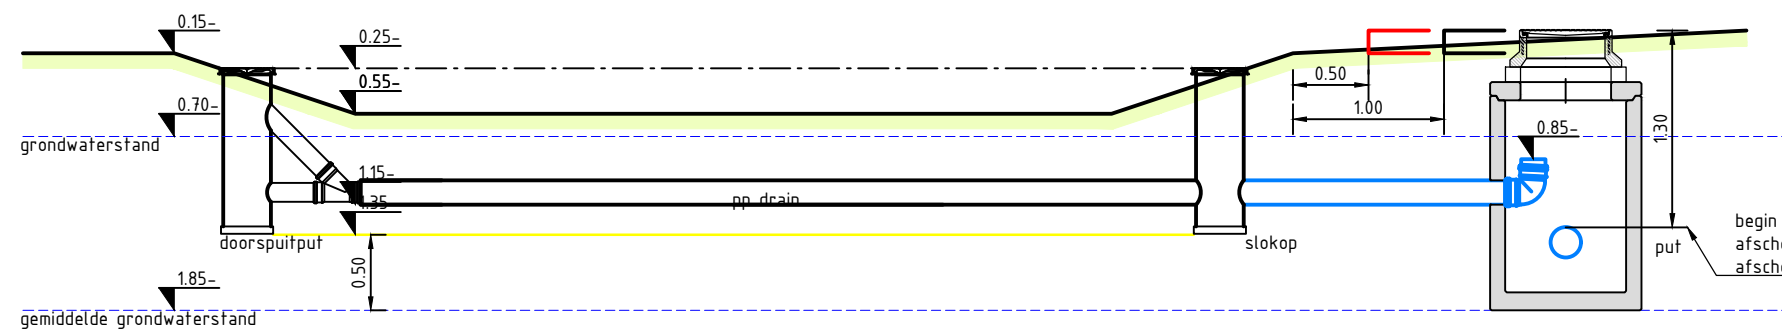


Plattegrond wadi
Schaal 1:50

LEGENDA


- hoogtelijn doorspuitputten/kolk
- pp-drain
- pvc-afvoer
- hwa-leiding
- geotextiel
- grondwaterhoogte Zoetermeer
- gemiddelde grondwaterhoogte GGH
- grondverbetering minimale laagdikte 0,30m
- zandkoffer

bergingscapaciteit en werking
wadi afhankelijk van capaciteit
dynamische berging

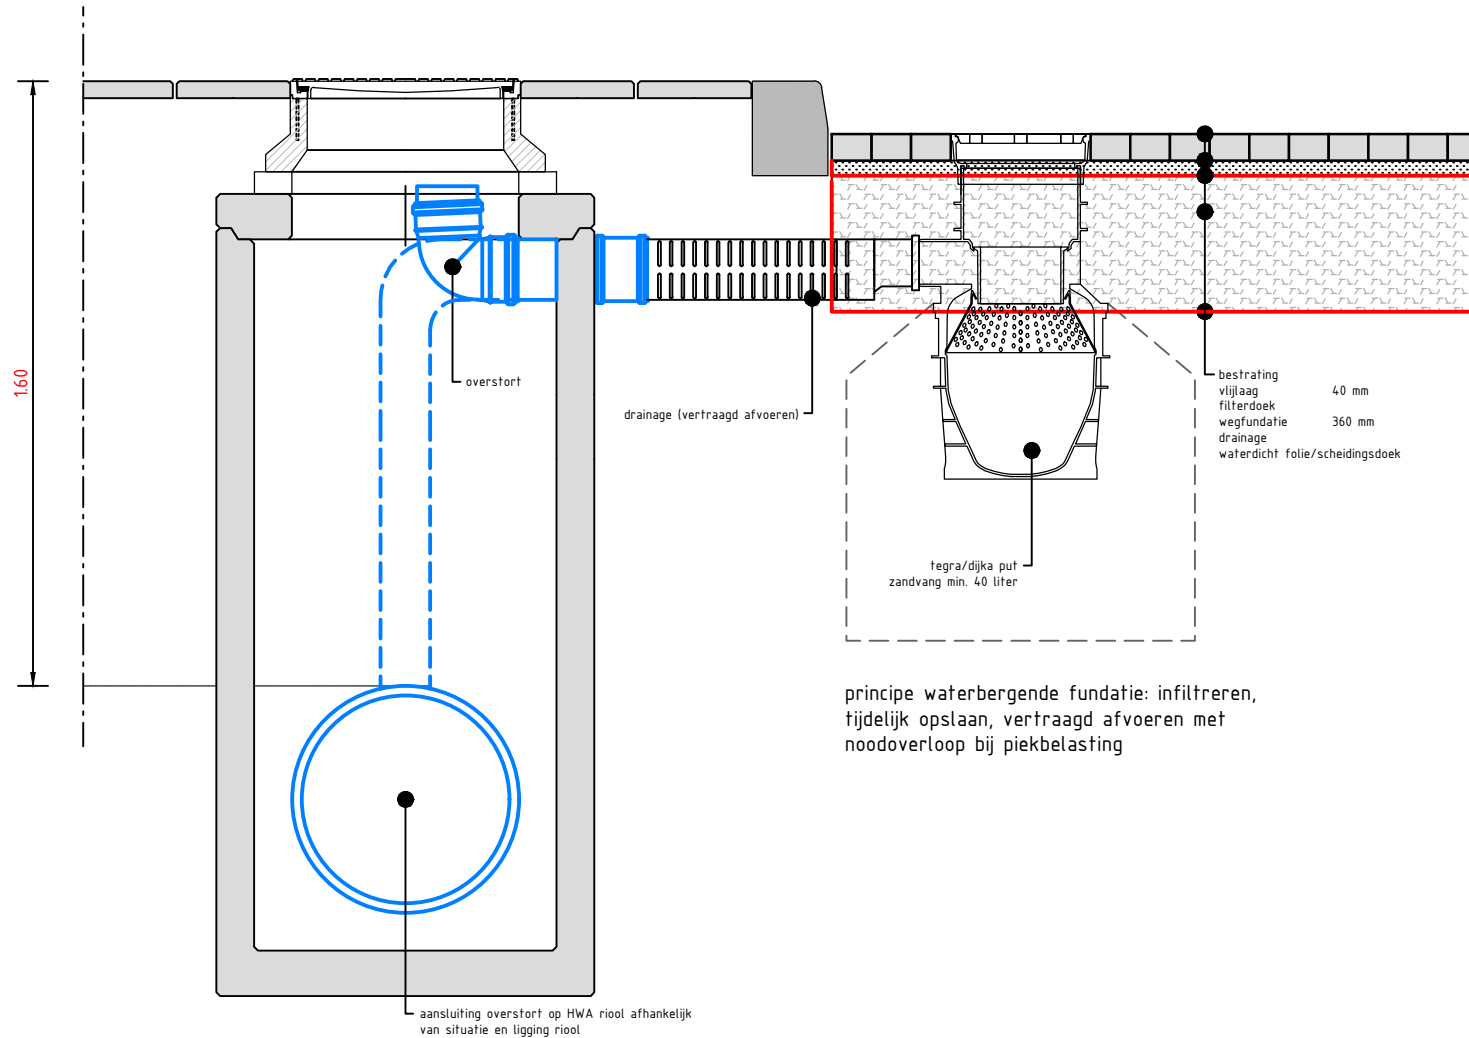


principe waterbergende fundatie: infiltreren,
tijdelijk opslaan, vertraagd afvoeren met
noodoverloop bij piekbelasting

Detail waterbergende bestrating doorsnede
Schaal 1:20

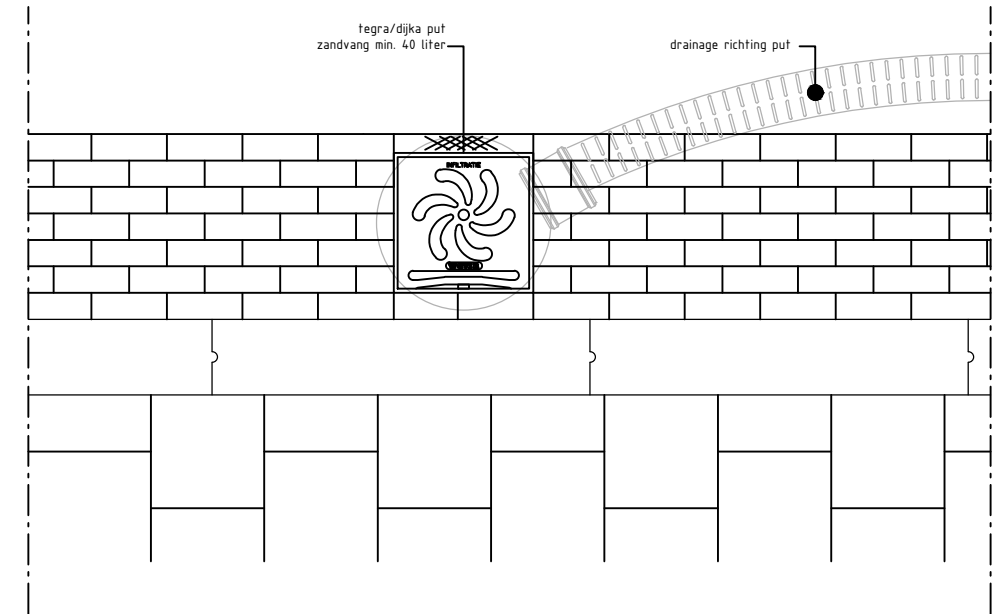


Detail waterbergende bestrating plattegrond
Schaal 1:20

LEGENDA	
	HWA riool
	kabels en leidingen
	waterbergend pakket
	doorvoer kabels en leidingen
	kolk

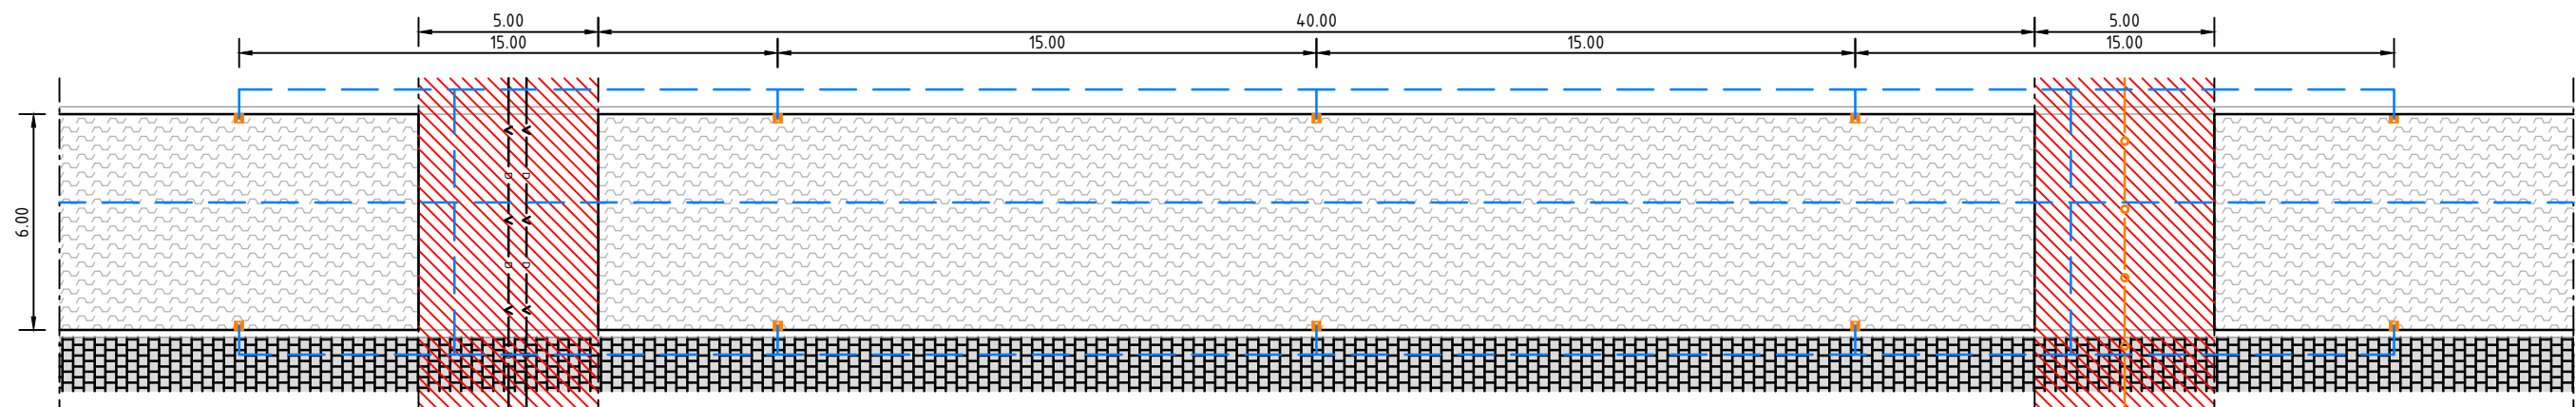

Detail waterbergende bestrating plattegrond
Schaal 1:200

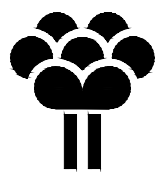


Gemeente
Zoetermeer

Details waterbergende bestrating

getekend: Gemeente Zoetermeer
gewijzigd: 3-4-2026
datum:

formaat: A3
schaal: 1:200
volgnummer: 1-4

Stadsbeheer 2026

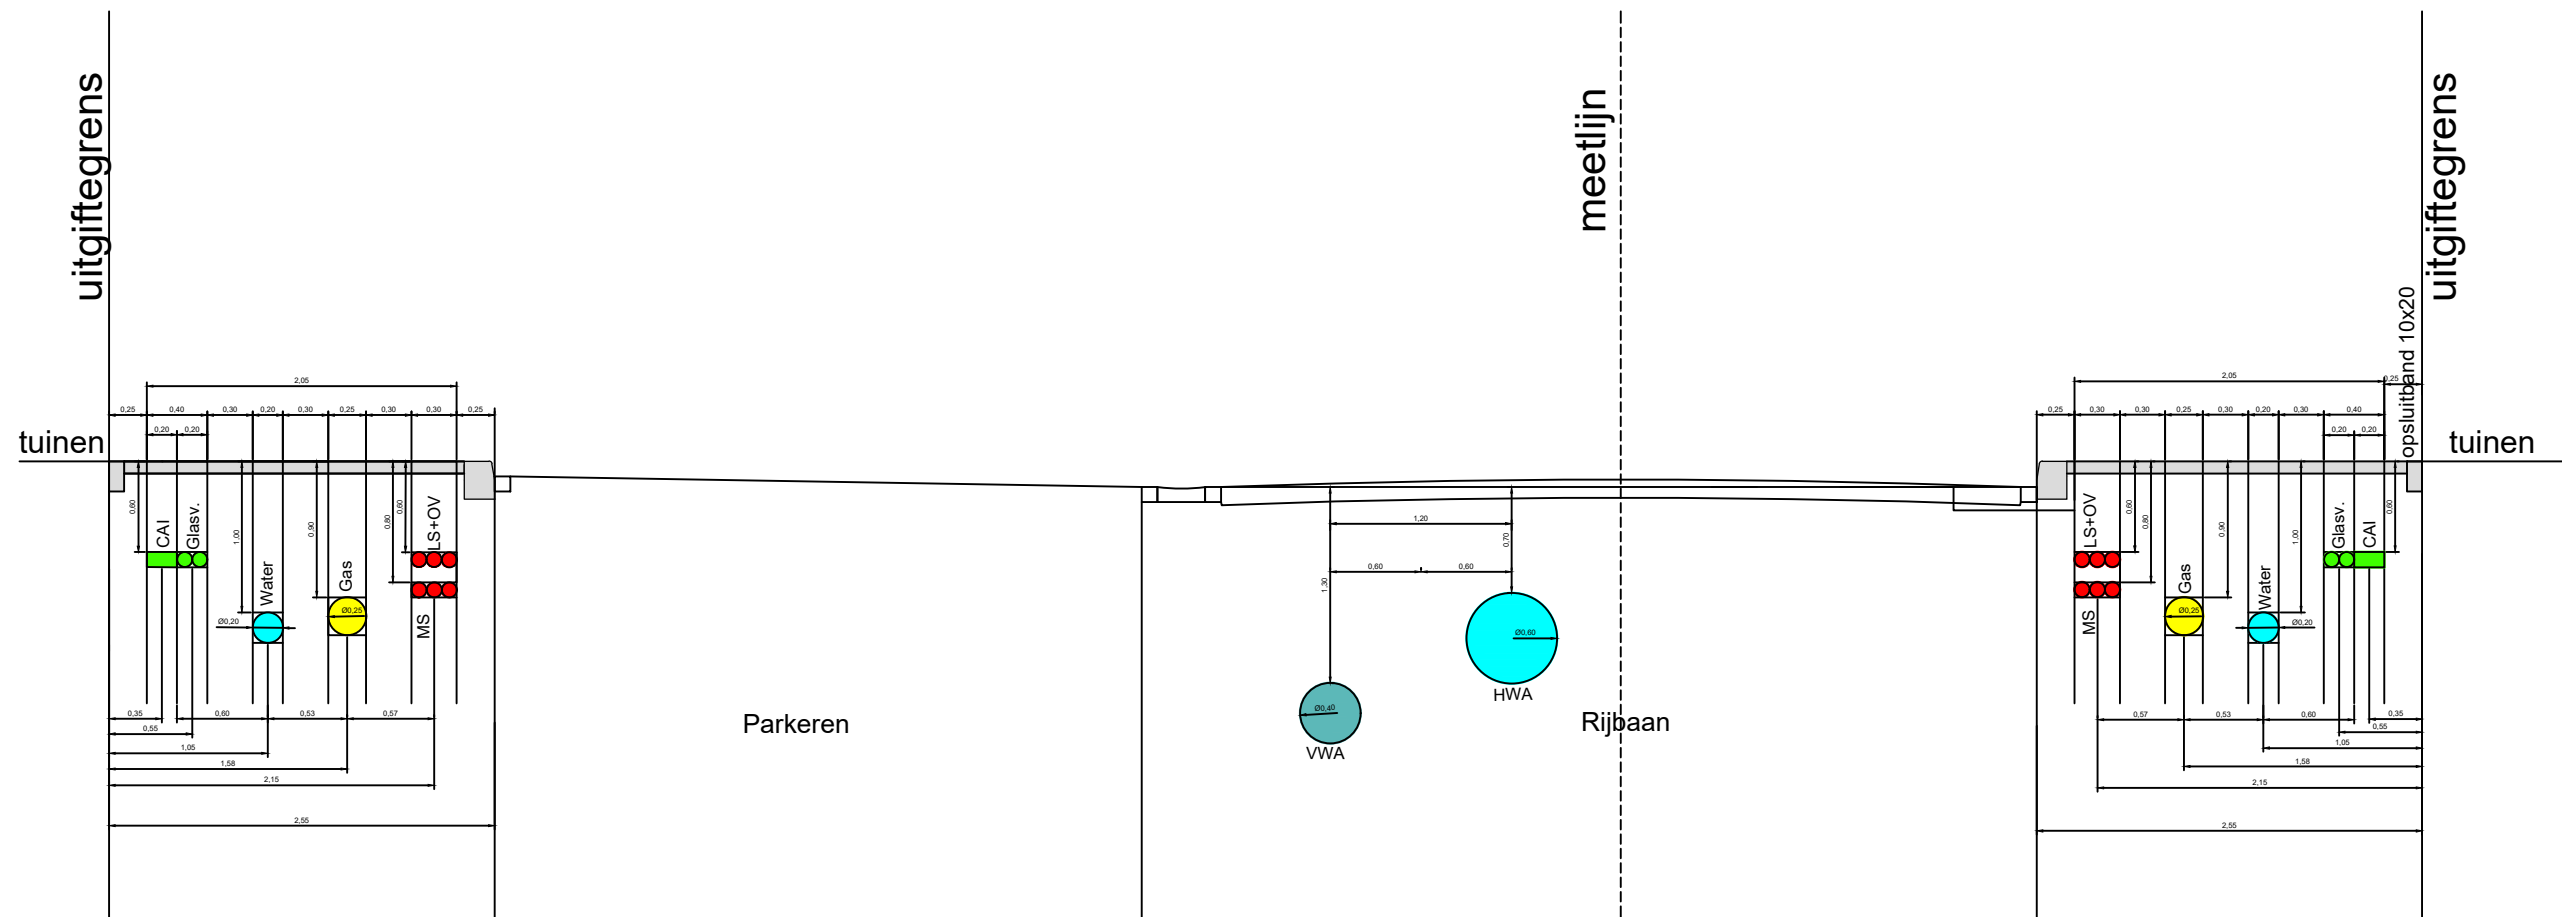

Minimale
gronddekking:

Data 60 cm

Water 100 cm


Gas 90 - 110 cm

Elektra LS 60 cm

Elektra MS 80 cm

Principe profiel Nutsbedrijven

Vanuit de uitgiftegrens data, KPN - ZIGGO e.d. daarna Water, Gas, Electra al dan niet gecombineerd met OV, gevolgd door de Riolering. Electra nooit naast data omdat de een de ander kan beïnvloeden met zwerfstroom e.d.

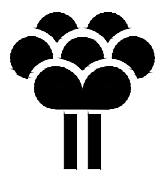


Gemeente
Zoetermeer

2 Kabels en leidingen - traditioneel

getekend: Gemeente Zoetermeer
gewijzigd: 3-4-2026
datum:

formaat: A3
schaal: 1:50
volgnummer: 2-1

Stadsbeheer 2026

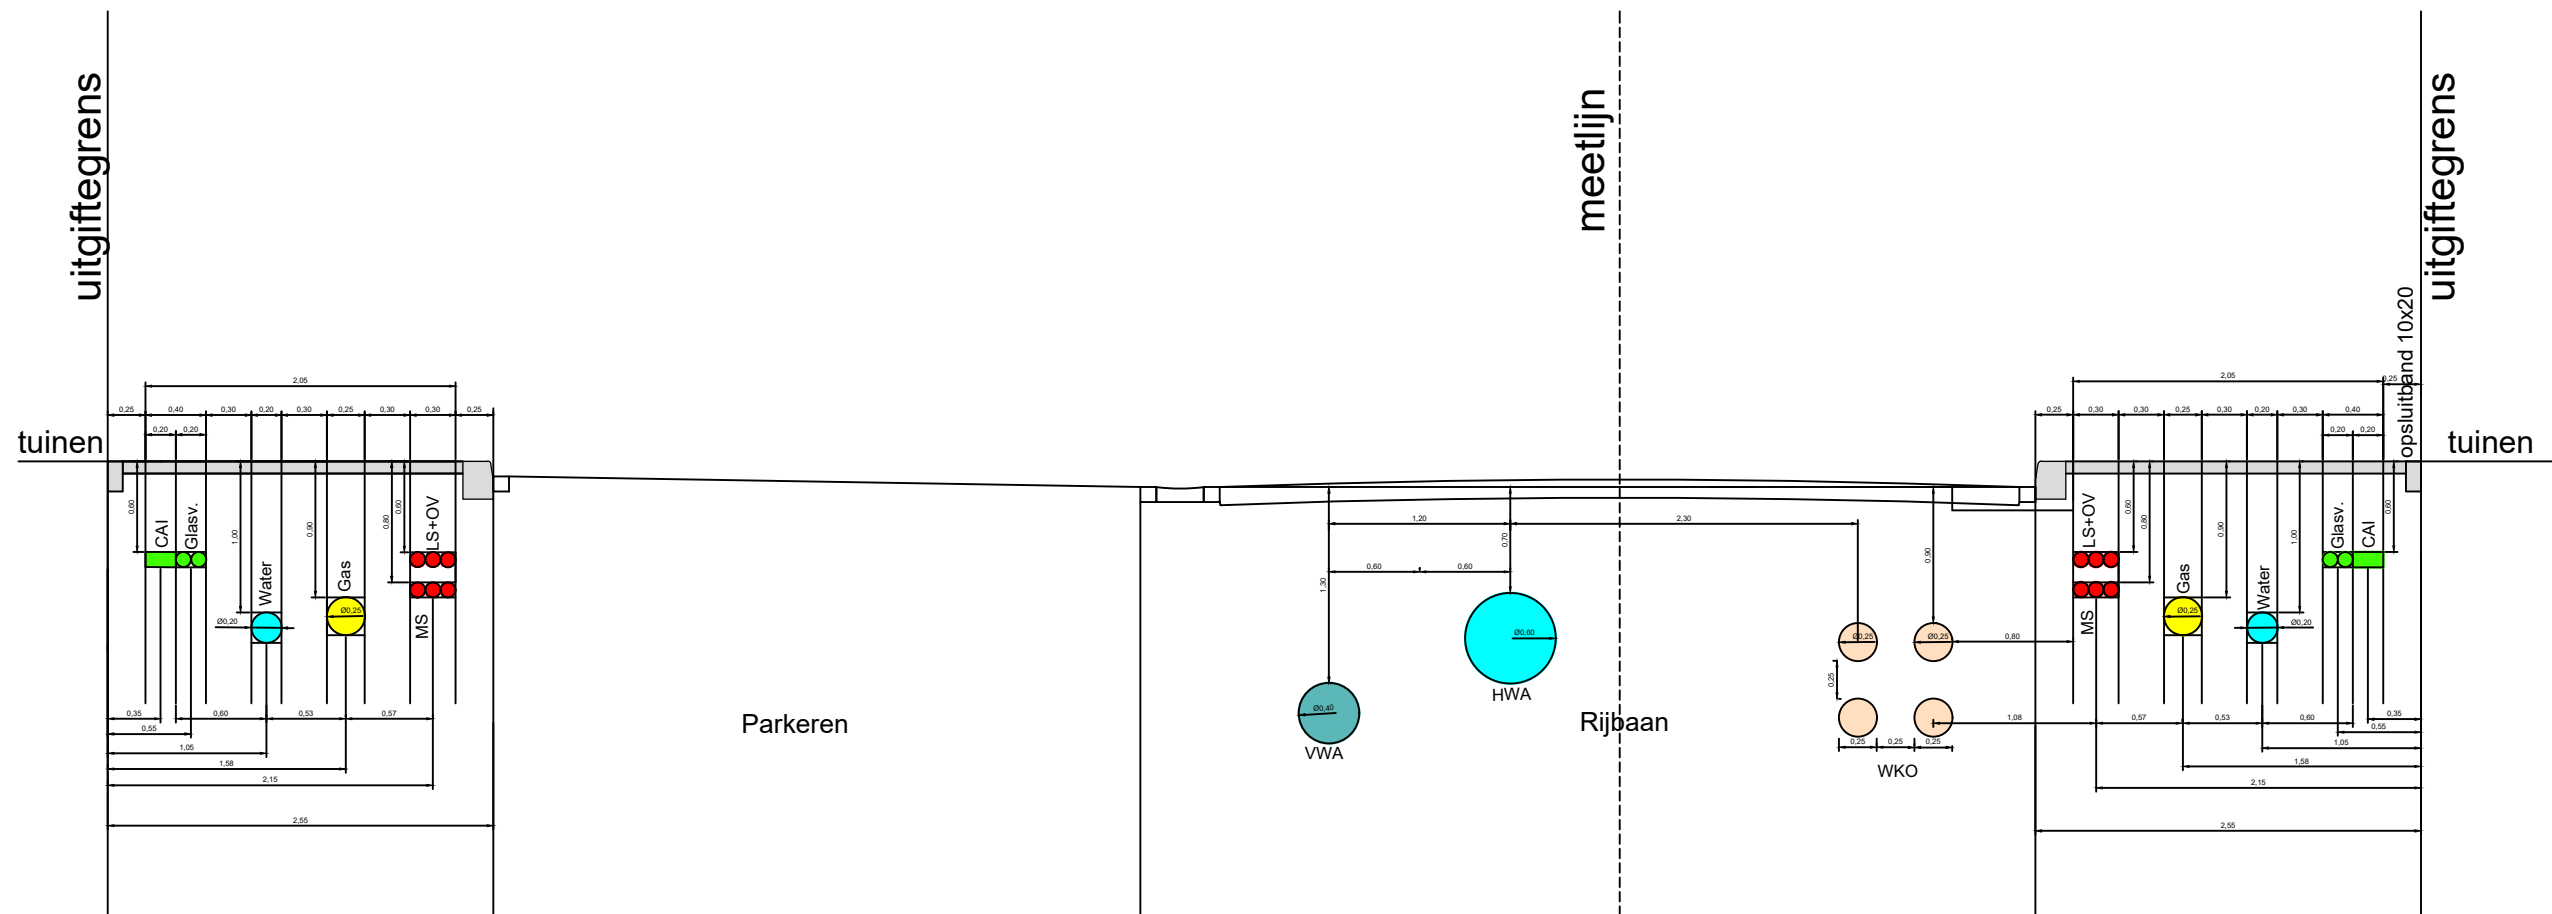

Minimale
gronddekking:

Data 60 cm

Water 100 cm

Gas 90 - 110 cm


Warmte 90 cm

Elektra LS 60 cm

Elektra MS 80 cm

Principe profiel nutsbedrijven

Vanuit de uitgiftegrens data, KPN - ZIGGO e.d. daarna Water, Electra al dan niet gecombineerd met OV, gevolgd door de WKO leidingen en daarna de Riolering.

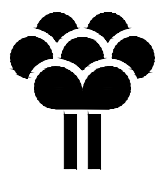


Gemeente
Zoetermeer

2 Kabels en leidingen - traditioneel + warmte

getekend: Gemeente Zoetermeer
gewijzigd:
datum: 3-4-2026

formaat: A3
schaal: 1:50
volgnummer: 2-2

Stadsbeheer 2026

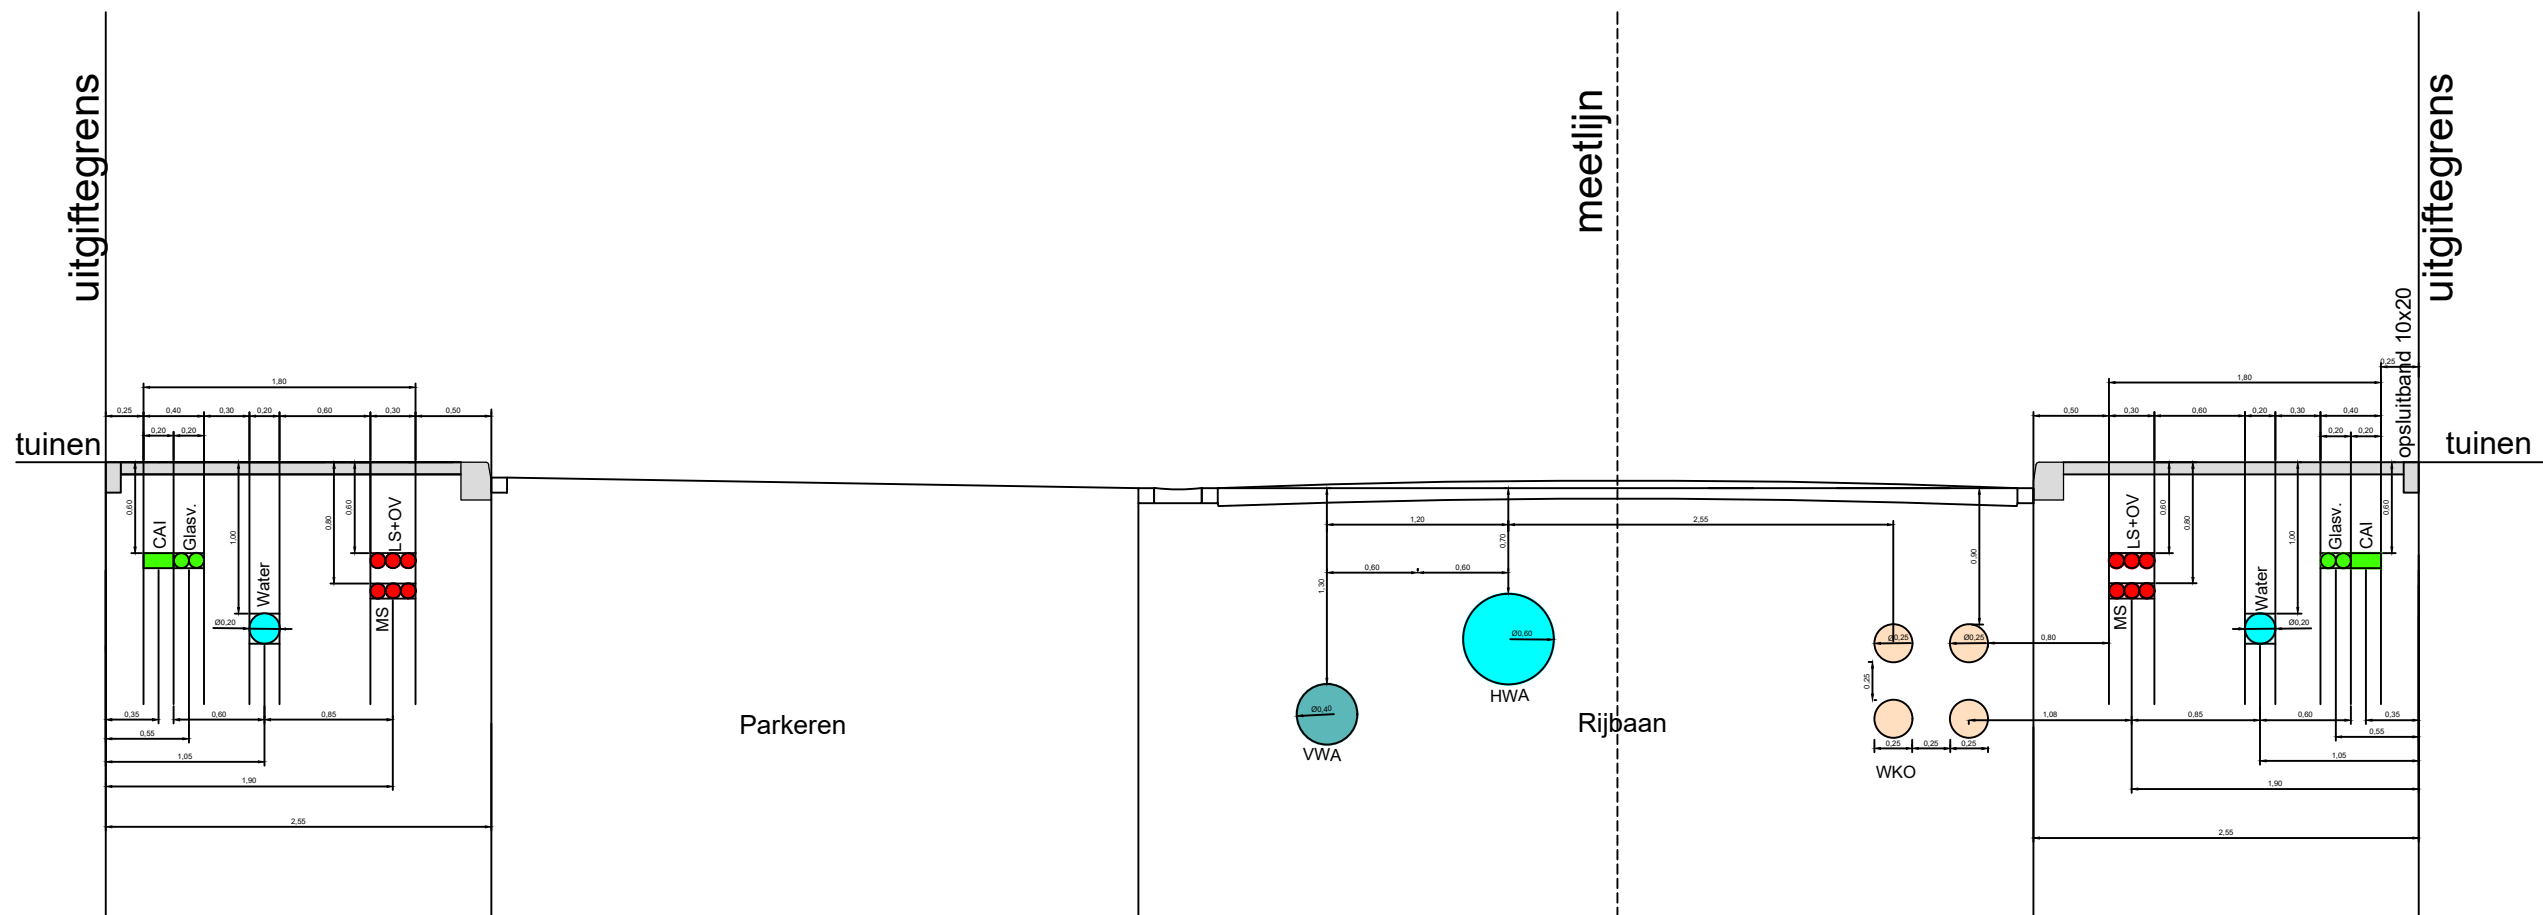

Minimale
gronddekking:

Data 60 cm

Water 100 cm


Warmte 90 cm

Elektra LS 60 cm

Elektra MS 80 cm

Principe profiel nutsbedrijven

Vanuit de uitgiftegrens data, KPN - ZIGGO e.d. daarna Water, Electra al dan niet gecombineerd met OV, gevolgd door de WKO leidingen en daarna de Riolering.

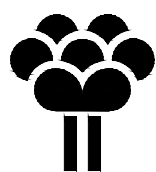

Gemeente
Zoetermeer


2 Kabels en leidingen - gasloos

getekend: Gemeente Zoetermeer
gewijzigd:
datum: 3-4-2026

formaat: A3
schaal: 1:50
volgnummer: 2-3

Stadsbeheer 2026

Bomen zonder beschermende maatregelen

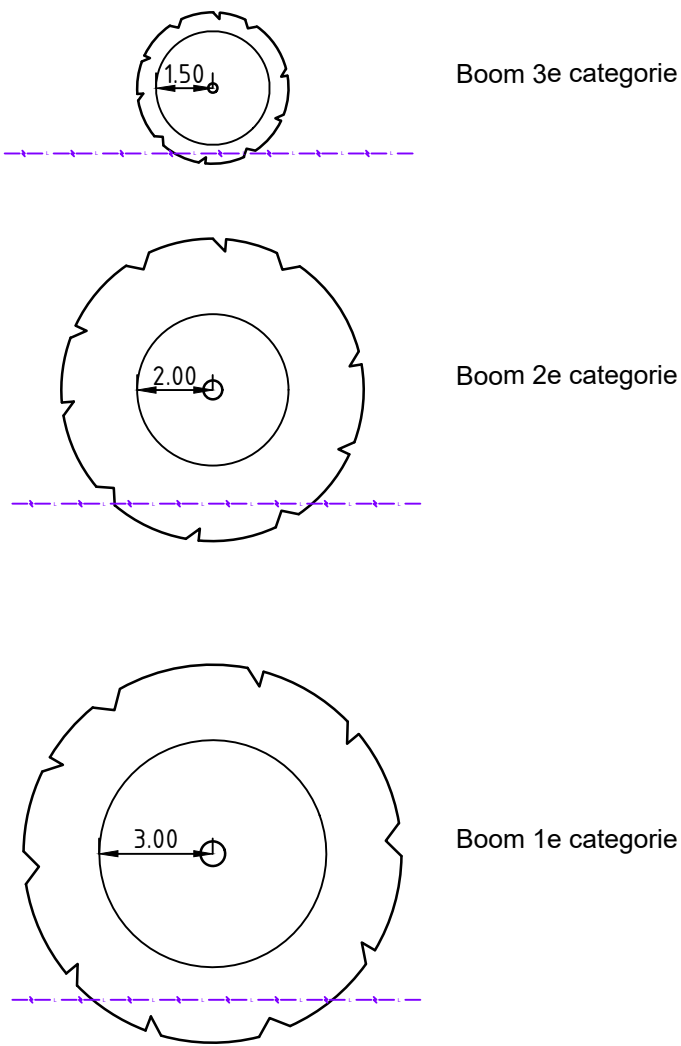


Kabel buiten de straal. Er hoeven geen beschermende maatregelen genomen te worden ter bescherming van de kabel

Zonder wortel beschermende maatregelen

Boomcategorie	Te verwachten tophoogte	Minimumafstand Hart stam tot zijkant K&L trace
1	>12 meter	3.0 meter
2	Tussen 6 en 12 m	2.0 meter
3	<6 meter	1.5 meter

Bomen met beschermende maatregelen

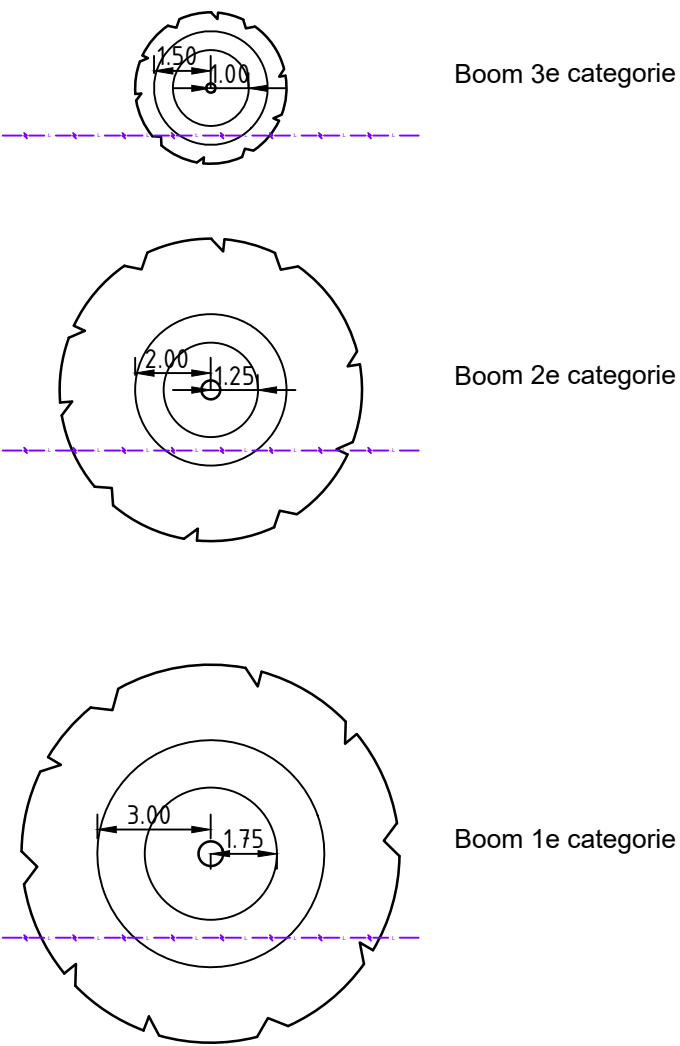


Kabel binnen de straal. Er moeten beschermende maatregelen genomen worden ter bescherming van de kabel

Met wortel beschermende maatregelen


Boomcategorie	Te verwachten tophoogte	Minimumafstand Hart stam tot zijkant K&L trace
1	>12 meter	1.75 meter
2	Tussen 6 en 12 m	1.25 meter
3	<6 meter	1.00 meter


Nieuwe kabels en leidingen bij bestaande bomen

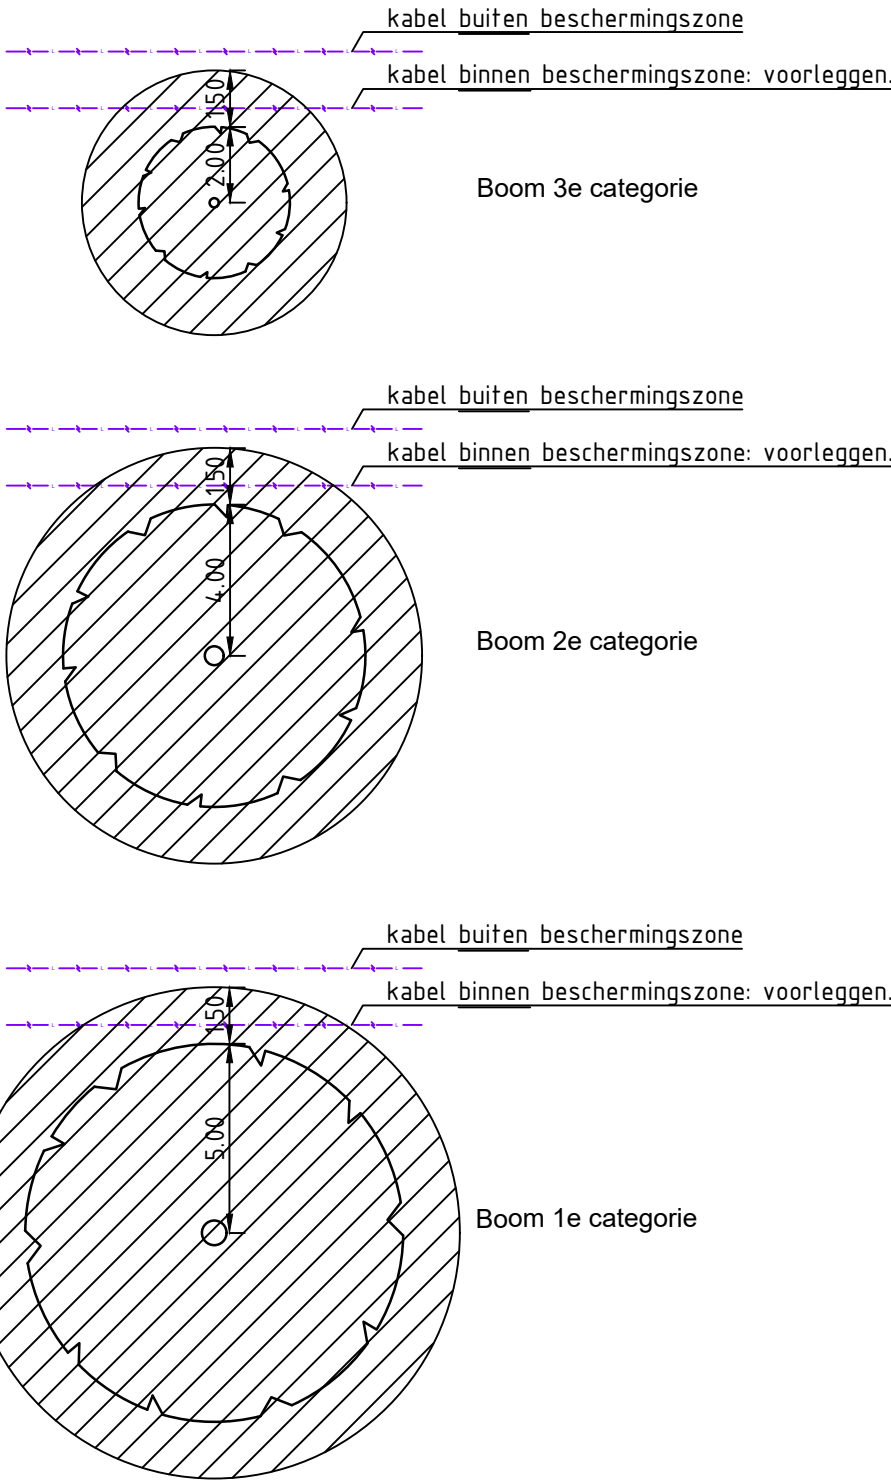

Kwetsbare boomzone: boomkroon (volgroeid) + 1,50 m.
Wanneer er ondergrondse infra wordt aangelegd binnen de 'kwetsbare boomzone' dient dit altijd ter goedkeuring te worden voorgelegd aan de assetspecialist bomen en groen, en de vergunningverlener K&L.

Afwijking Handboek Bomen: Voor de minimale afstanden en beschermingszones tussen bomen en het tracé voor kabels & leidingen, zijn de in deze detailtekening genoemde Zoetermeerse categorieën en maatvoeringen (1.00m tot 3.00m) leidend.

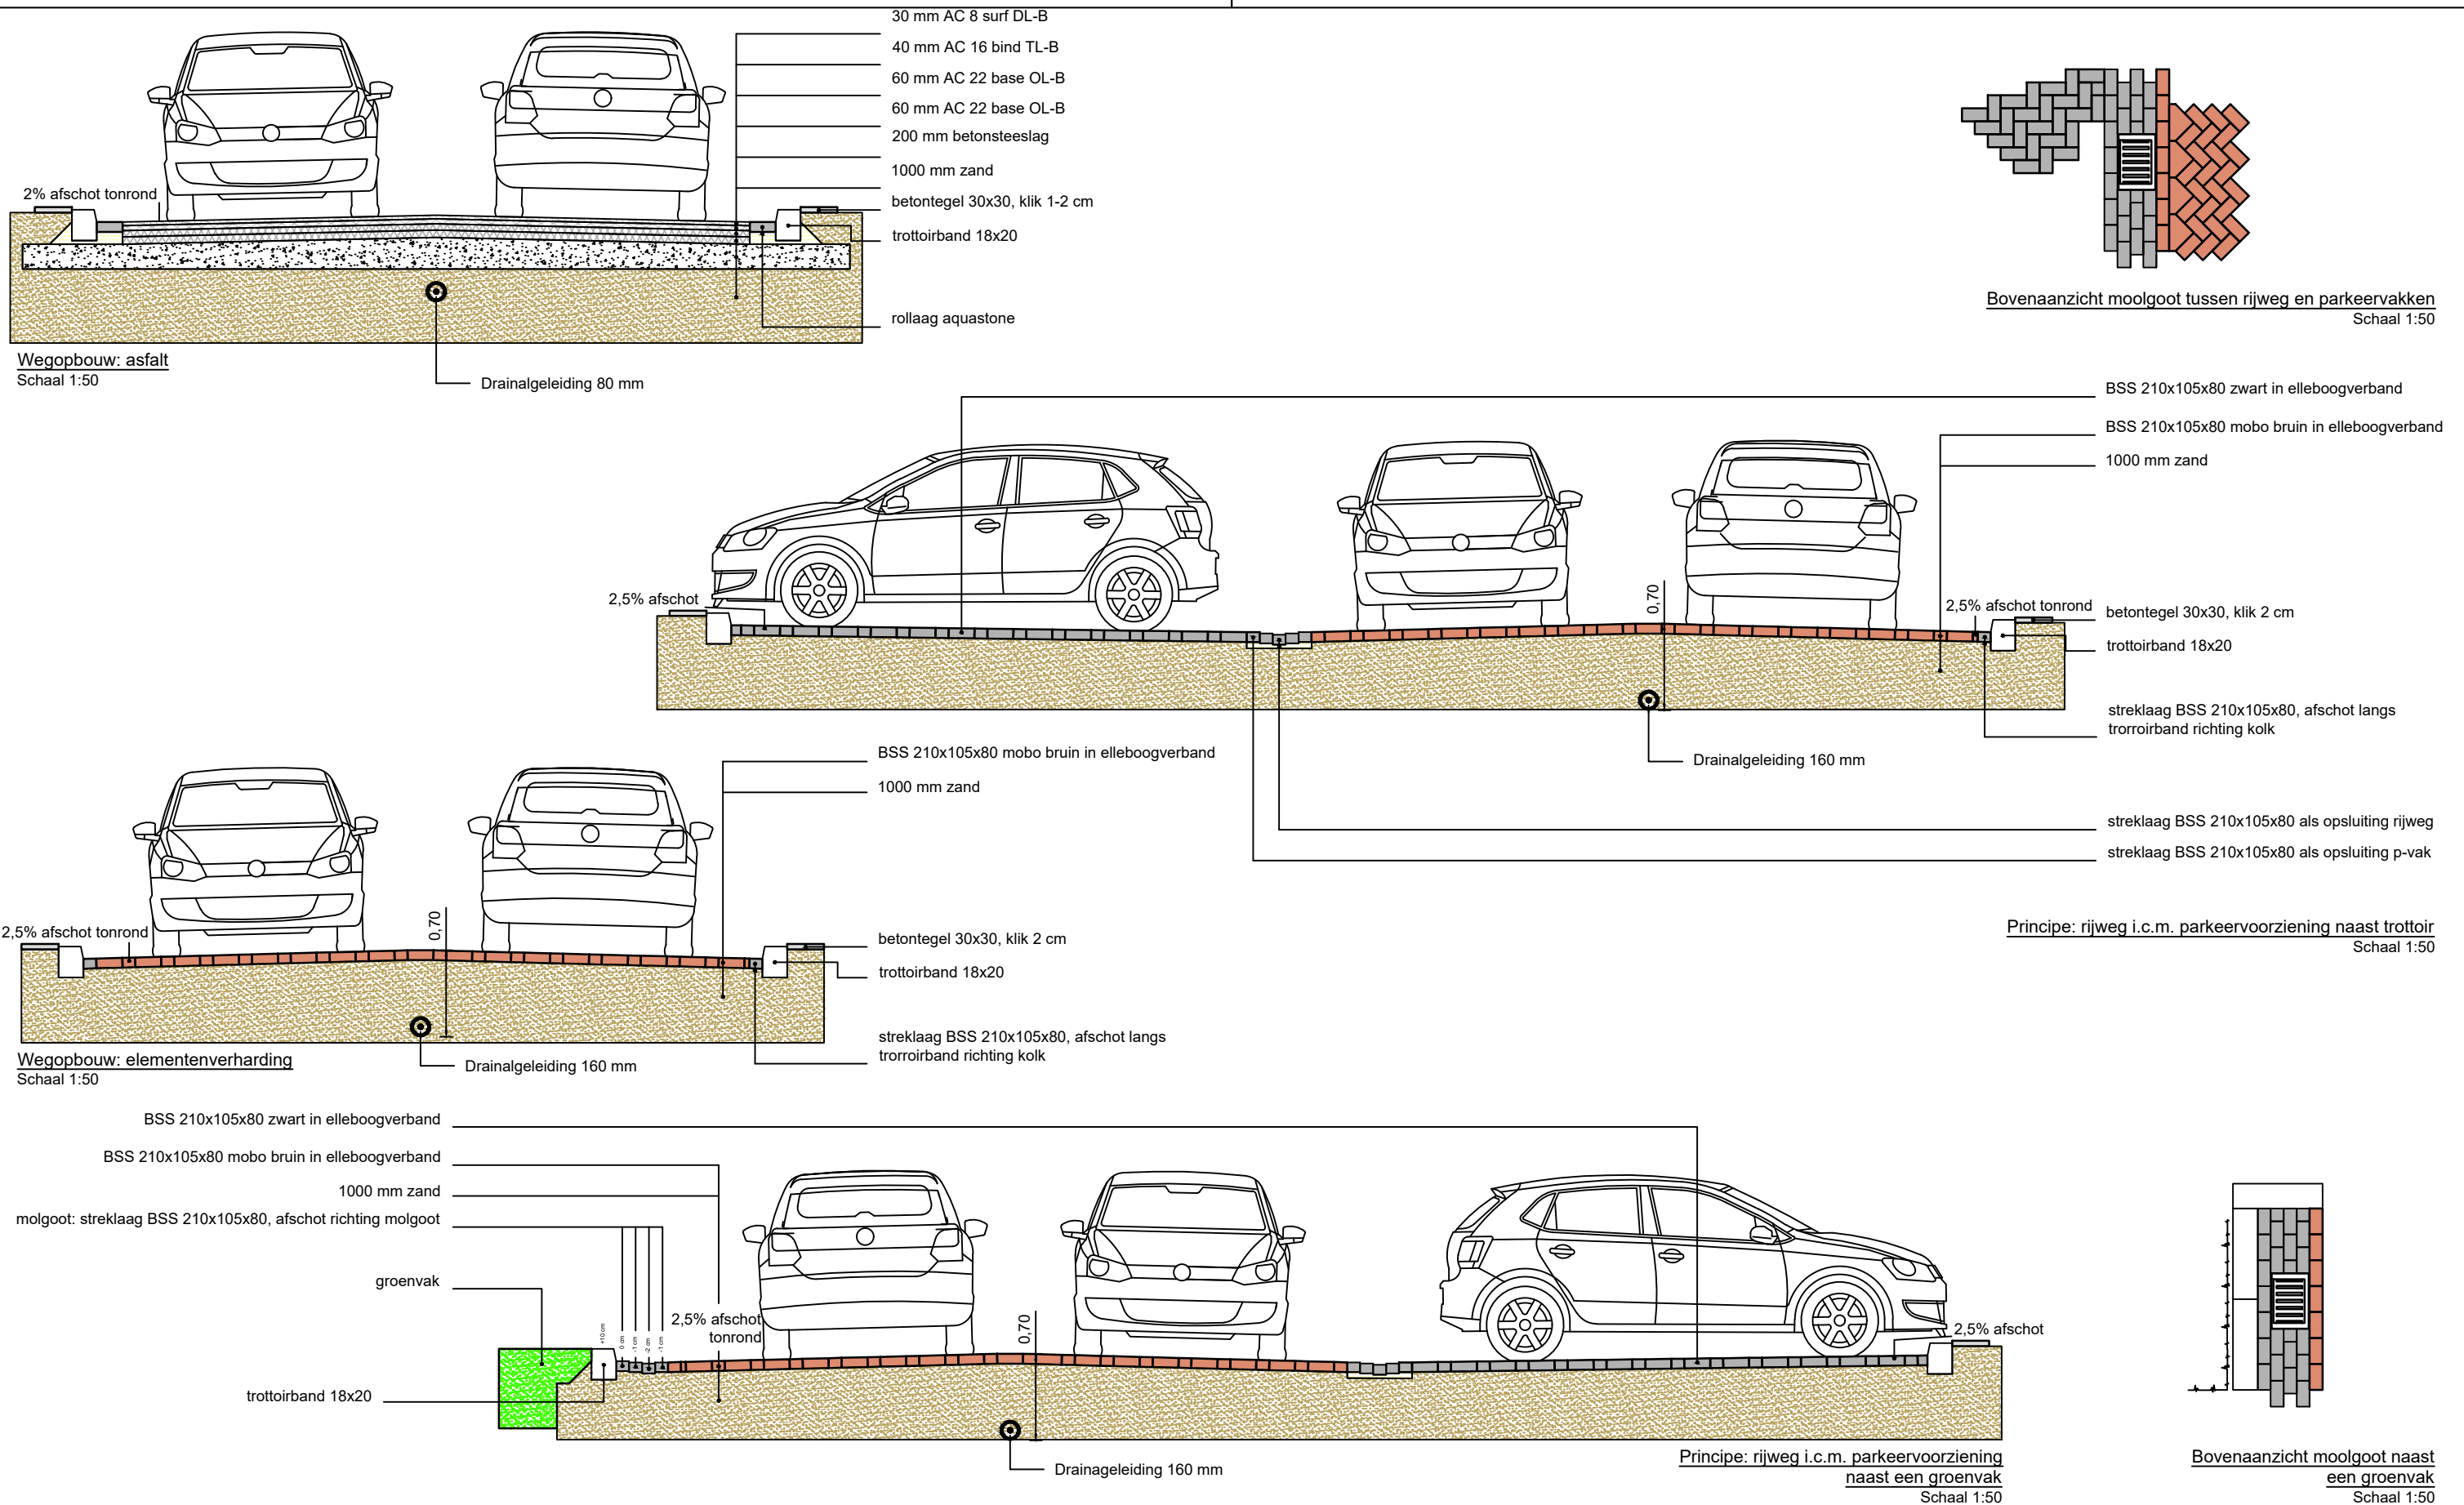


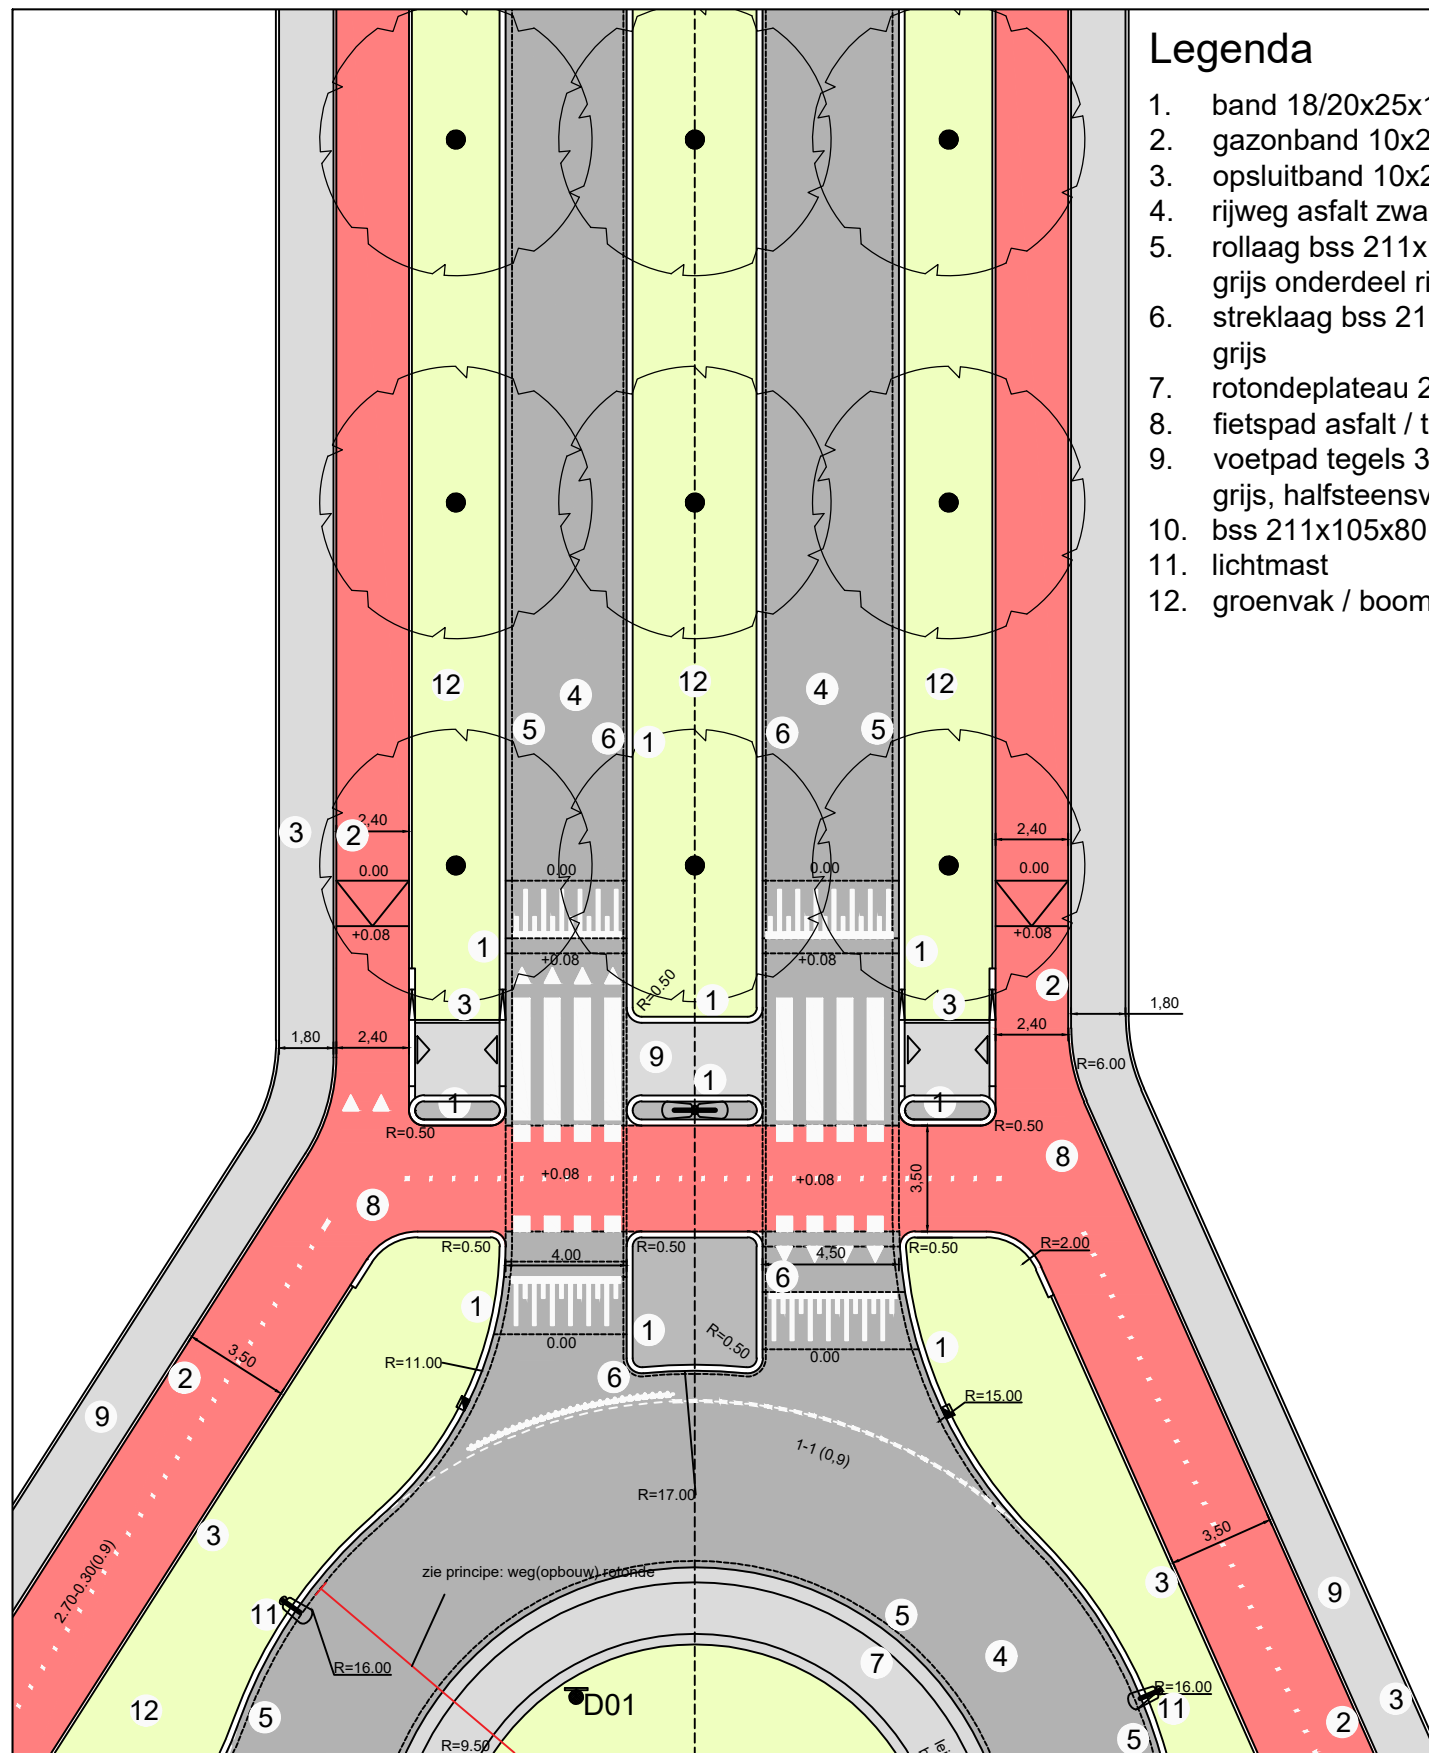


3-2-1 Hoofdweg 70 km/u
Schaal 1:250

Legenda

1. band 18/20x25x100, kleur grijs
2. gazonband 10x20x100, kleur grijs
3. opsluitband 10x20x100, kleur grijs
4. rijweg asfalt zwart
5. rollaag bss 211x105x80, kleur grijs onderdeel rijweg
6. streklaag bss 211x105x80, kleur grijs
7. rotondeplateau 250
8. fietspad asfalt / tegels 30x30 rood
9. voetpad tegels 30x30x7, kleur grijs, halfsteensverband
10. bss 211x105x80, kleur grijs
11. lichtmast
12. groenvak / boom

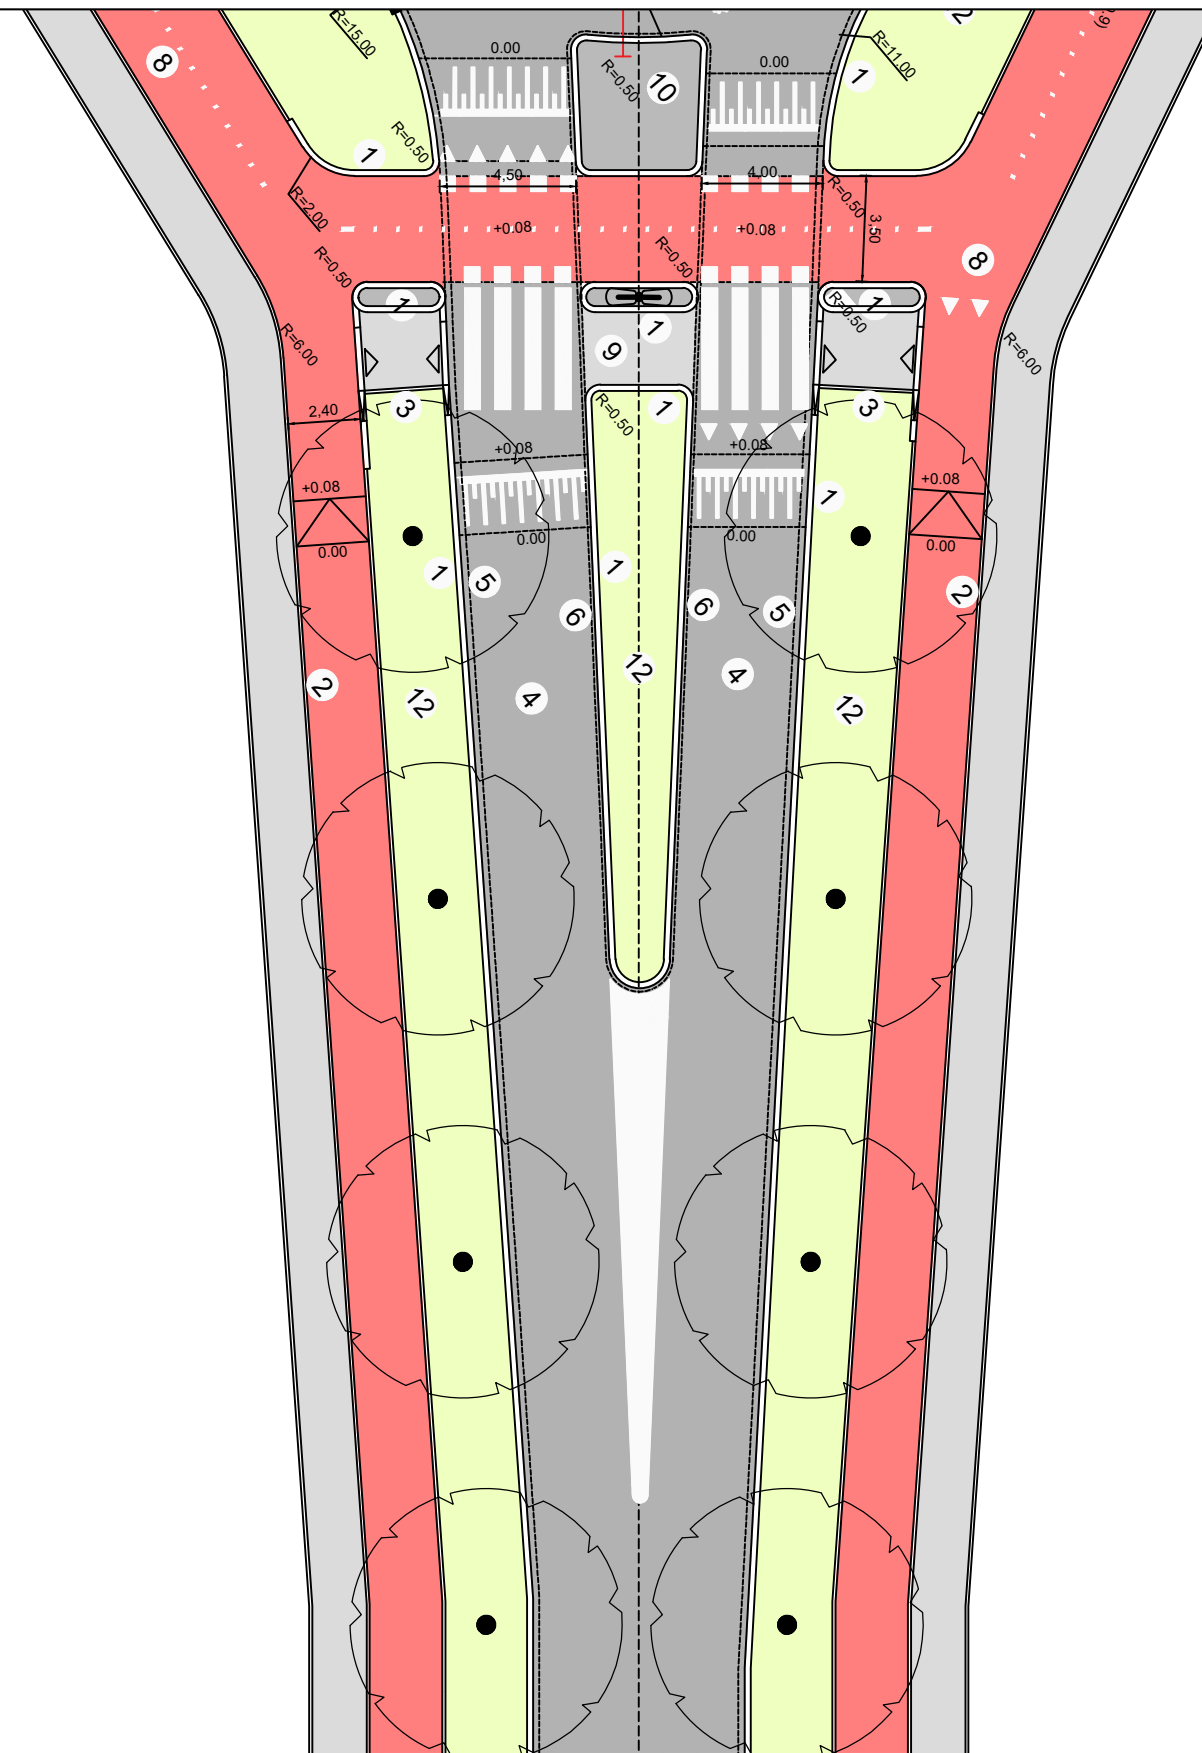

3-2-2 Gebiedsontsluitingsweg 50 km/u
Schaal 1:250

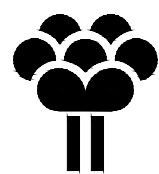


Gemeente
Zoetermeer

Hoofdweg en gebiedsontsluitingsweg

getekend: Gemeente Zoetermeer
gewijzigd:
datum: 3-4-2026

formaat: A3
schaal: 1:250
volgnummer: 3-2

Stadsbeheer 2026

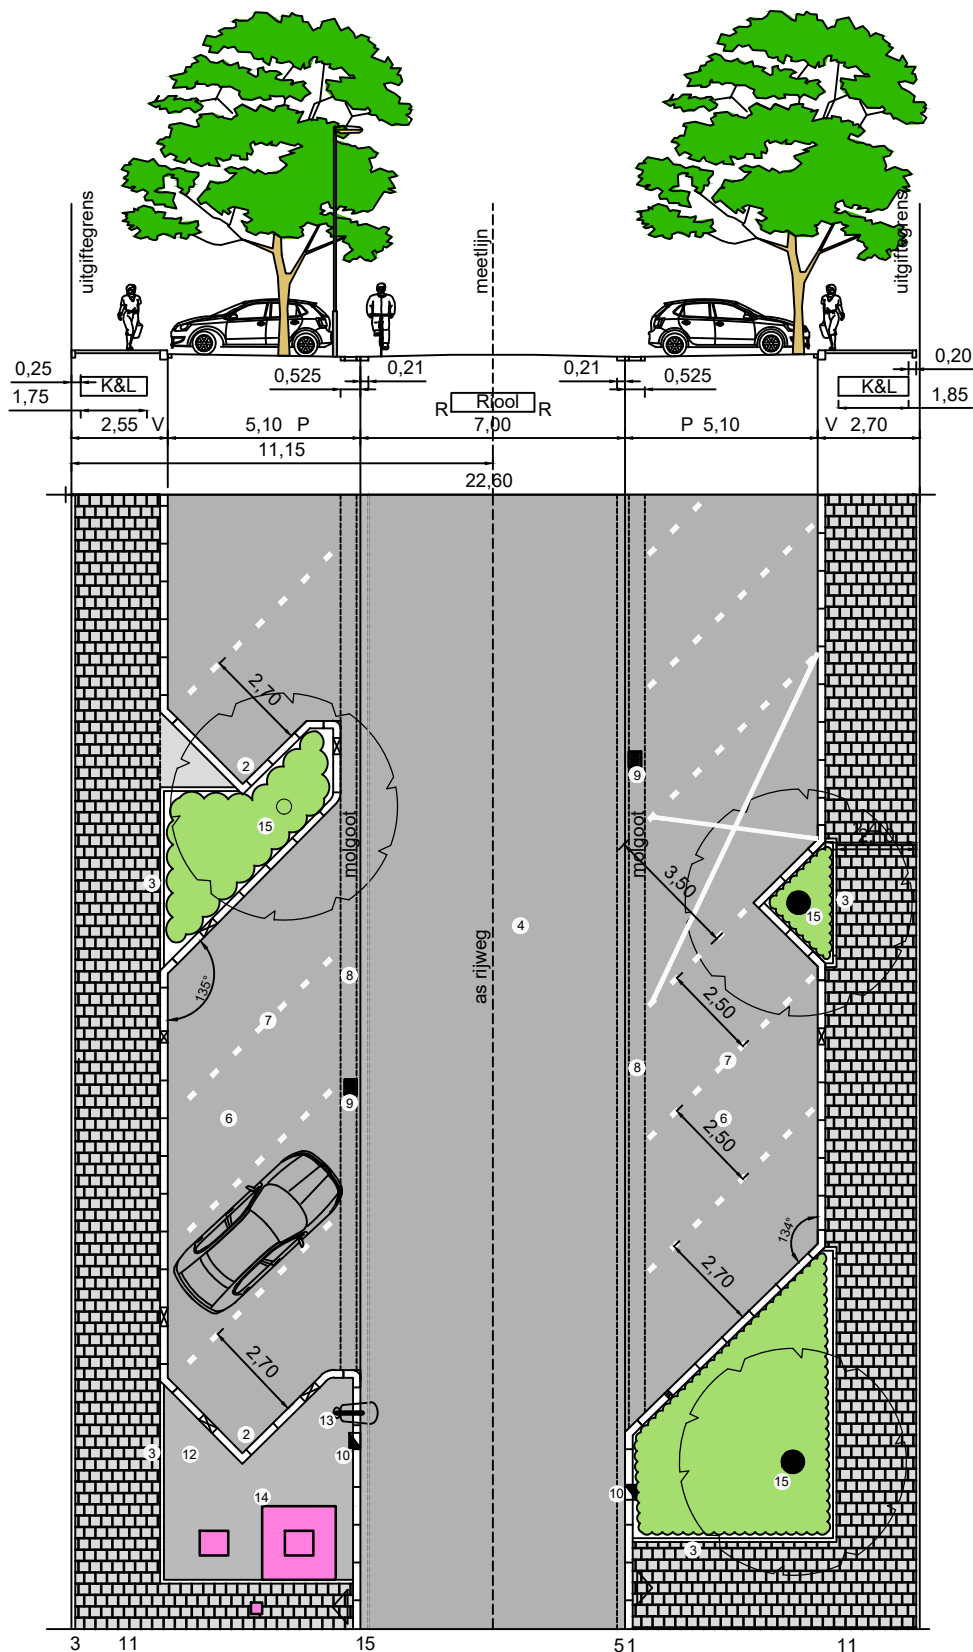


Legenda

1. band 18/20x25x100, kleur grijs.
2. hoek- en bochtstukken 18/20x25x45x45, kleur grijs.
3. opsluitband 10x20x100, kleur grijs.
4. rijweg asfalt zwart.
5. rollaag bss 211x105x80, kleur grijs onderdeel rijweg.
6. parkeerplaats bss 211x105x80, kleur antraciet, keperverband.
7. parkeer markering bss 211x105x80, kleur wit.
8. molgoot bss 211x105x80, kleur zwart 5x streklaag (onderdeel parkeren).
9. straatkolk 30x45.
10. trottoirkolk.
11. voetpad tegels 300x300x70, kleur grijs, halfsteensverband.
12. bss 211x105x80, kleur grijs, elleboogverband.
13. lichtmast.
14. ondergrondse huisvuilverzameling (rest/ gft) met bedieningszuil.
15. groenvak/ boom.
16. mindervalideparkeervak, kruis doorgetrokken streep bss wit.
17. RVV verkeersbord E06.

- band (halve band)
 band 18/20x25x50, R=0.50
 verlaagde band

Schuinparkeren 4,95 meter
wijkweg (bomen langs de weg)
Schaal 1:200

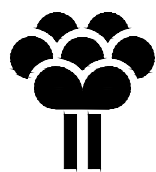

Gemeente
Zoetermeer


Wijkweg schuinparkeren
Schuinparkeren

Deze tekening heeft geen juridische werking, zodat daaraan geen rechten ontleend kunnen worden. Wijzigingen voorbehouden.

getekend: Gemeente Zoetermeer
gewijzigd:
datum: 3-4-2026

formaat: A3
schaal: 1:200
volgnummer: 3-3

Stadsbeheer 2026

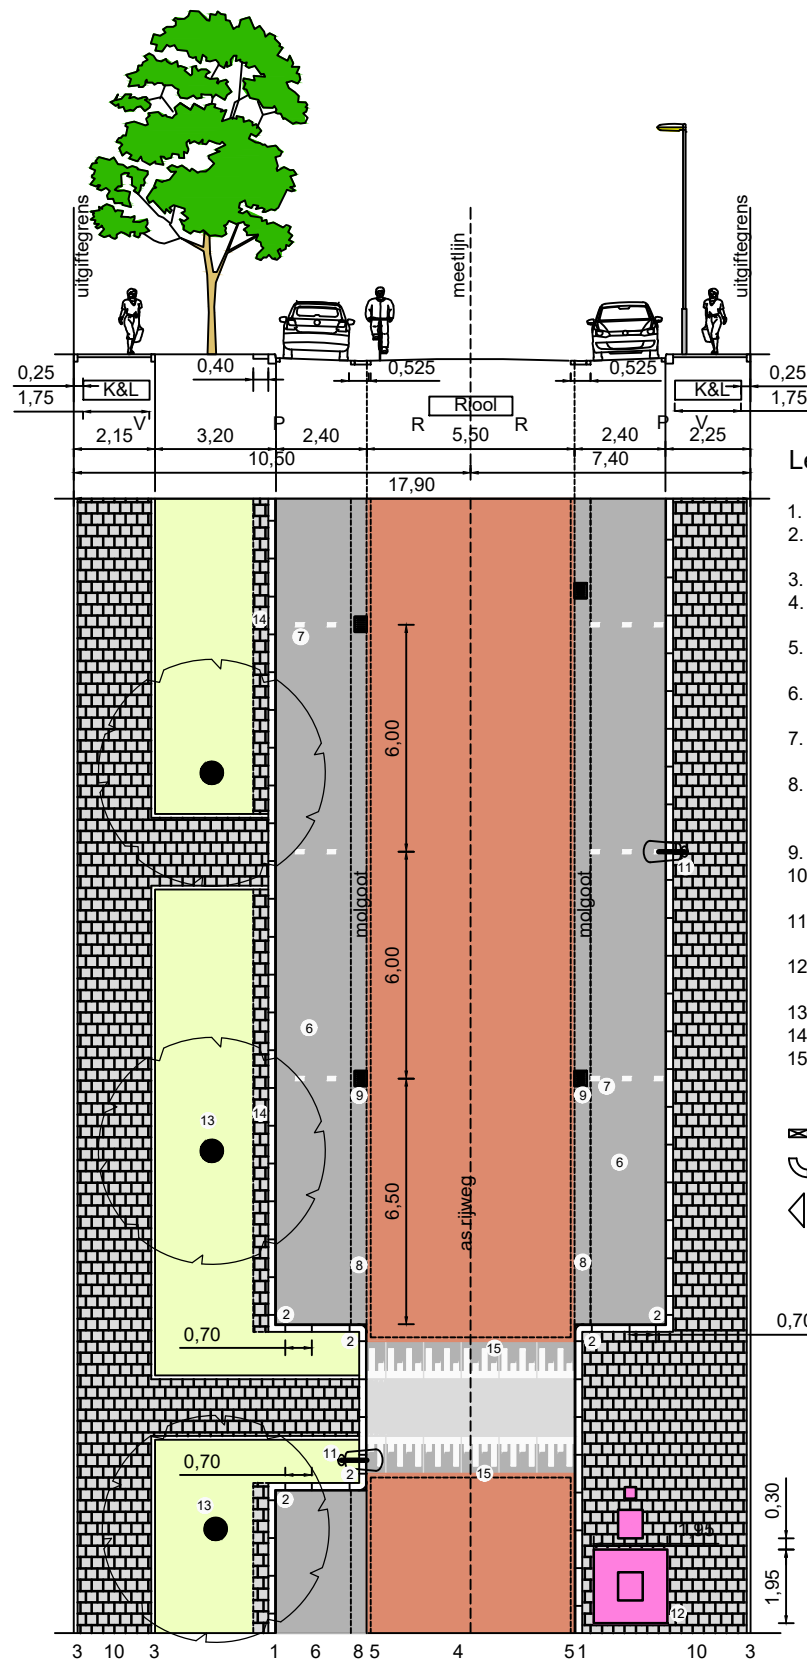


Legenda

- band 18/20x25x100, kleur grijs.
- hoek- en bochtstukken 18/20x25x45x45, kleur grijs.
- opsluitband 10x20x100, kleur grijs.
- rijweg bss 211x105x80, kleur mobobruin keperverband.
- streklaag bss 211x105x80, kleur mobobruin onderdeel rijweg.
- parkeerplaats bss 211x105x80, kleur antraciet, elleboogverband.
- parkeer markering bss 211x105x80, kleur wit.
- molgoot bss 211x105x80, kleur antraciet 4x streklaag (onderdeel parkeren).
- straatkolk 30x45.
- voetpad tegels 300x300x70, kleur grijs, halfsteensverband.
- lichtmast/ eiland (4x hoekstukken (18/20x25x45x45).
- ondergrondse huisvuilverzameling (rest/ gft) met bedieningszuil.
- groenvak/ boom.
- tegels 40x60x12 grijs (uitstapstrook).
- drempel beton met taludmarkering wit.

- band (halve band)
- band 18/20x25x50, R=0.50
- verlaagde band

Langsparkeren 6,00 meter
wijkweg
Schaal 1:200

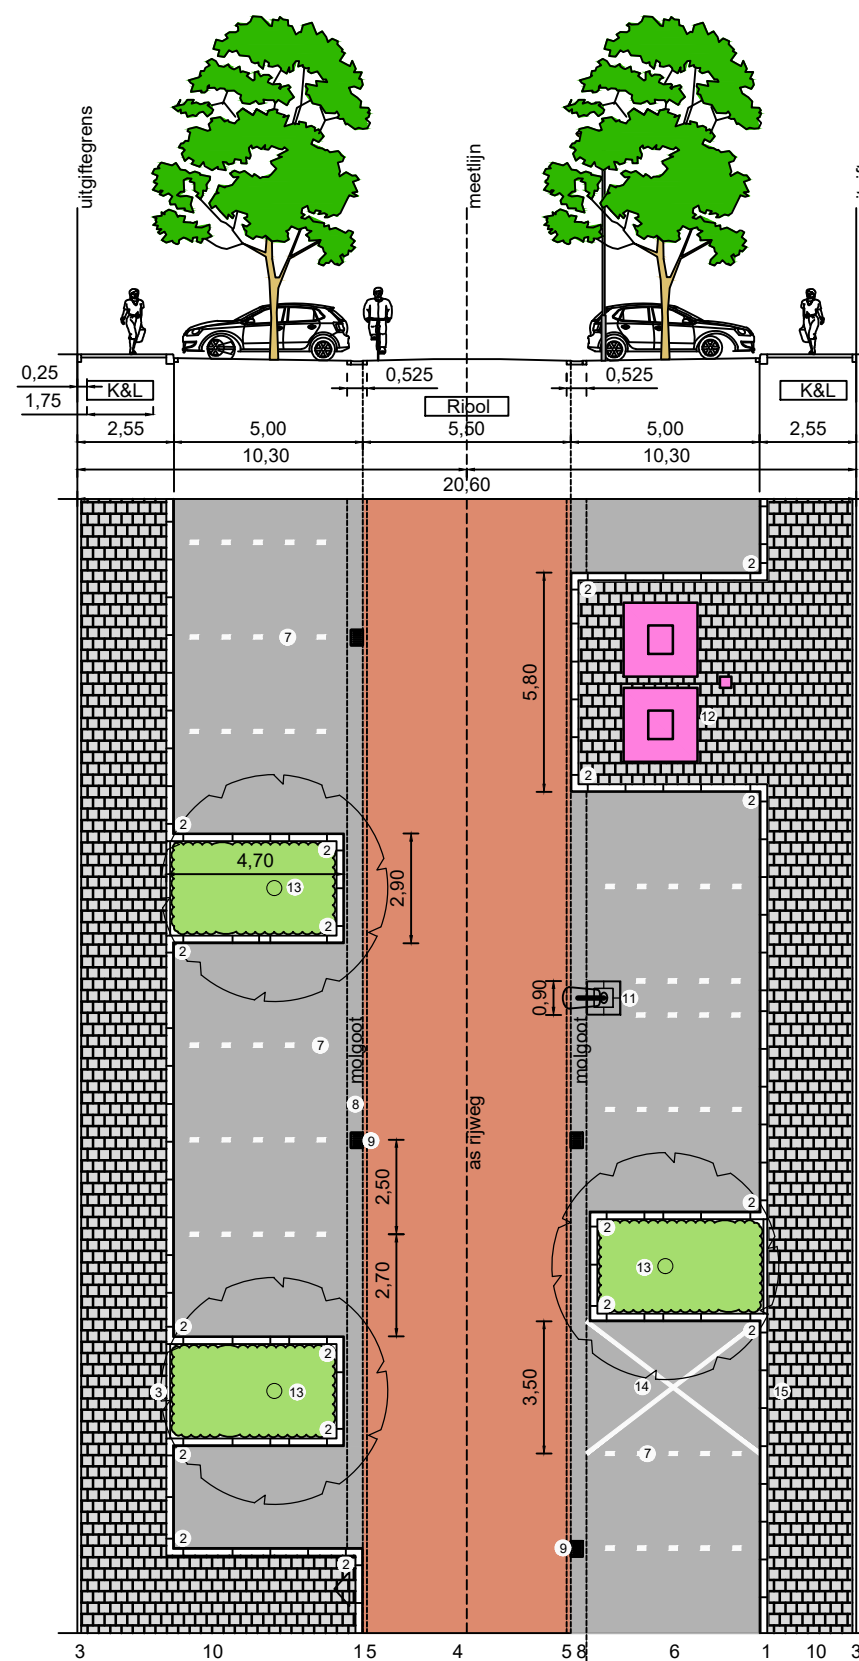


Legenda

- band 18/20x25x100, kleur grijs.
- hoek- en bochtstukken 18/20x25x45x45, kleur grijs.
- opsluitband 10x20x100, kleur grijs.
- rijweg bss 211x105x80, kleur mobobruin keperverband.
- streklaag bss 211x105x80, kleur mobobruin onderdeel rijweg.
- parkeerplaats bss 211x105x80, kleur antraciet, elleboogverband.
- parkeer markering bss 211x105x80, kleur wit.
- molgoot bss 211x105x80, kleur antraciet 4x streklaag (onderdeel parkeren).
- straatkolk 30x45.
- voetpad tegels 300x300x70, kleur grijs, halfsteensverband.
- lichtmast (4x hoekstukken (18/20x25x45x45).
- ondergrondse huisvuilverzameling (rest/ gft) met bedieningszuil.
- groenvak/ boom.
- invalidenparkeervak.
- RVV verkeersbord E06

- band (halve band)
- band 18/20x25x50, R=0.50
- verlaagde band

Haaksparkeren 5,00 meter
Schaal 1:200

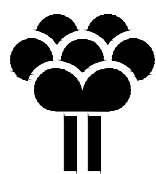


Gemeente
Zoetermeer

Woonstraat langs- en haaksparkeren

getekend: Gemeente Zoetermeer
gewijzigd: 3-4-2026
datum:

formaat: A3
schaal: 1:200
volgnummer: 3-4


Stadsbeheer 2026

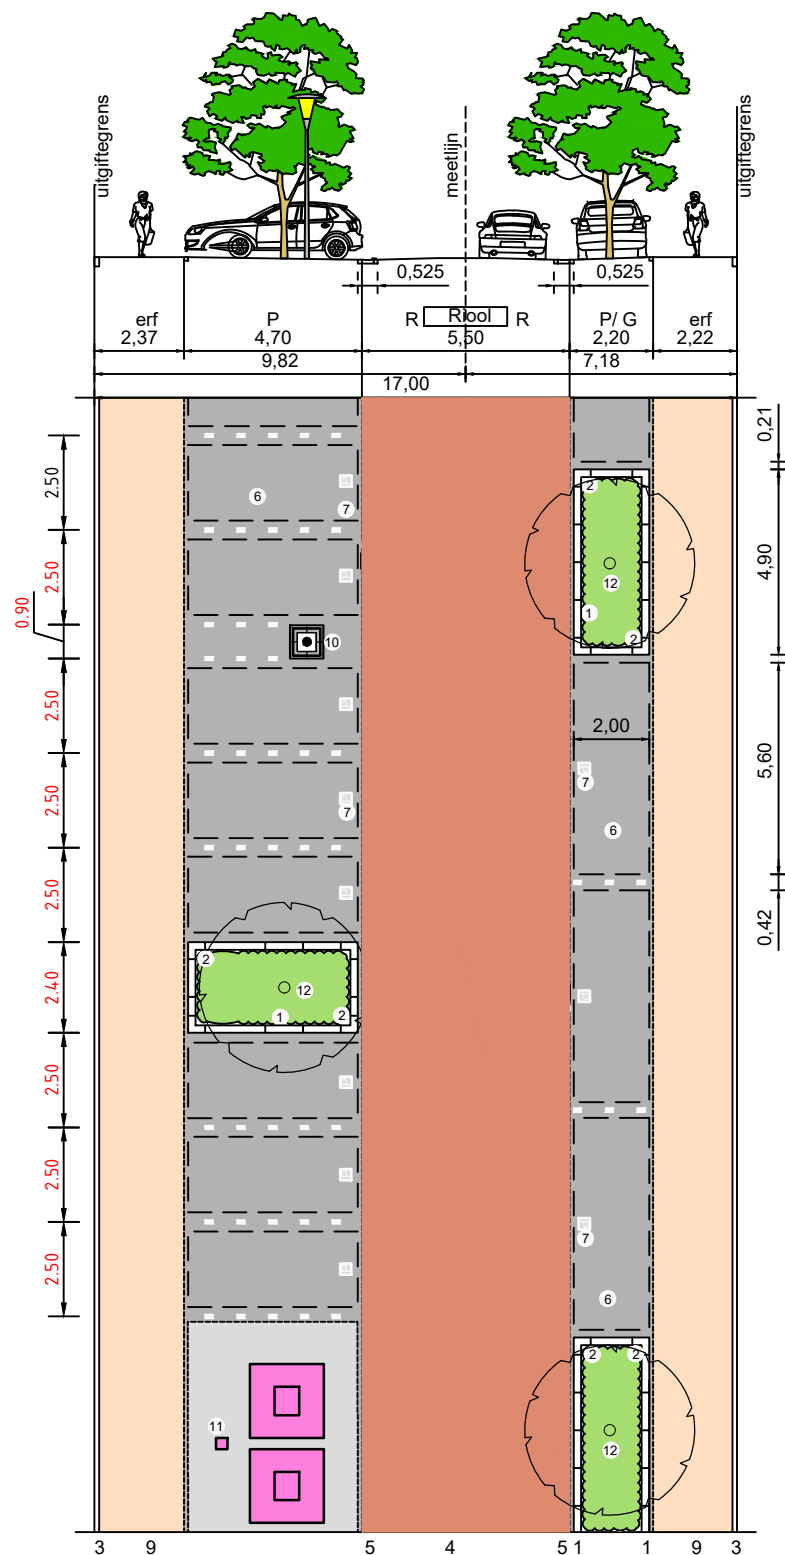

Legenda

1. band 18/20x25x100, kleur grijs.
2. hoek- en bochtstukken 18/20x25x45x45, kleur grijs.
3. opsluitband 12x25x100, kleur grijs.
4. rijweg bss 211x105x80, kleur grijs halfsteensverband of keperverband.
5. molgoot bss 211x105x80, kleur grijs 5x streklaag.
6. parkeerplaats bss 211x105x80, kleur antraciet, elleboogverband.
7. teksttegel P-wit 21x21 (woonerf).
8. straatkolk 30x45.
9. rijweg bss 211x105x80, kleur mobobruin keperverband.
10. lichtmast/ eiland (4x hoekstukken (18/20x25x45x45).
11. ondergrondse huisvuilverzameling (rest/ gft) met bedieningszuil.
12. groenvak/ boom.

Haaks- en langsparkeren
Schaal 1:200

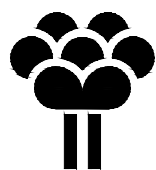


Gemeente
Zoetermeer
Woonerf
Haaks- en langsparkeren

getekend: Gemeente Zoetermeer
gewijzigd:
datum: 3-4-2026




formaat: A3
schaal: 1:200
volnummer: 3-5

Stadsbeheer 2026

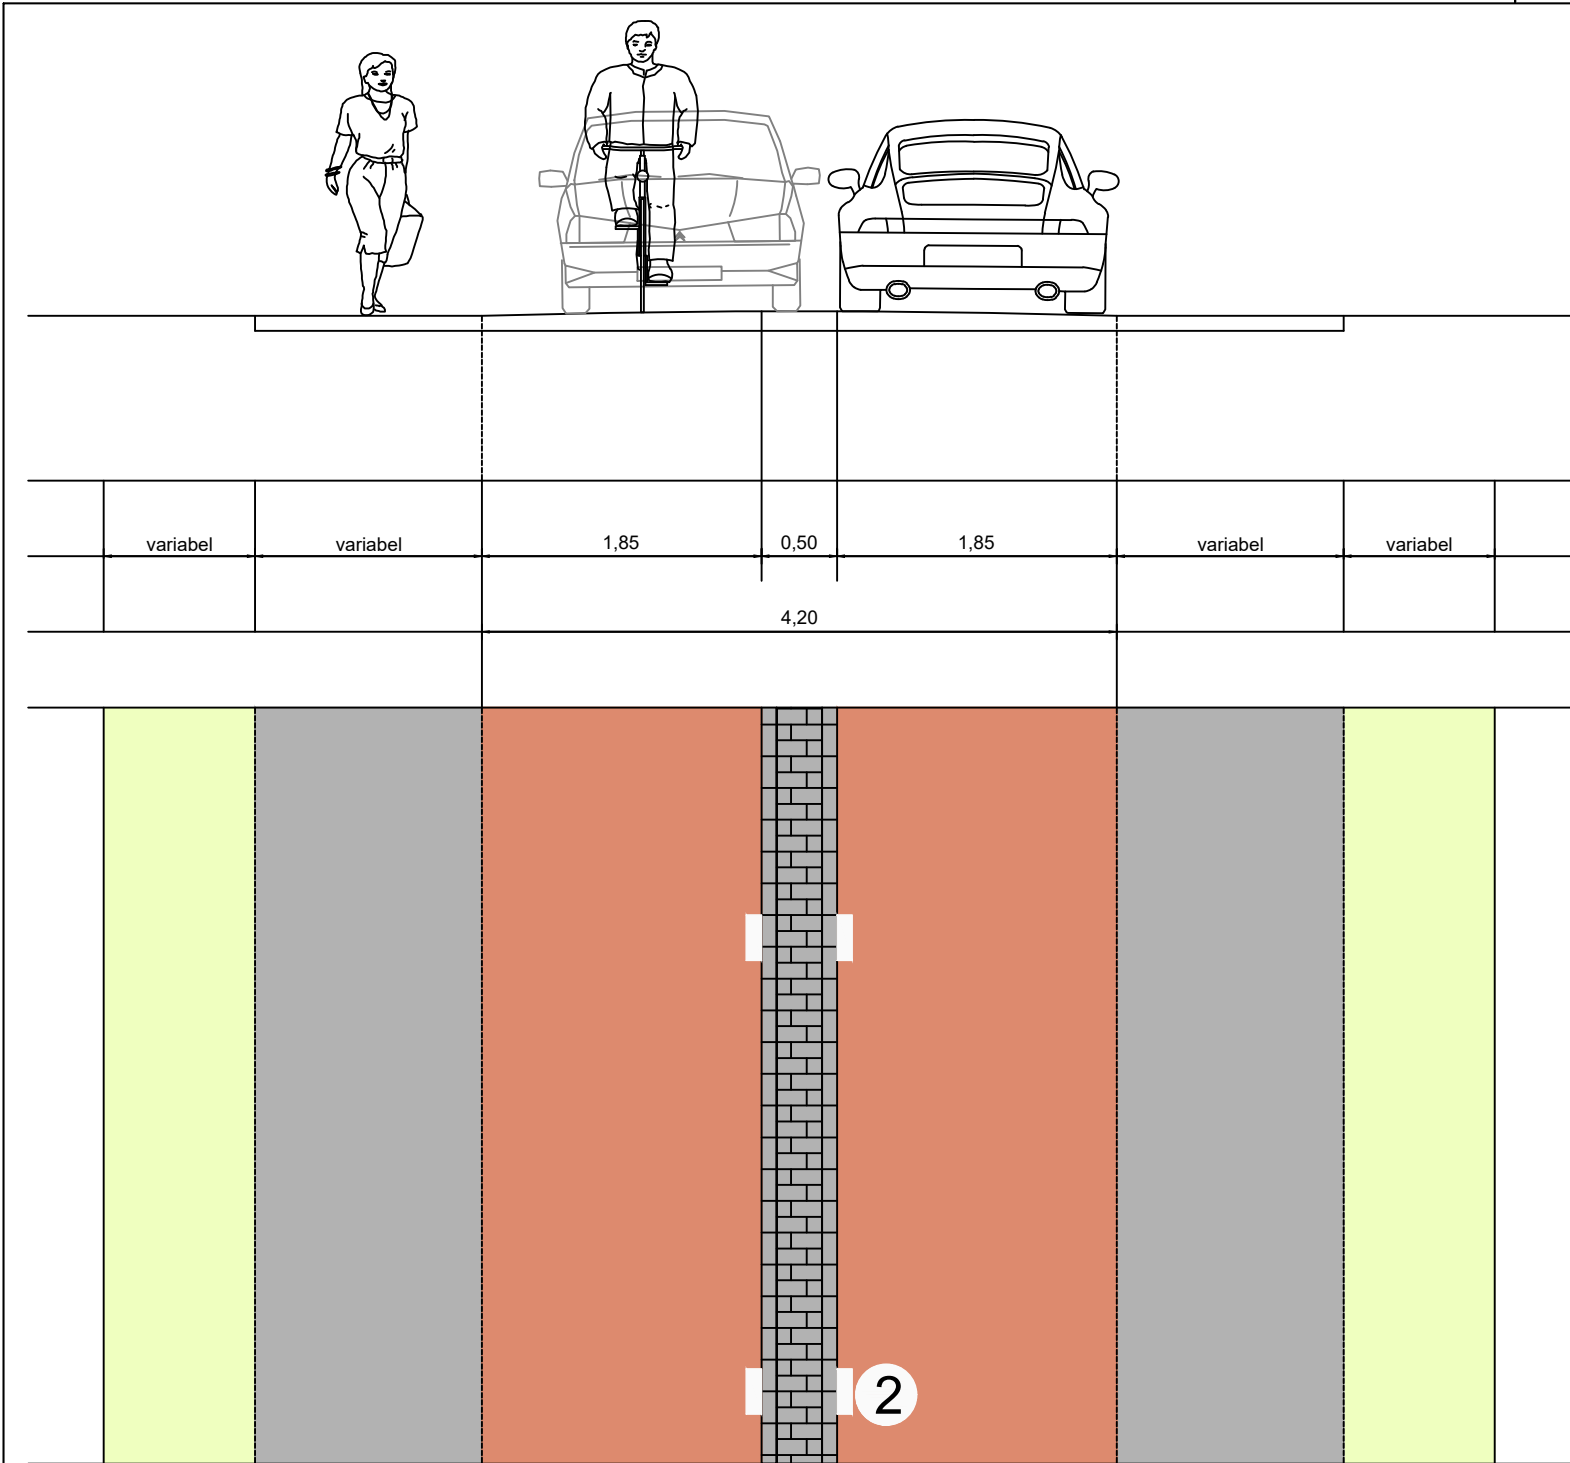


1. aanbrengen rood thermoplast op asfalt (fietsstrook)
2. aanbrengen witte markering 0,3-2,70(0,10).
3. aanbrengen streetprint, (bss formaat)
4. rest verharding asfalt (variabel).

Fietsstraat
Schaal 1:50

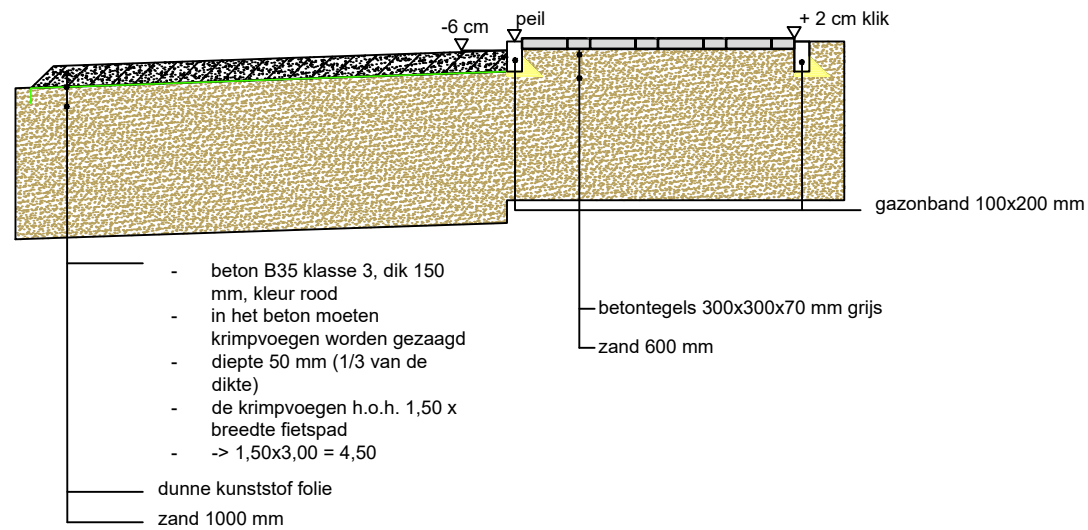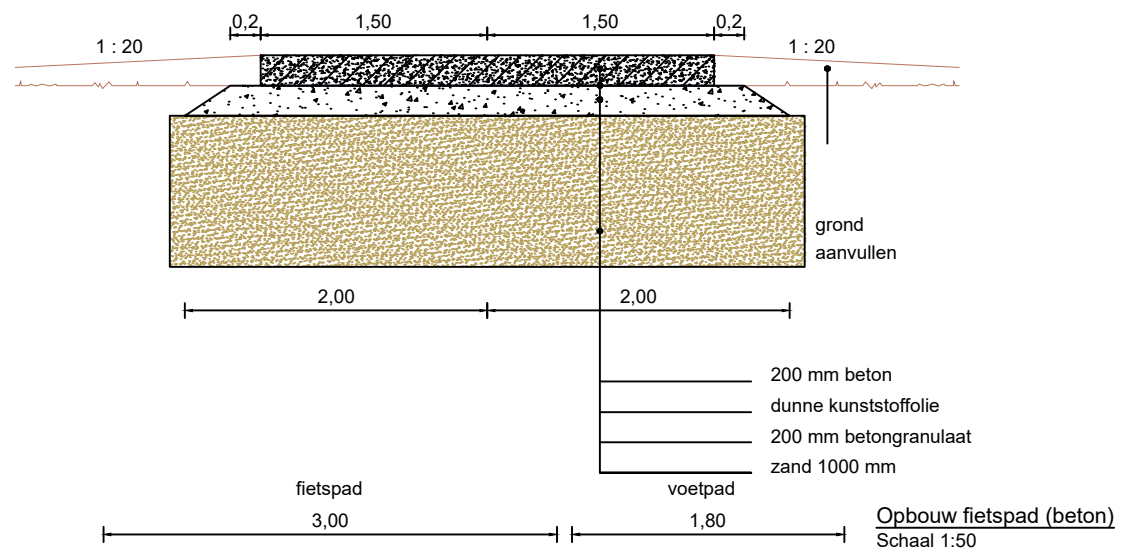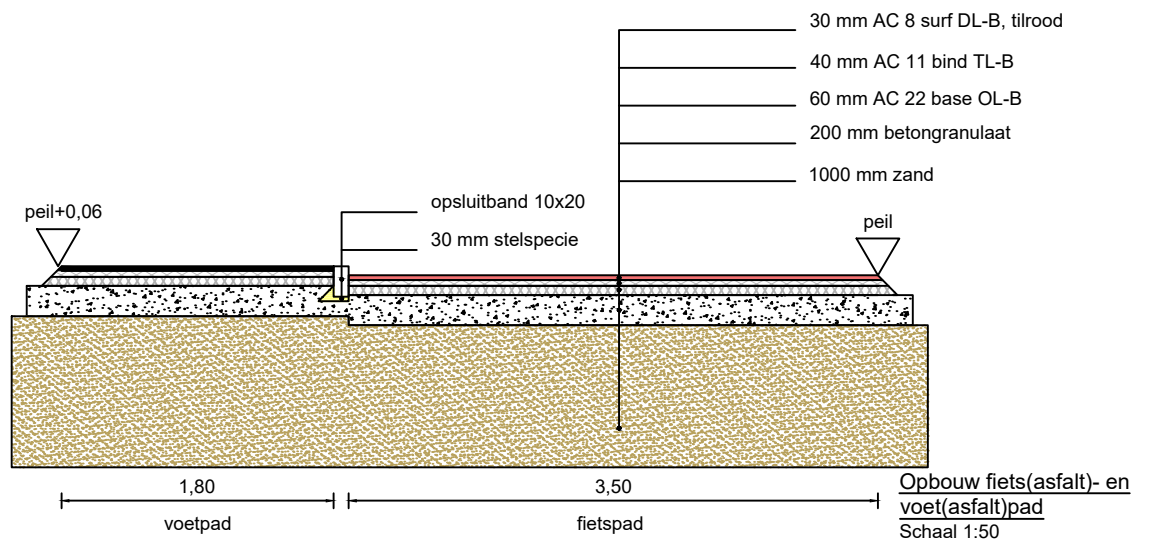


Opbouw fiets(beton)- en voet(tegel)pad
Schaal 1:50

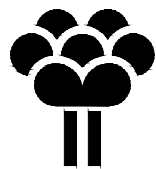


Gemeente
Zoetermeer
Fiets- en voetpaden

getekend: Gemeente Zoetermeer
gewijzigd: 3-4-2026
datum: formaat: A3
schaal: 1:50
volgnummer: 3-6


Stadsbeheer 2026

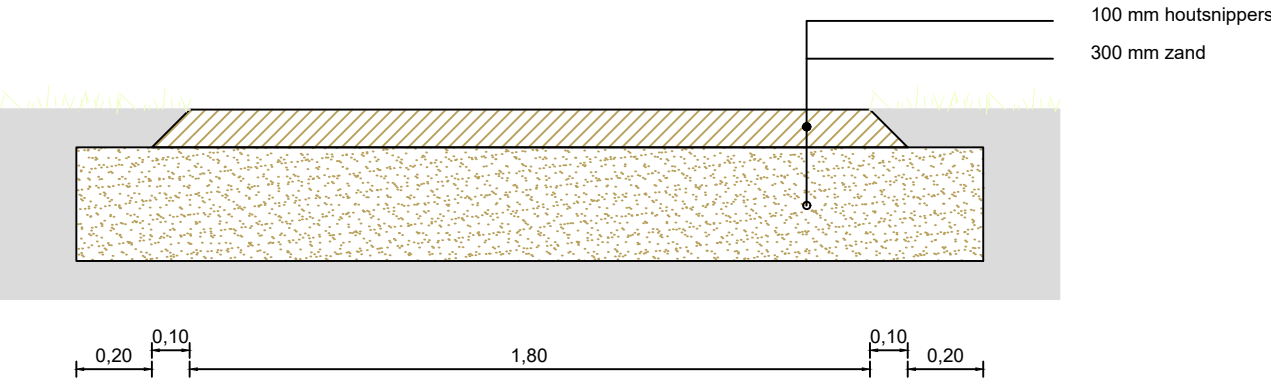


Voetpad met houtsnippers
Schaal 1:20

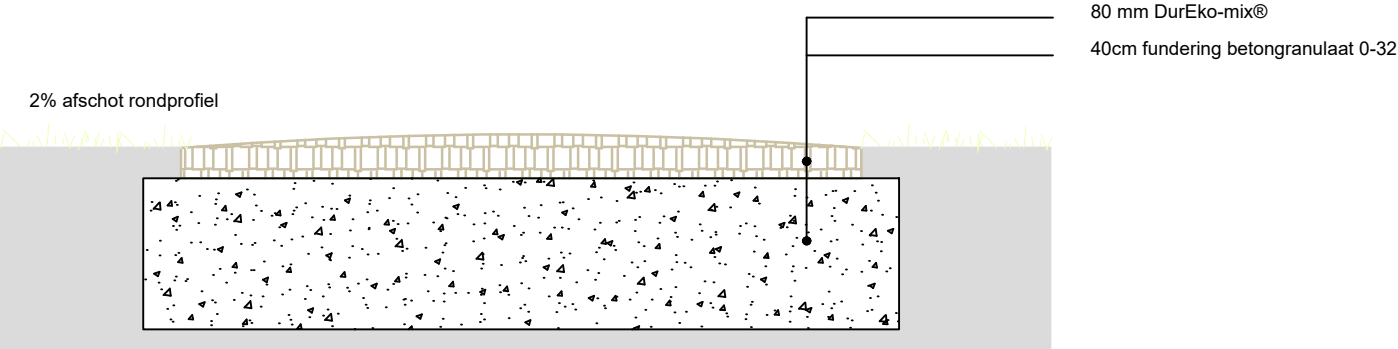

Voetpad met DurEko-mix®
Schaal 1:20

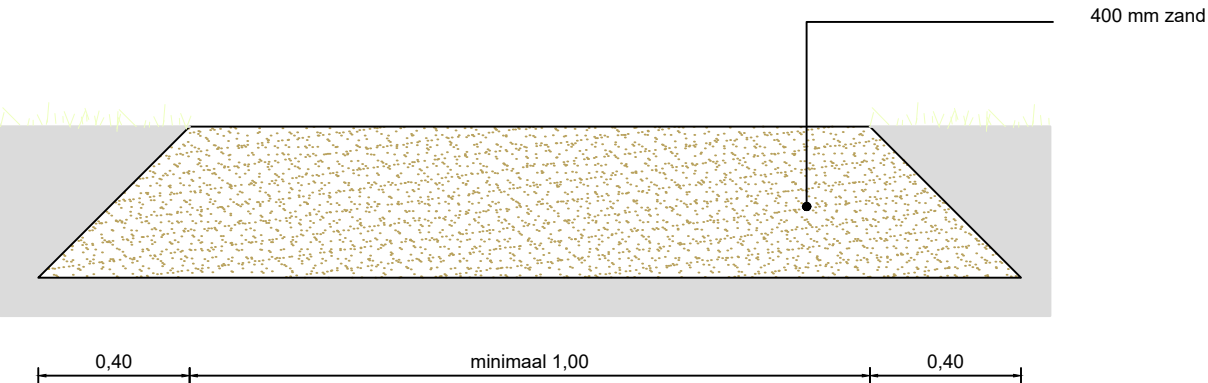

Ruiterpad
Schaal 1:20

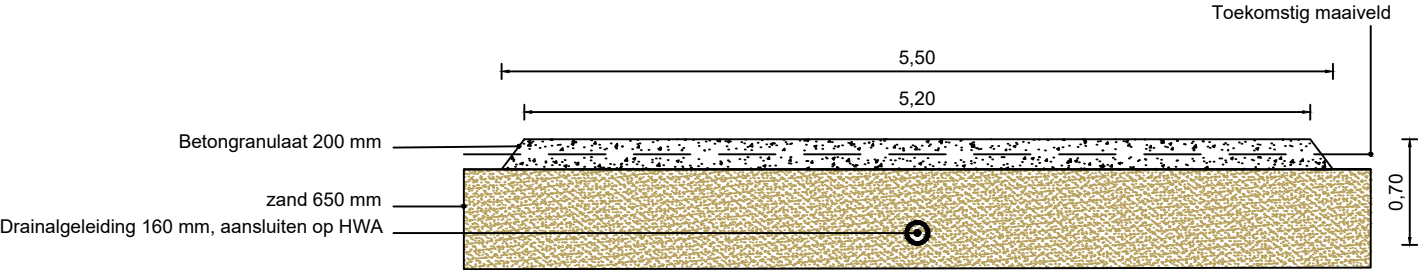

Bouwweg met fundering
betongranulaat
Schaal 1:50




Gemeente
Zoetermeer
Halfverharde paden - bouwweg


getekend: Gemeente Zoetermeer
gewijzigd: 3-4-2026
datum: 3-4-2026

formaat: A3
schaal: 1:20/1:50
volgnummer: 3-7

Stadsbeheer 2026

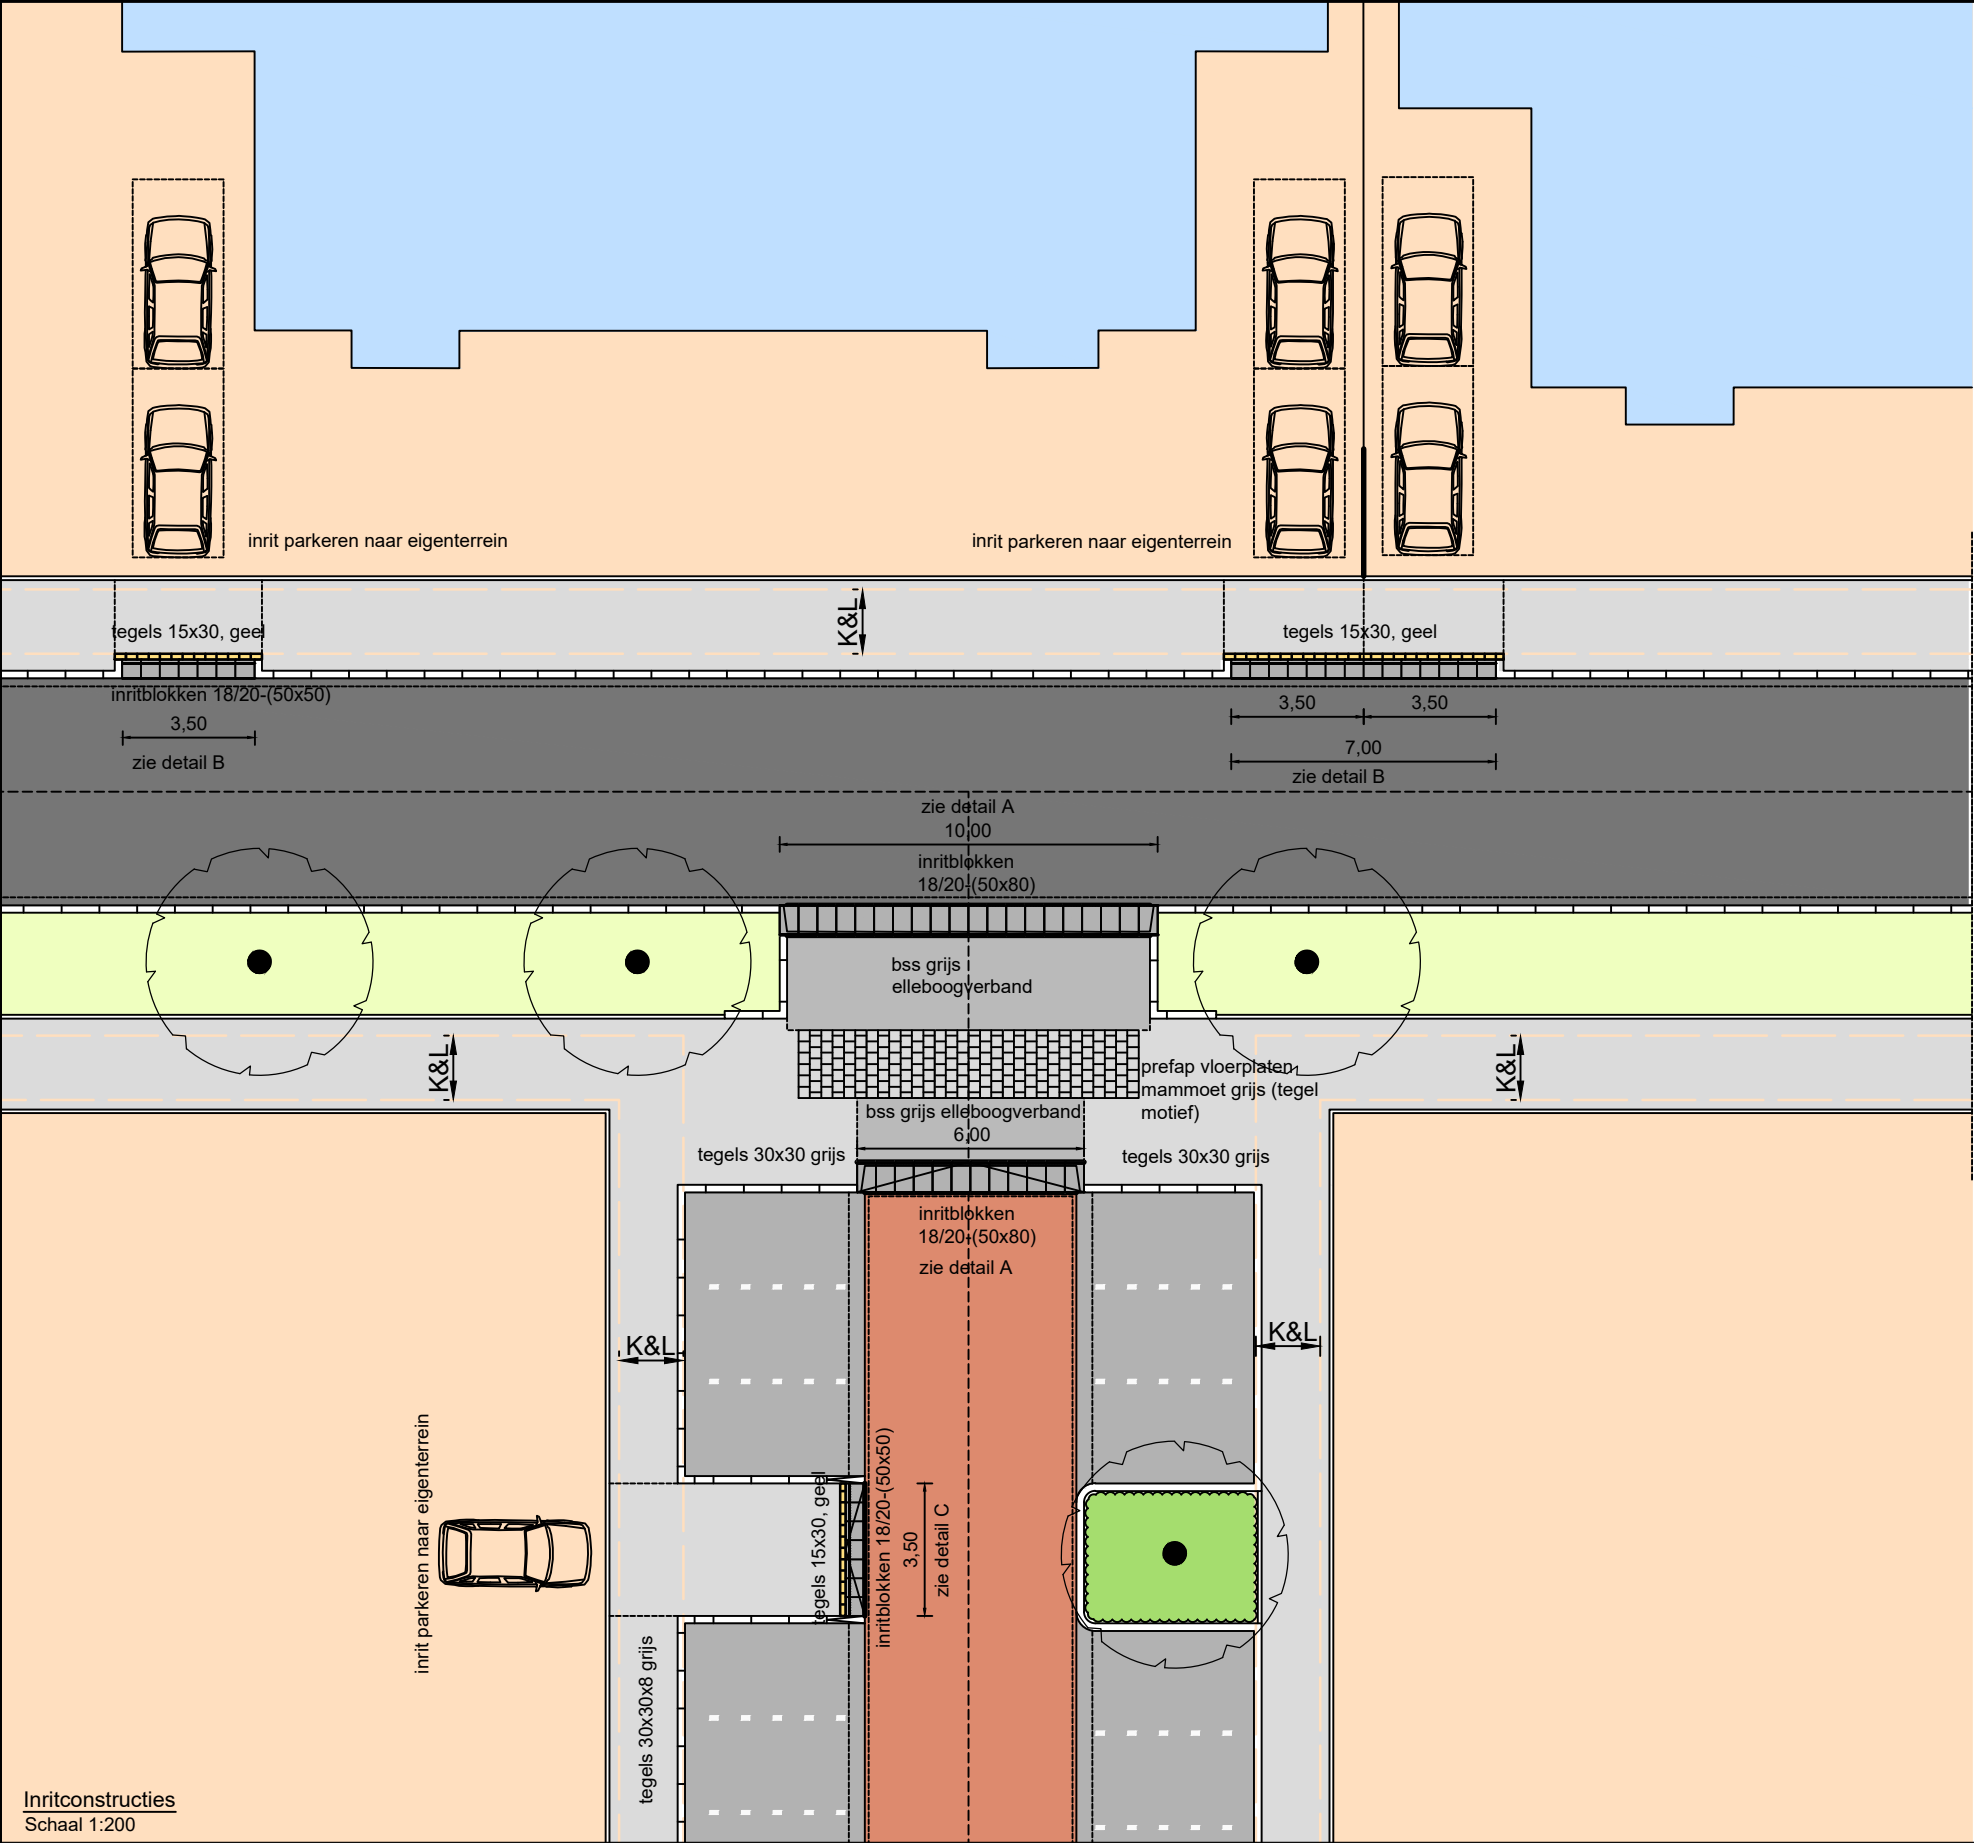

Inritconstructies
Schaal 1:200

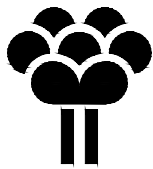


Gemeente
Zoetermeer

Inritconstructies
Situatie

Deze tekening heeft geen juridische werking, zodat daaraan geen rechten ontleend kunnen worden. Wijzigingen voorbehouden.


getekend: Gemeente Zoetermeer
gewijzigd: 3-4-2026
datum:
formaat: A3
schaal: 1:200
volnummer: 3-8

Stadsbeheer 2026

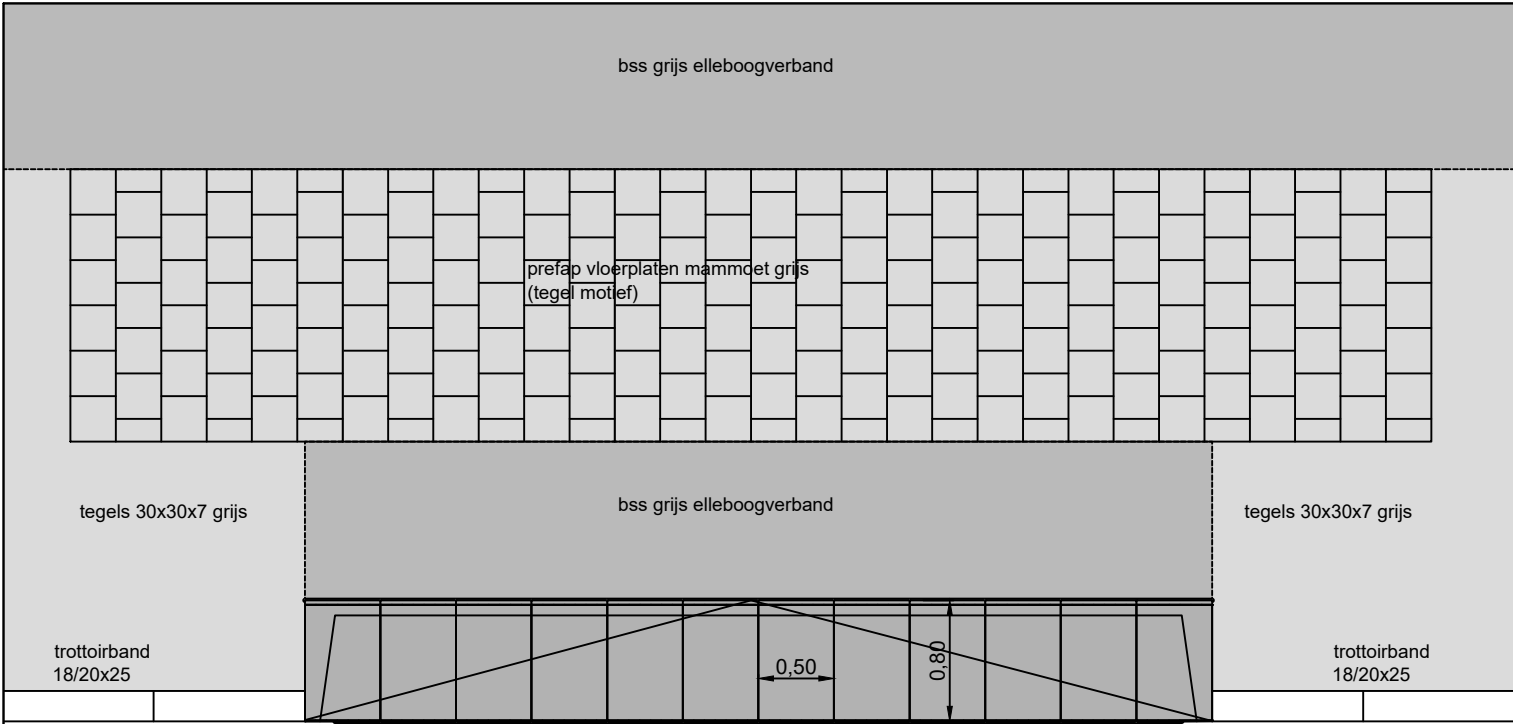


Detail A: inritconstructie
Schaal 1:50


inritblokken 18/20-(50x80x18) antraciet
zwart tbv. zijstraat (en) openbare gebied

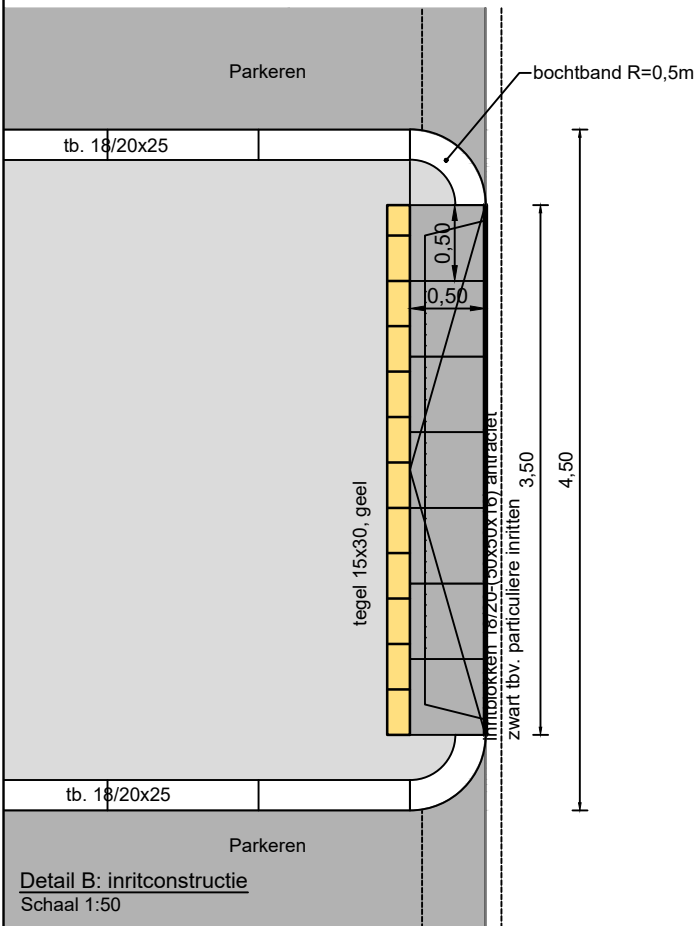


Detail B: inritconstructie
Schaal 1:50

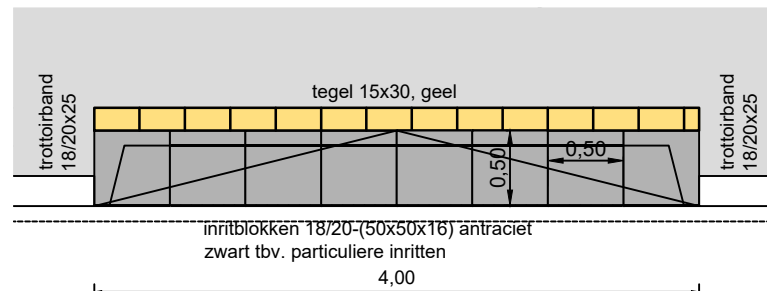


Detail C: inritconstructie
Schaal 1:50

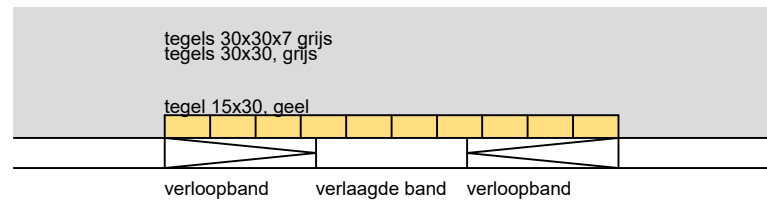


Detail D: inritconstructie
Schaal 1:50

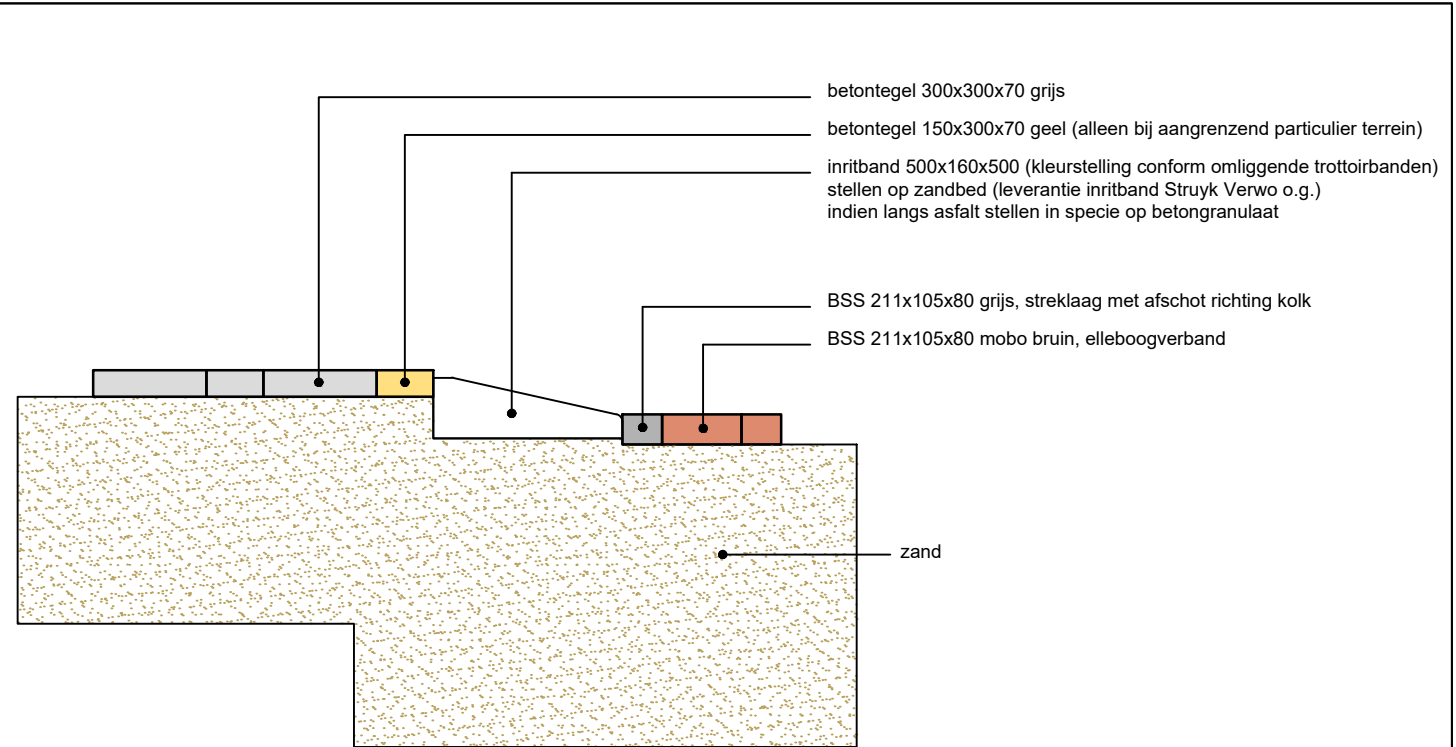

Inritblok 50x16x50 (inritten bij particulieren)
Schaal 1:20

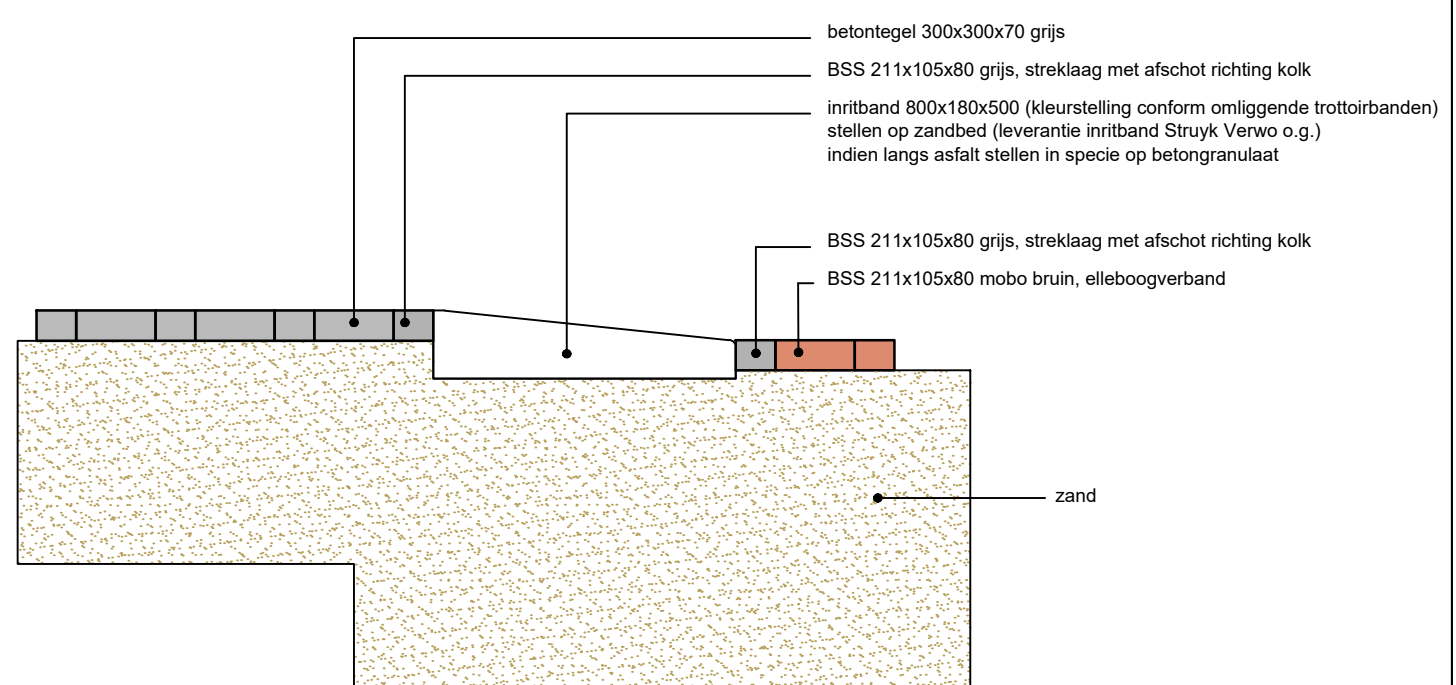

Inritblok 80x18x50
Schaal 1:20

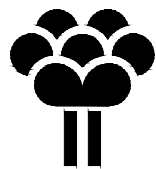

Gemeente
Zoetermeer
Inritconstructies
Opbouw

Deze tekening heeft geen juridische werking, zodat daaraan geen rechten ontleend kunnen worden. Wijzigingen voorbehouden.



getekend: Gemeente Zoetermeer
gewijzigd:
datum: 3-4-2026

formaat: A3
schaal: 1:50/1:20
volgnummer: 3-9

Stadsbeheer 2026


Legenda

band 18/20x25x100, kleur grijs
gazonband 10x20x100, kleur grijs
opsluitband 10x20x100, kleur grijs
rijweg asfalt zwart
rolraag bss 211x105x80, kleur grijs
grijs onderdeel rijweg
streklag bss 211x105x80, kleur grijs
grijs
rotondeplateau 250
fietspad asfalt / tegels 30x30 rood
voetpad tegels 30x30x7, kleur grijs, halfsteensverband
bss 211x105x80, kleur grijs
lichtmast
groenvak / boom

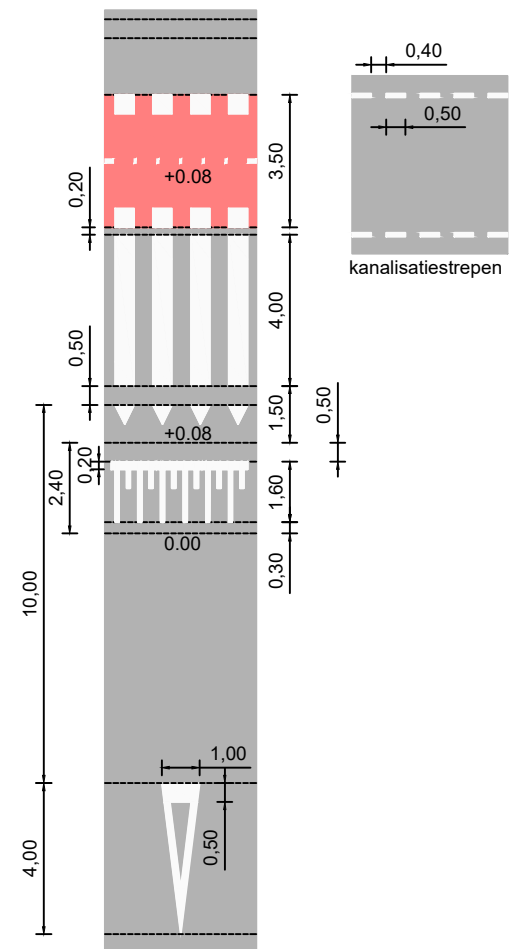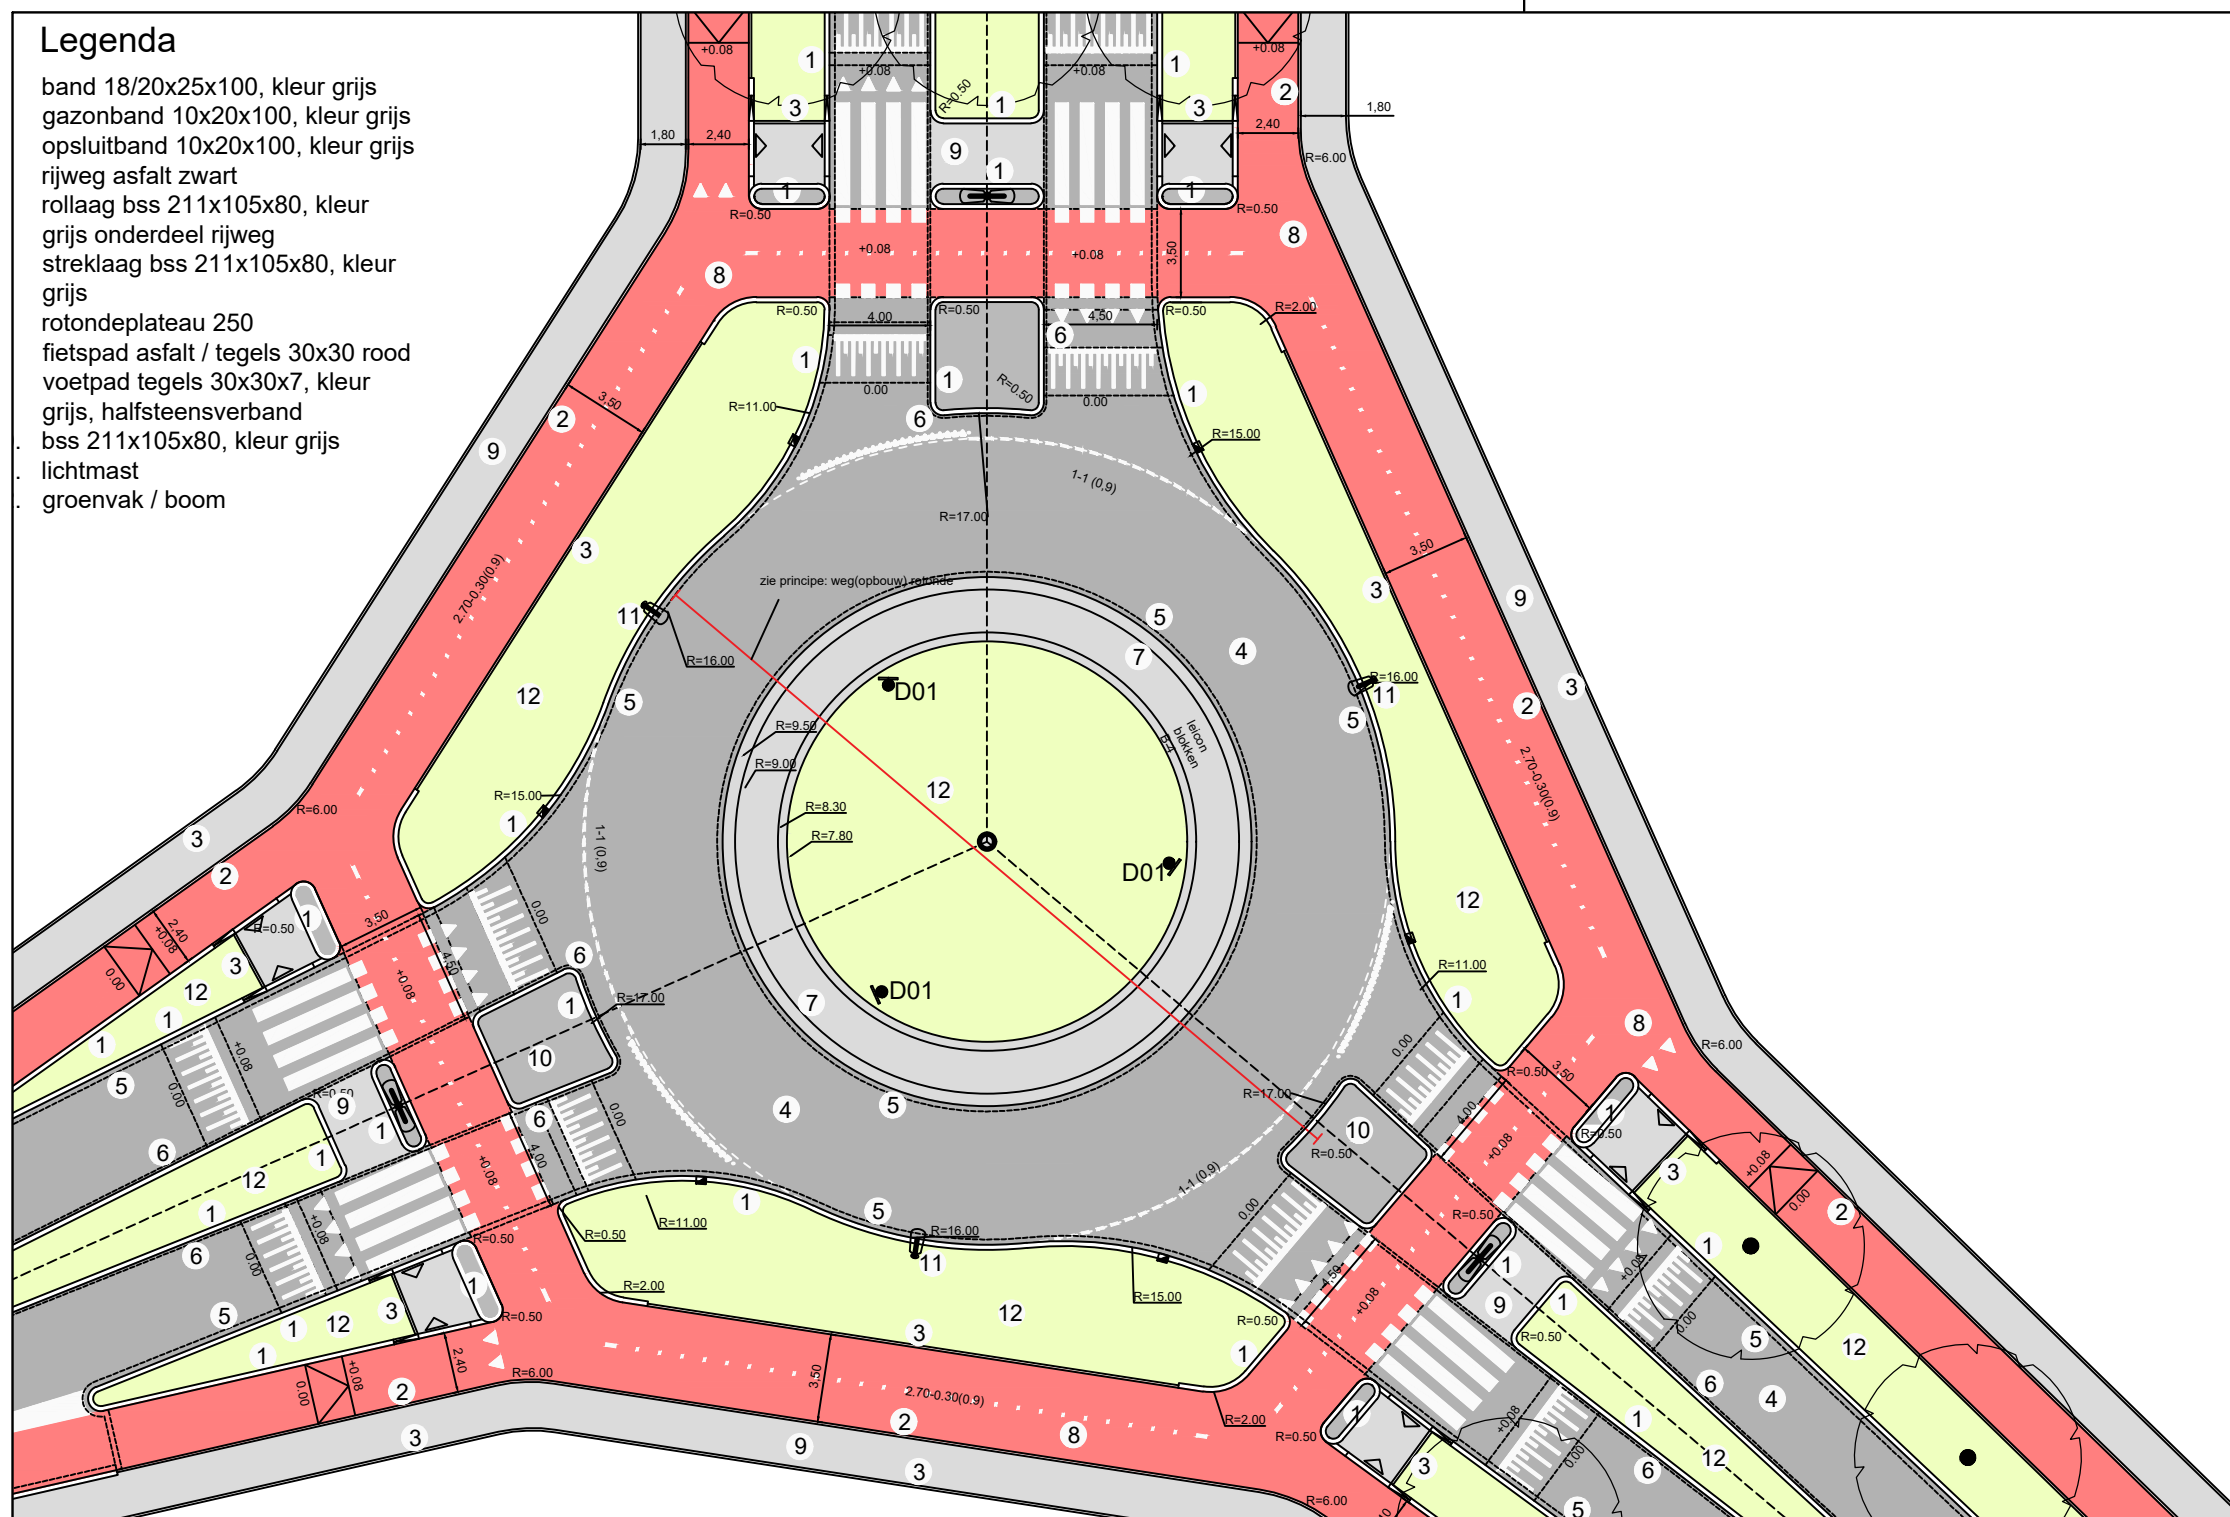


Principe: wegmarkering en
belijning aanrijdroute rotonde
Schaal 1:200

Rotonde:
Schaal 1:300

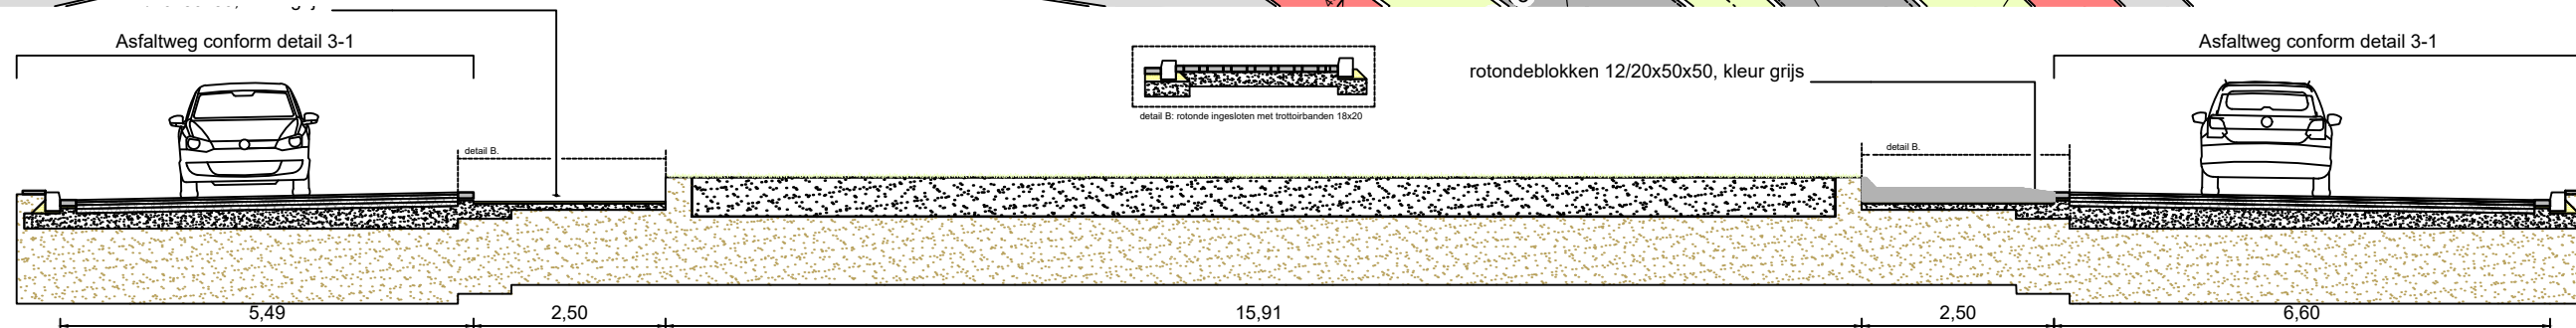

Principe: (weg)opbouw rotonde
Schaal 1:100

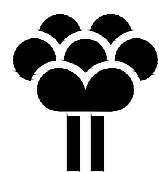


Gemeente
Zoetermeer

Rotonde en wegmarkering aanrijdroute

getekend: Gemeente Zoetermeer
gewijzigd:
datum: 3-4-2026

formaat: A3
schaal: 1:300/1:200/1:100
volgnummer: 3-10


Stadsbeheer 2026

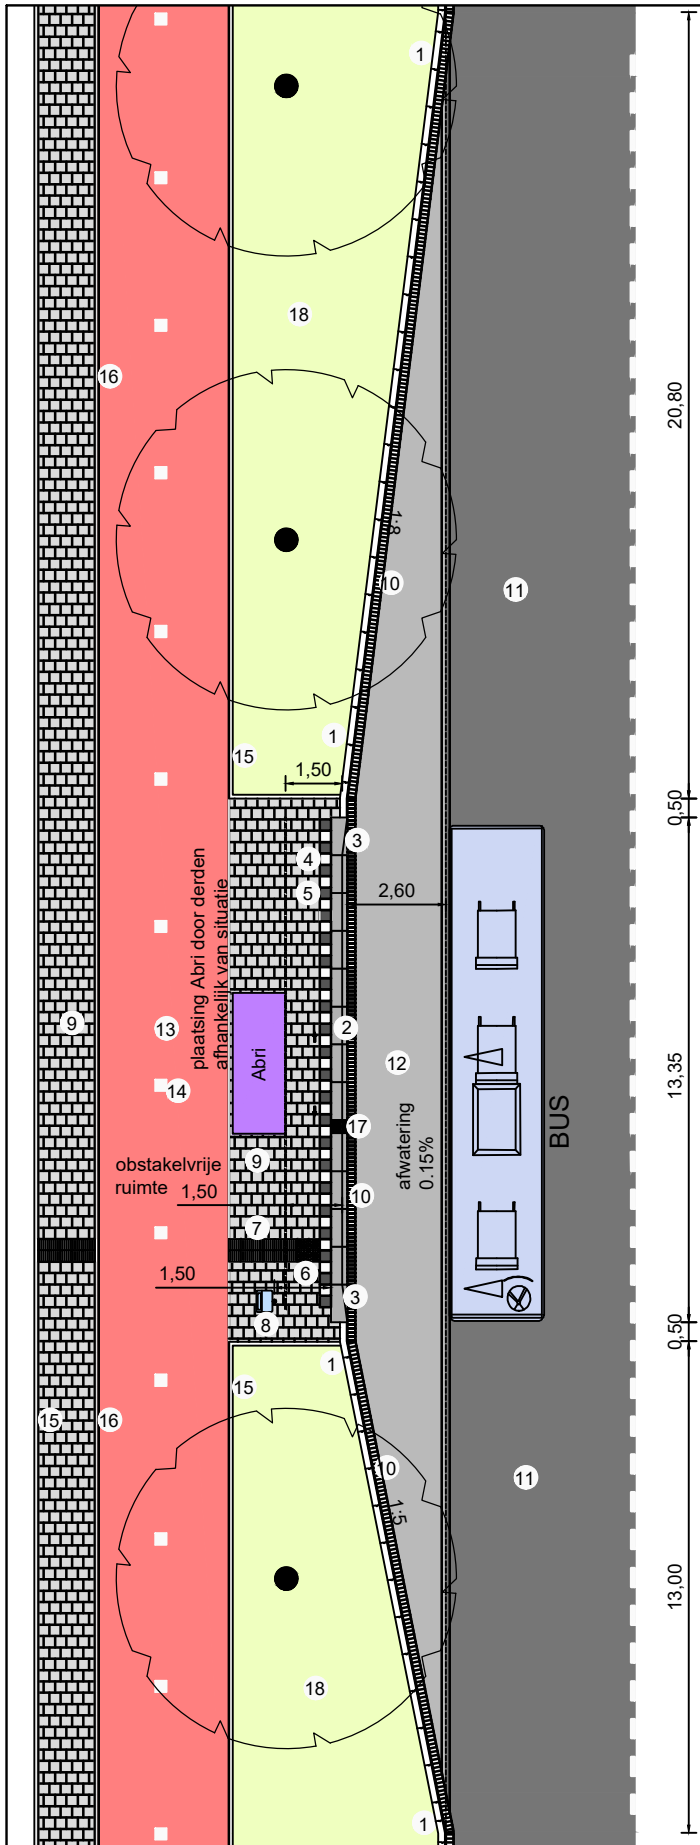


Legenda

1. band 18/20x25x100, kleur grijs.
2. leicon profil perronband 0.30/0.435x0.334x100.
3. leicon profil perronband overgangselement.
4. tegels 0.30x0.30x0.08, kleur wit.
5. tegels 0.30x0.30x0.08, kleur zwart
6. noppen tegels 0.30x0.30x0.08, kleur zwart.
7. geleidetegels 0.30x0.30x0.08, kleur grijs.
8. haltepaal met afvalbak.
9. tegel 0.30x0.30x0.08, kleur grijs halfsteensverband.
10. rollaag bss 211x105x80, kleur grijs onderdeel bushaven.
11. rijweg, asfalt.
12. bushaven, bss grijs- zwart/ asfalt zwart op betongranulaat
13. fietspad tegels 0.30x0.30, kleur rood/ asfalt rood.
14. fietspad as markering tegel 0.30x0.30, kleur wit.
15. opsluitband 10x20x100, kleur grijs.
16. gazonband 10x20x100, kleur grijs.
17. leicon busperron kolk 0.35x0.43x1.00m.
18. groen/ bomen.

Bushaven 13,35 meter / Leiconprofil perronbanden
Schaal 1:200

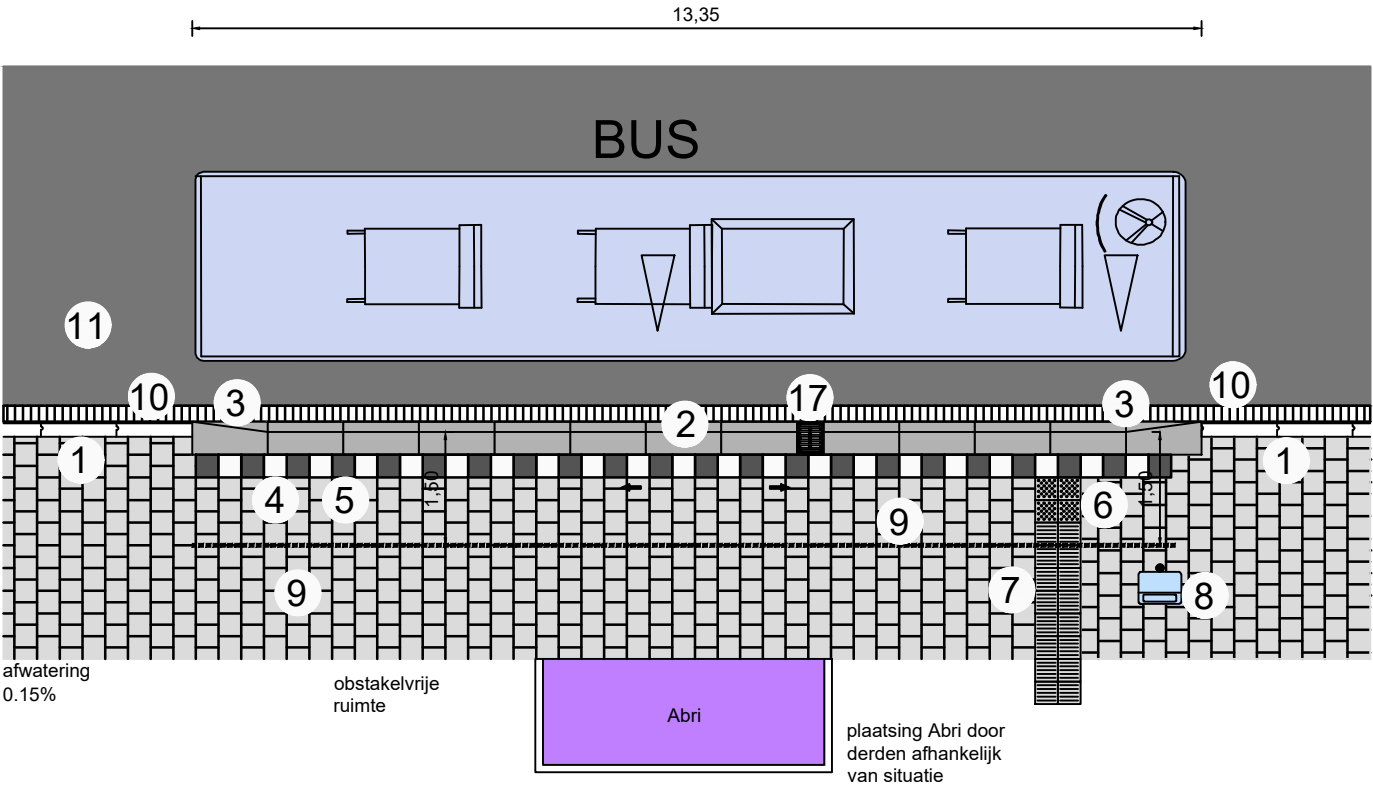

Bushalte 13,35 meter
Schaal 1:100


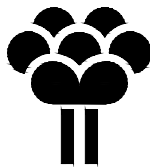


Gemeente
Zoetermeer
Bushaven


getekend: Gemeente Zoetermeer
gewijzigd: 3-4-2026
datum:

formaat: A3
schaal: 1:200/1:100
volgnummer: 3-11


Stadsbeheer 2026

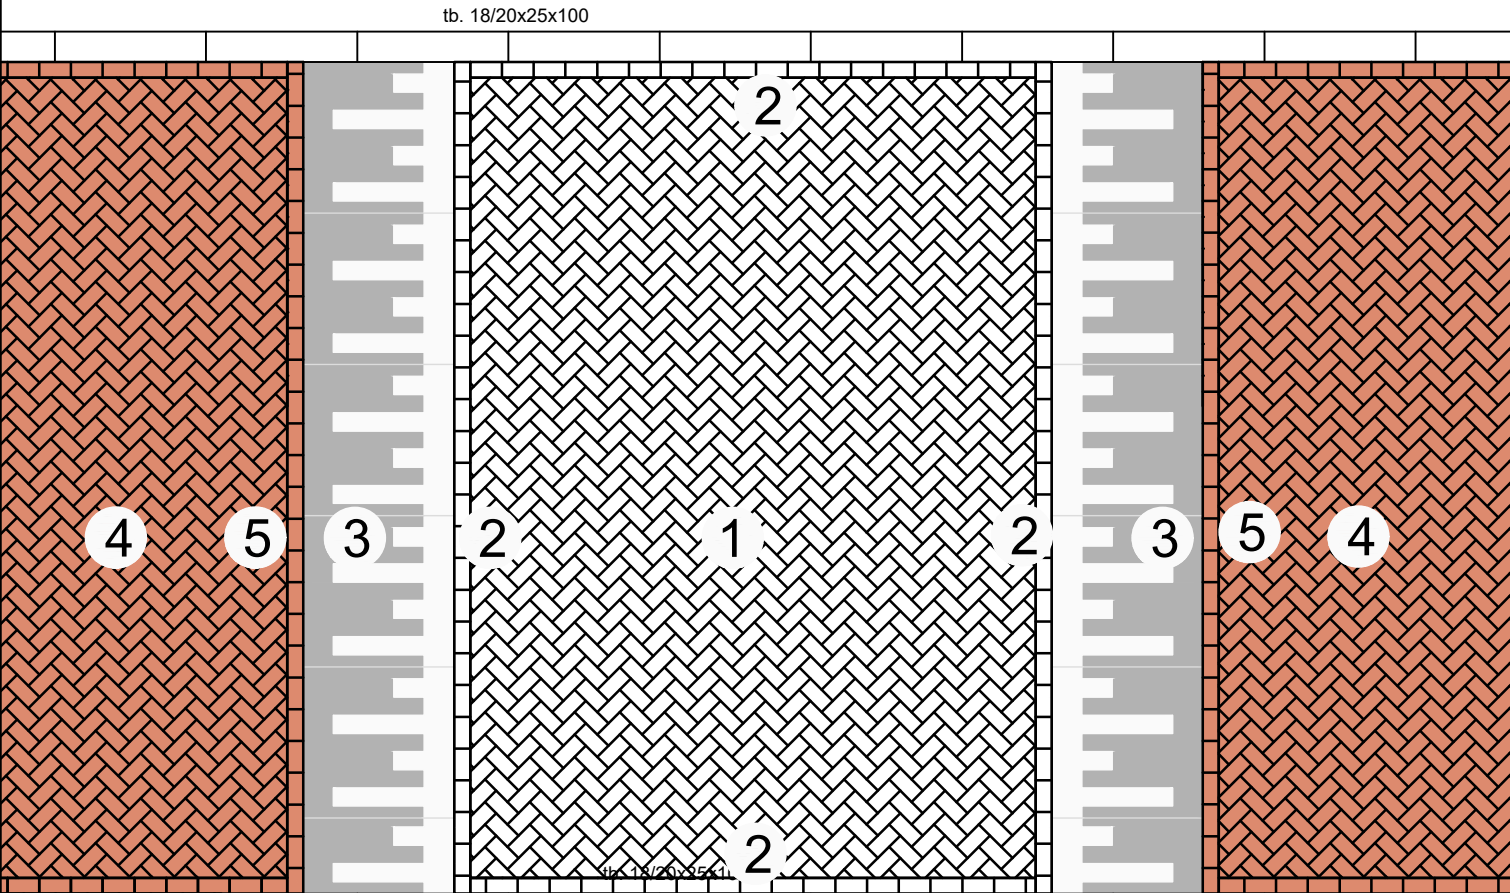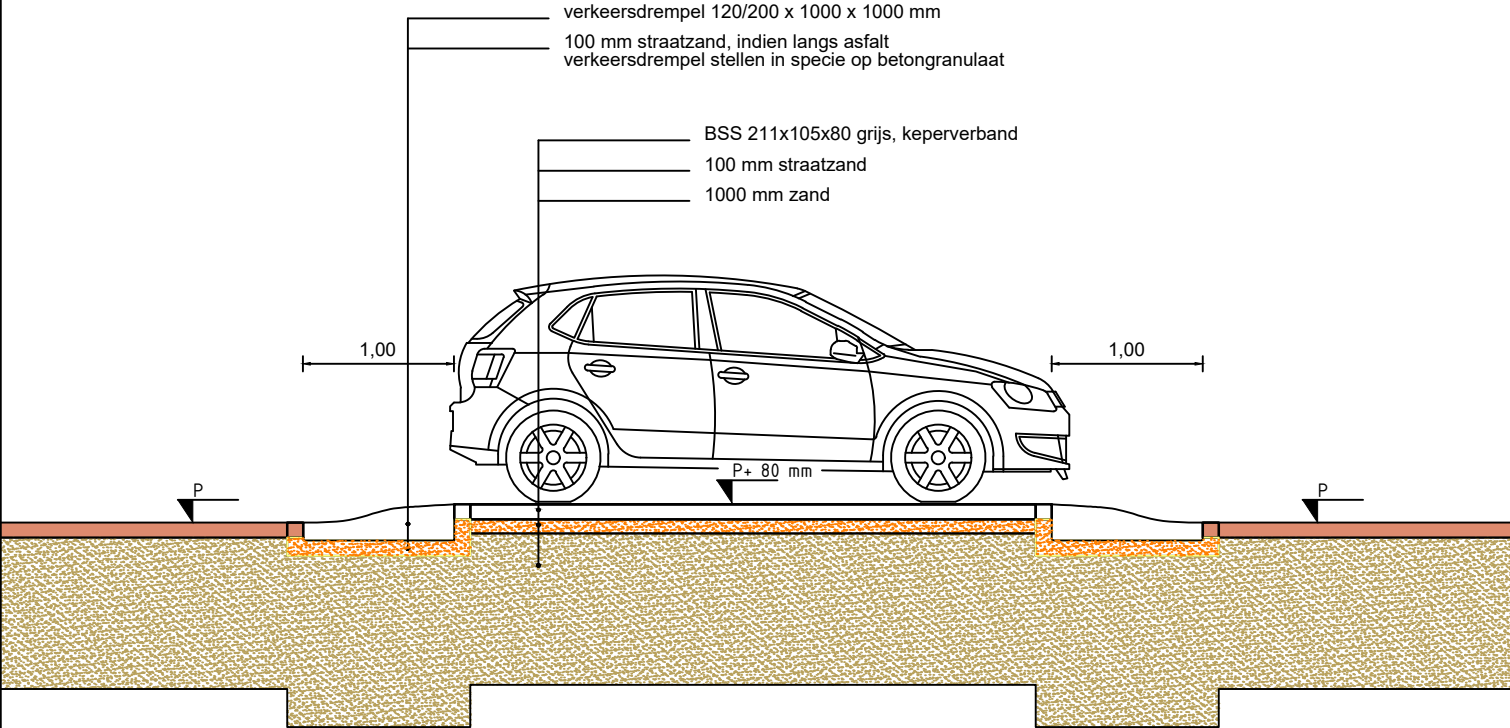

1. plateau bss grijs keperverband.
2. plateau bss grijs streklaag.
3. plateau drempel beton (hxbxl) 120/200x500/1000x1000 (afhankelijk van snelheid) sinus 8cm Lavarø zwart met standaard taludmarkering wit.
4. rijweg bss Mobo bruin/ zwart genuanceerd keperverband.
5. bss Mobo bruin/ zwart streklaag.

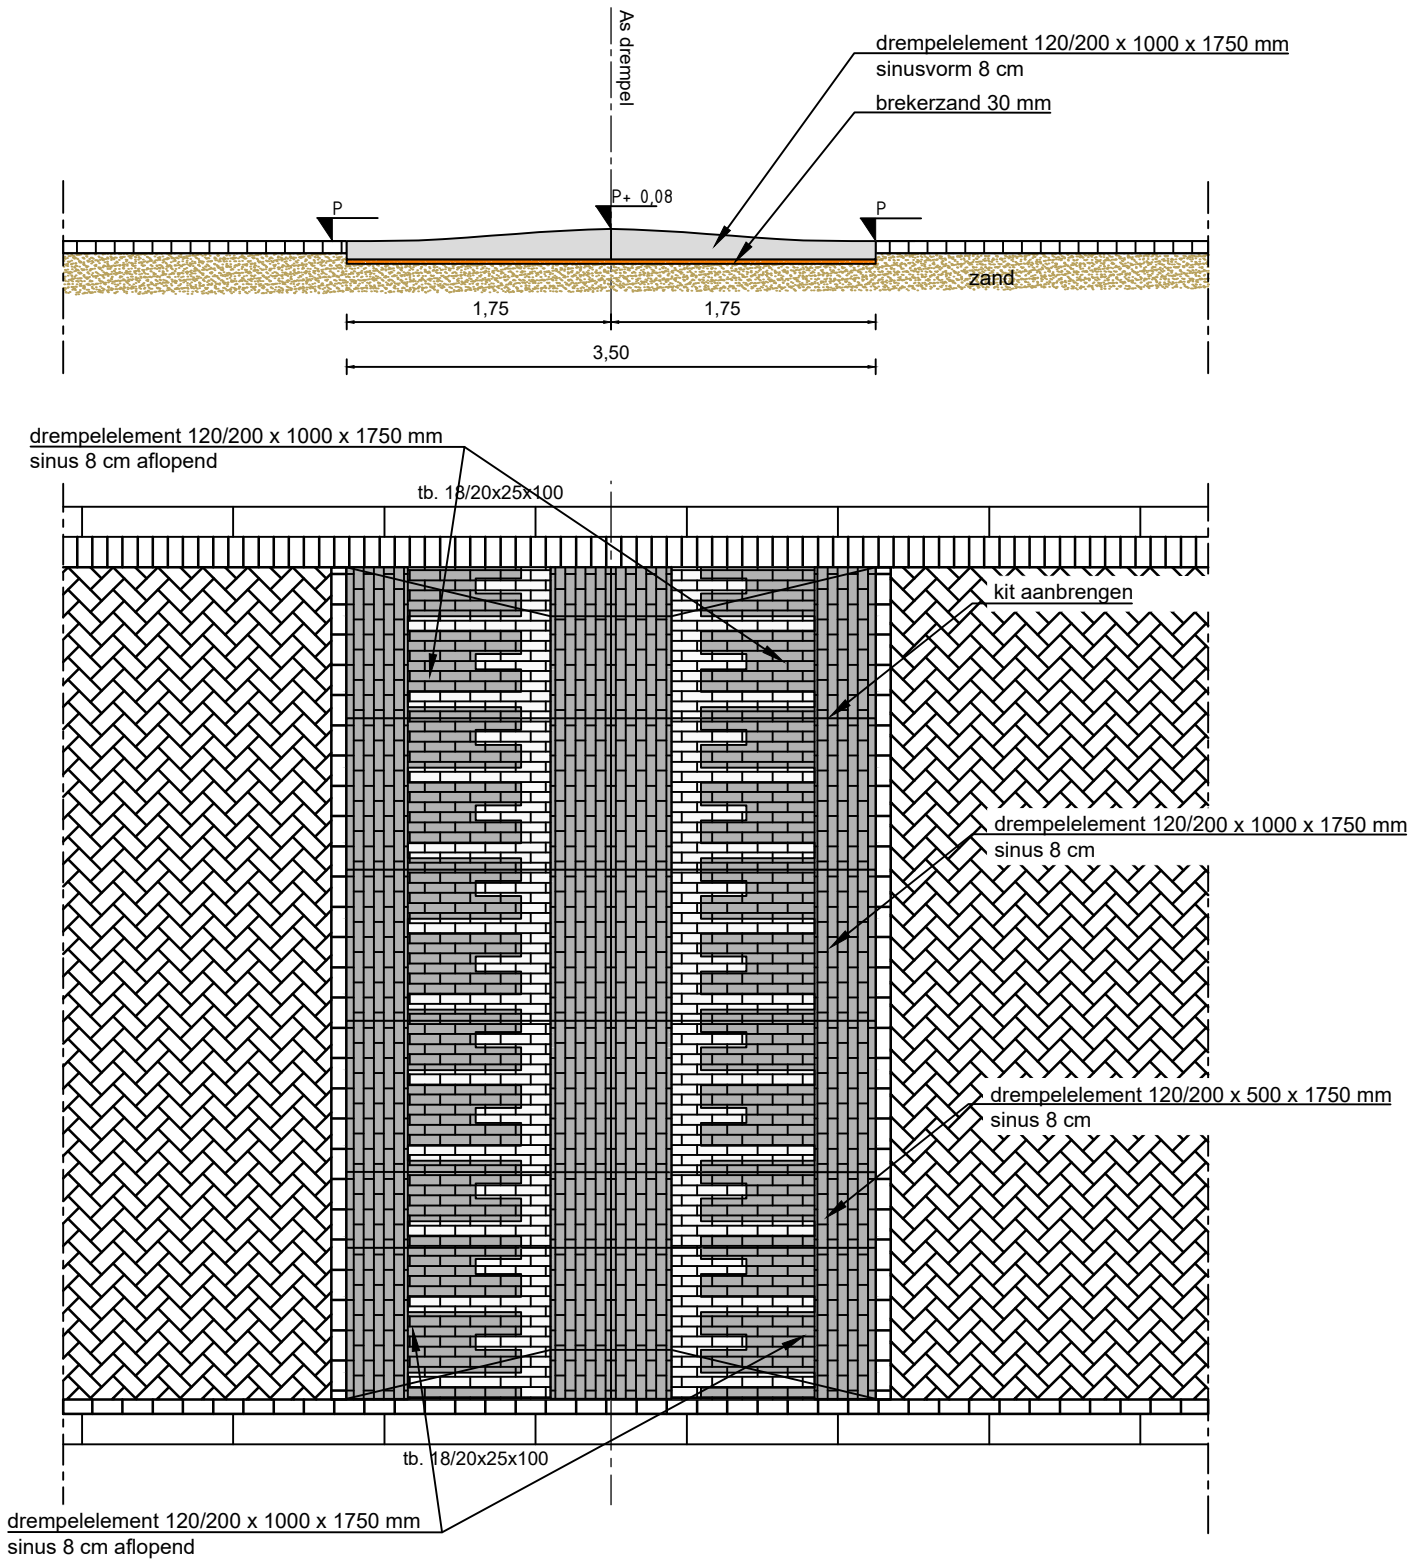

* drempelementen met steenmotief


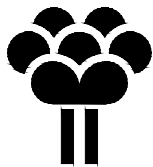


Gemeente
Zoetermeer



Plateau verkeersdrempel 30 km/u - betondrempel 30 km/u

getekend: Gemeente Zoetermeer
gewijzigd: 3-4-2026
datum: formaat: A3
schaal: 1:50
volgnummer: 3-12


Stadsbeheer 2026

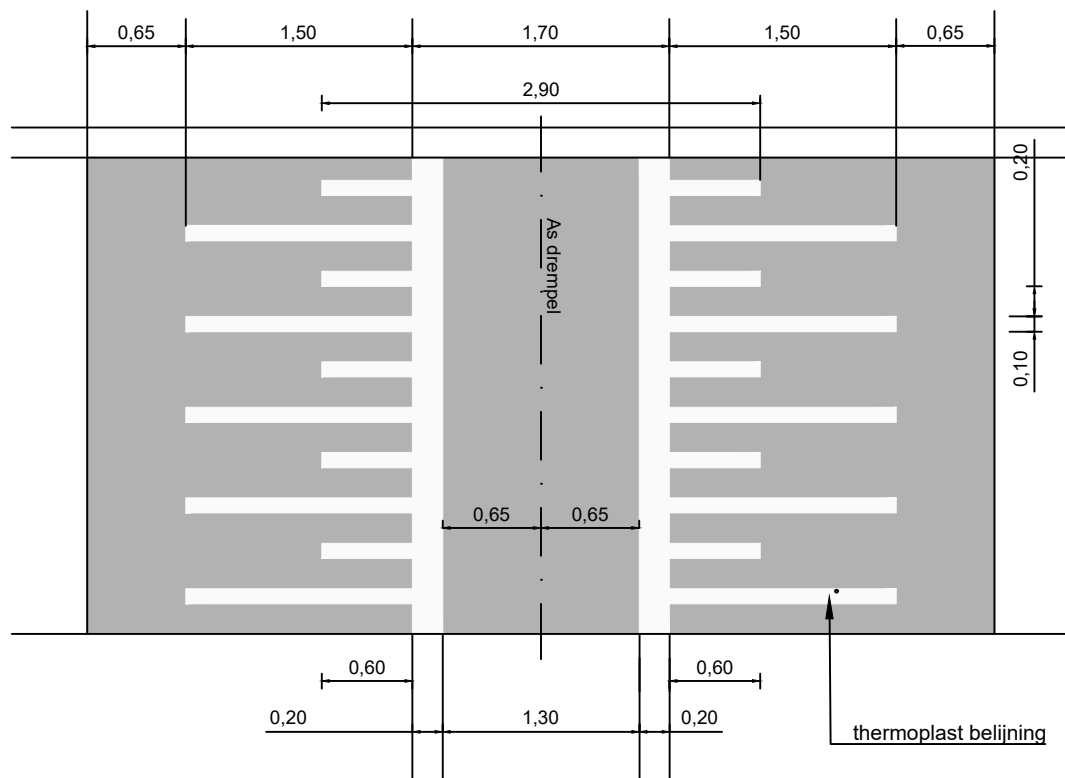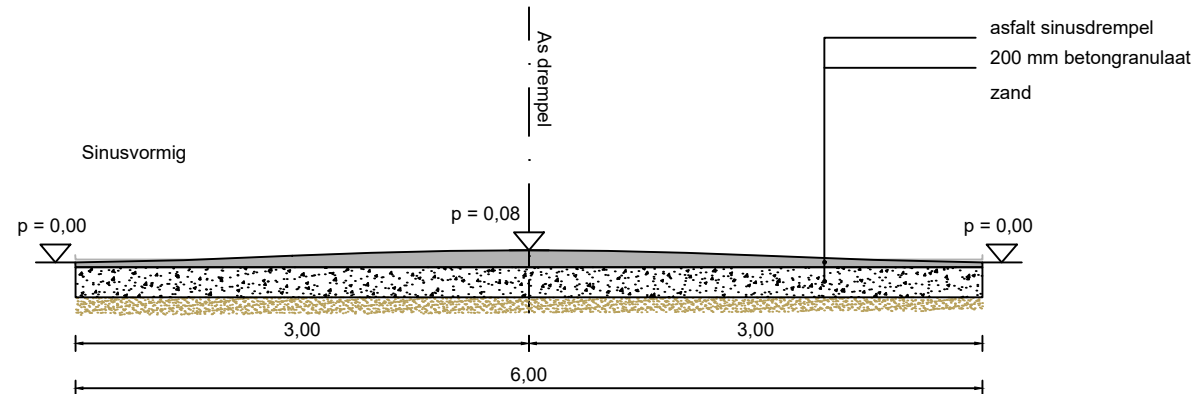

3-13-1 Asfalt sinusdrempel 50 km/u
Schaal 1:50

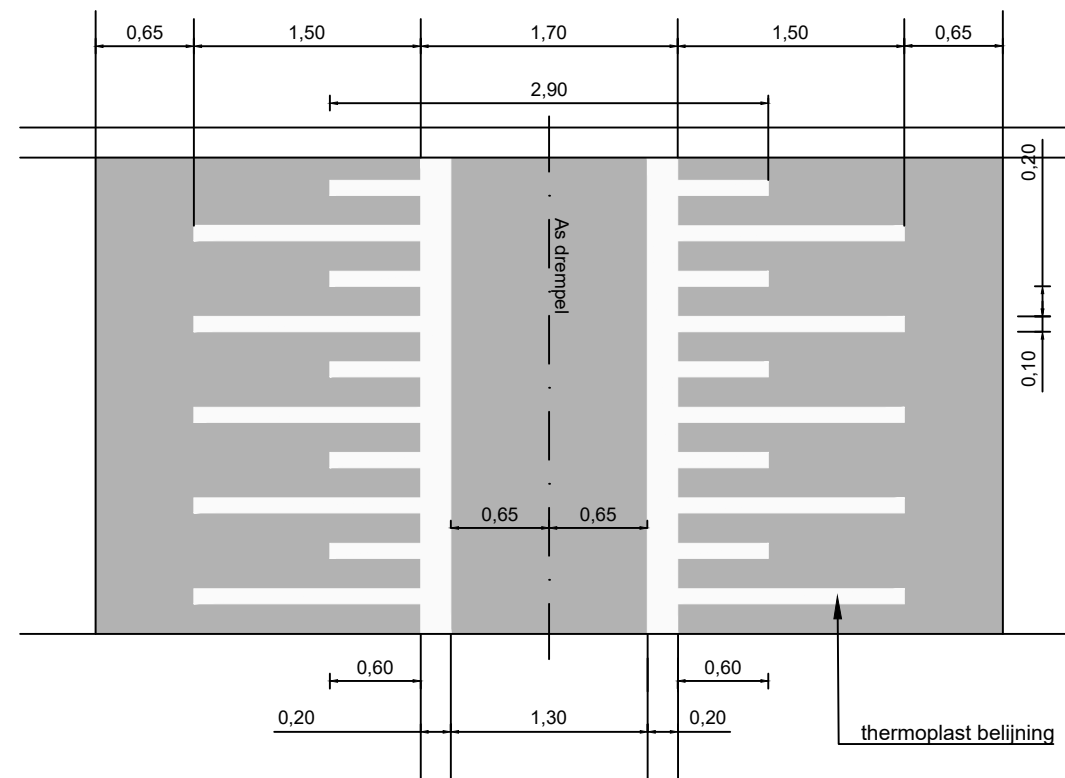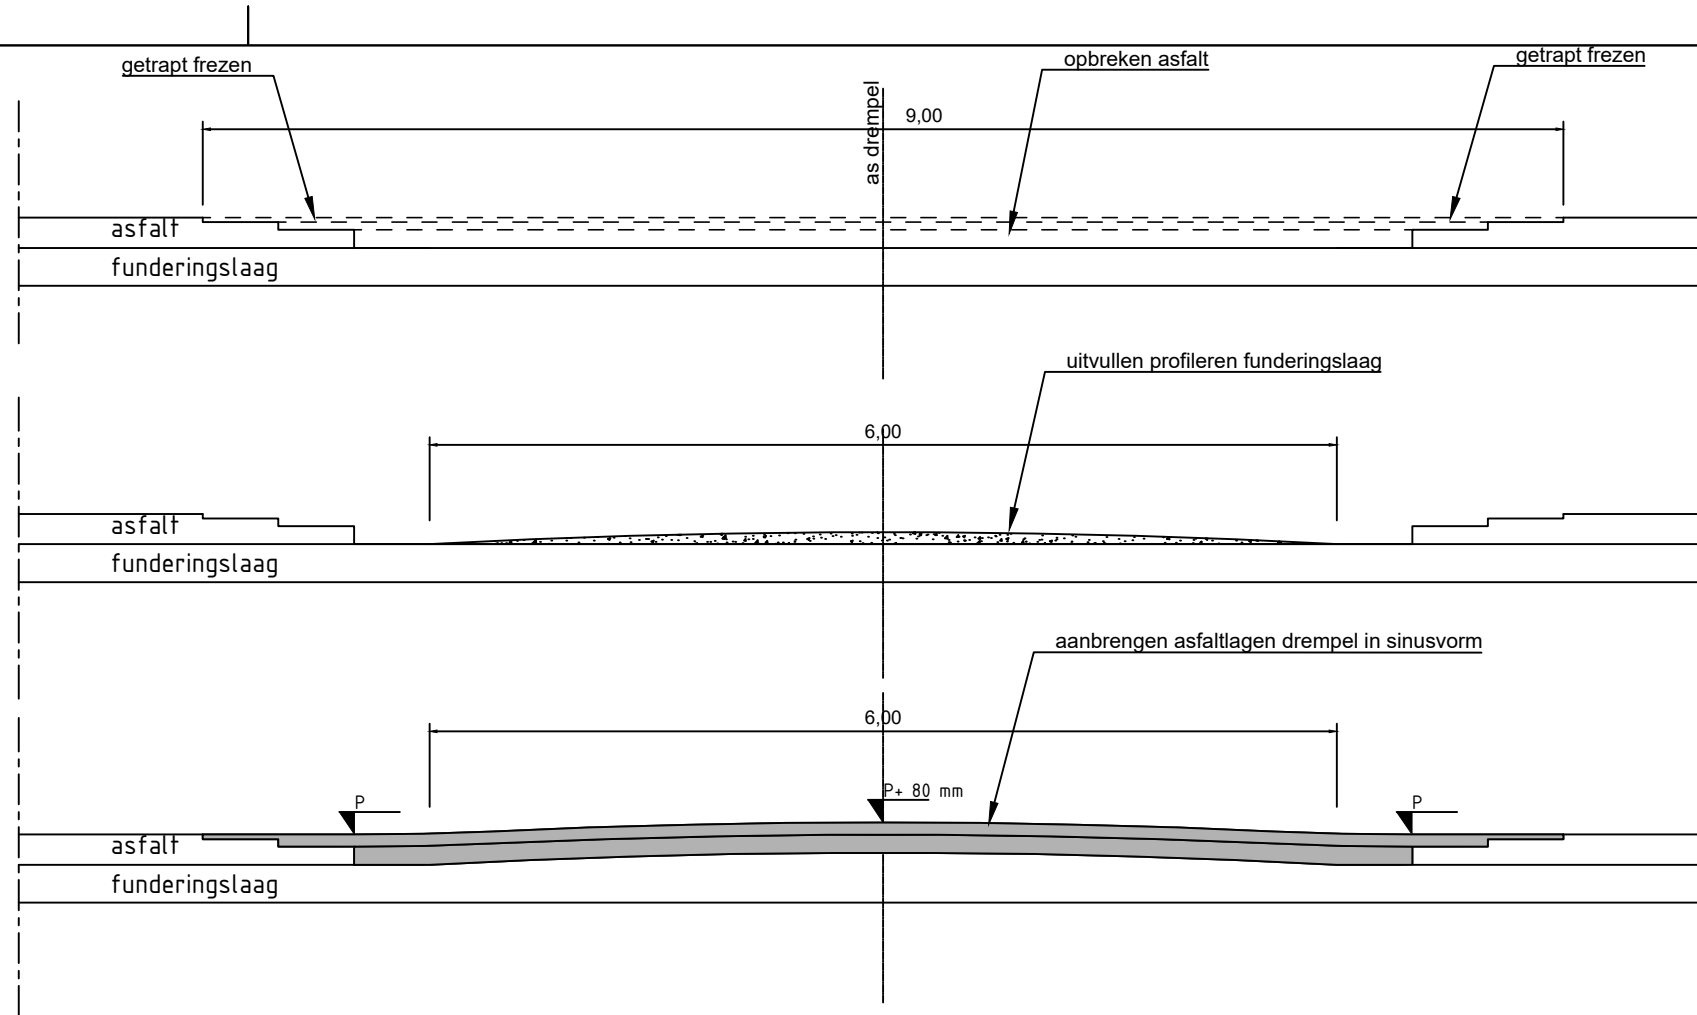

3-13-2 Asfalt sinusdrempel 50 km/u in bestaand asfalt
Schaal 1:50

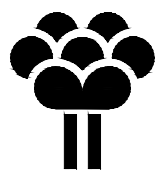


Gemeente
Zoetermeer

Asfalt sinusdrempel 50 km/u - Asfaltdrempel 50 km/u in bestaand asfalt

getekend: Gemeente Zoetermeer
gewijzigd:
datum: 3-4-2026


formaat: A3
schaal: 1:50
volgnummer: 3-13

Stadsbeheer 2026

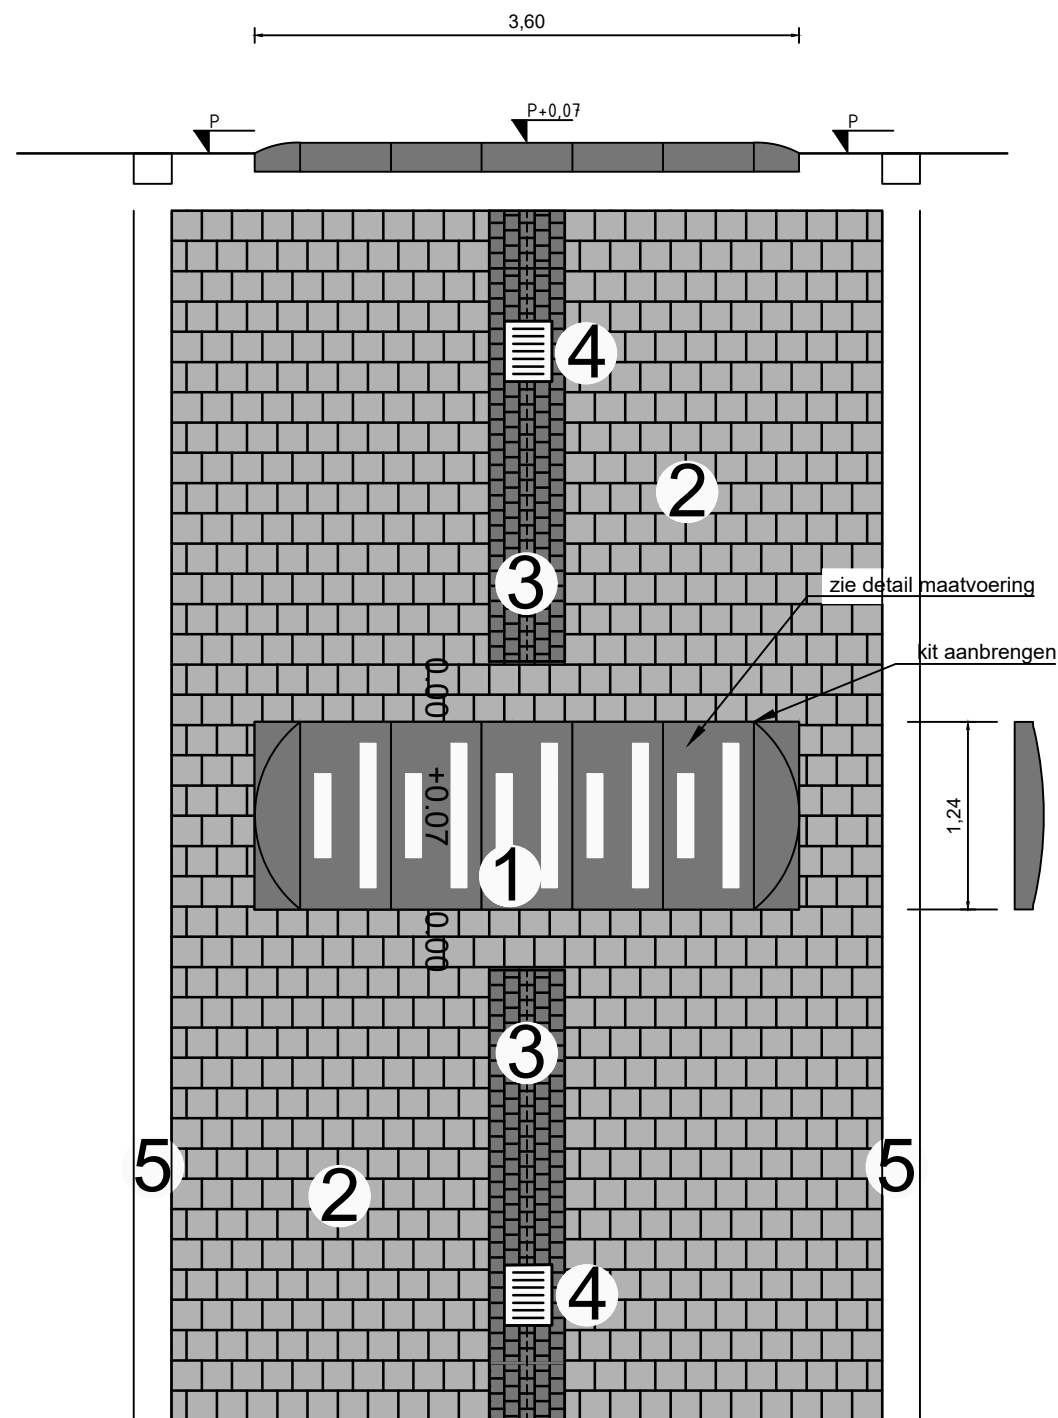


Principe detail: kussendrempel beton schaal 1:50

1. verkeersdrempel beton 124x60/30x12/19 (sinus 7cm) antraciet zwart.
2. tegels 20x20x8, kleur Oosterheem donker halfsteensverband.
3. molgoot cobblestone 10x10x8, kleur zwart halfsteensverband.
4. straatkolk
5. band 25x20x100 recht, kleur Oosterheem donker.

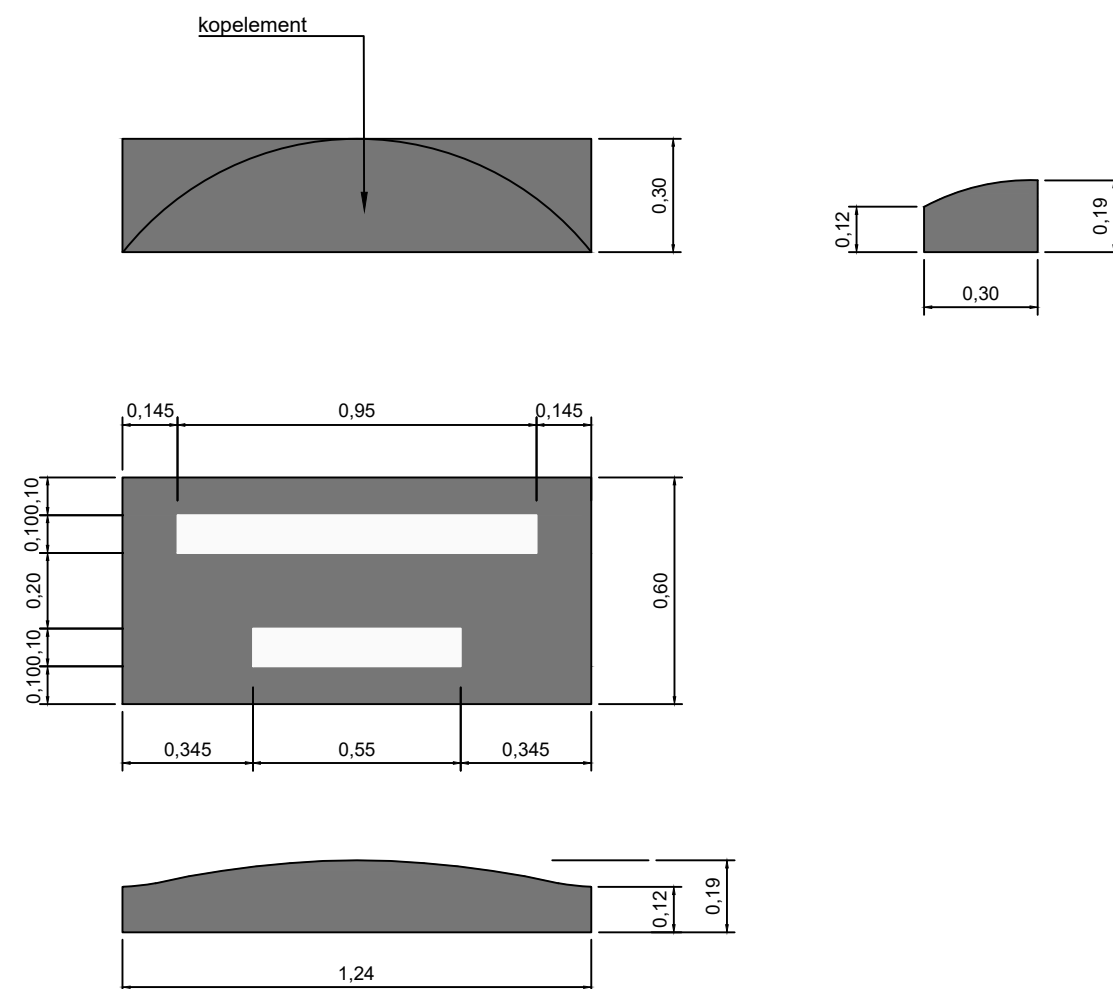

Detail maatvoering:
verkeersdrempel beton woonerf (lxbxh)
124x60/30x12/19,
sinus 7 (15-30km/u)
Type: Gicon Combi, fabriikaat Giverbo
schaal 1 : 20

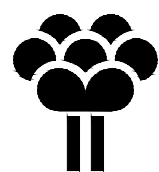


Gemeente
Zoetermeer

Principedetail kussendrempel beton op woonerf

getekend: Gemeente Zoetermeer
gewijzigd: 3-4-2026
datum:



formaat: A3
schaal: 1:50
volgnummer: 3-15

Stadsbeheer 2026

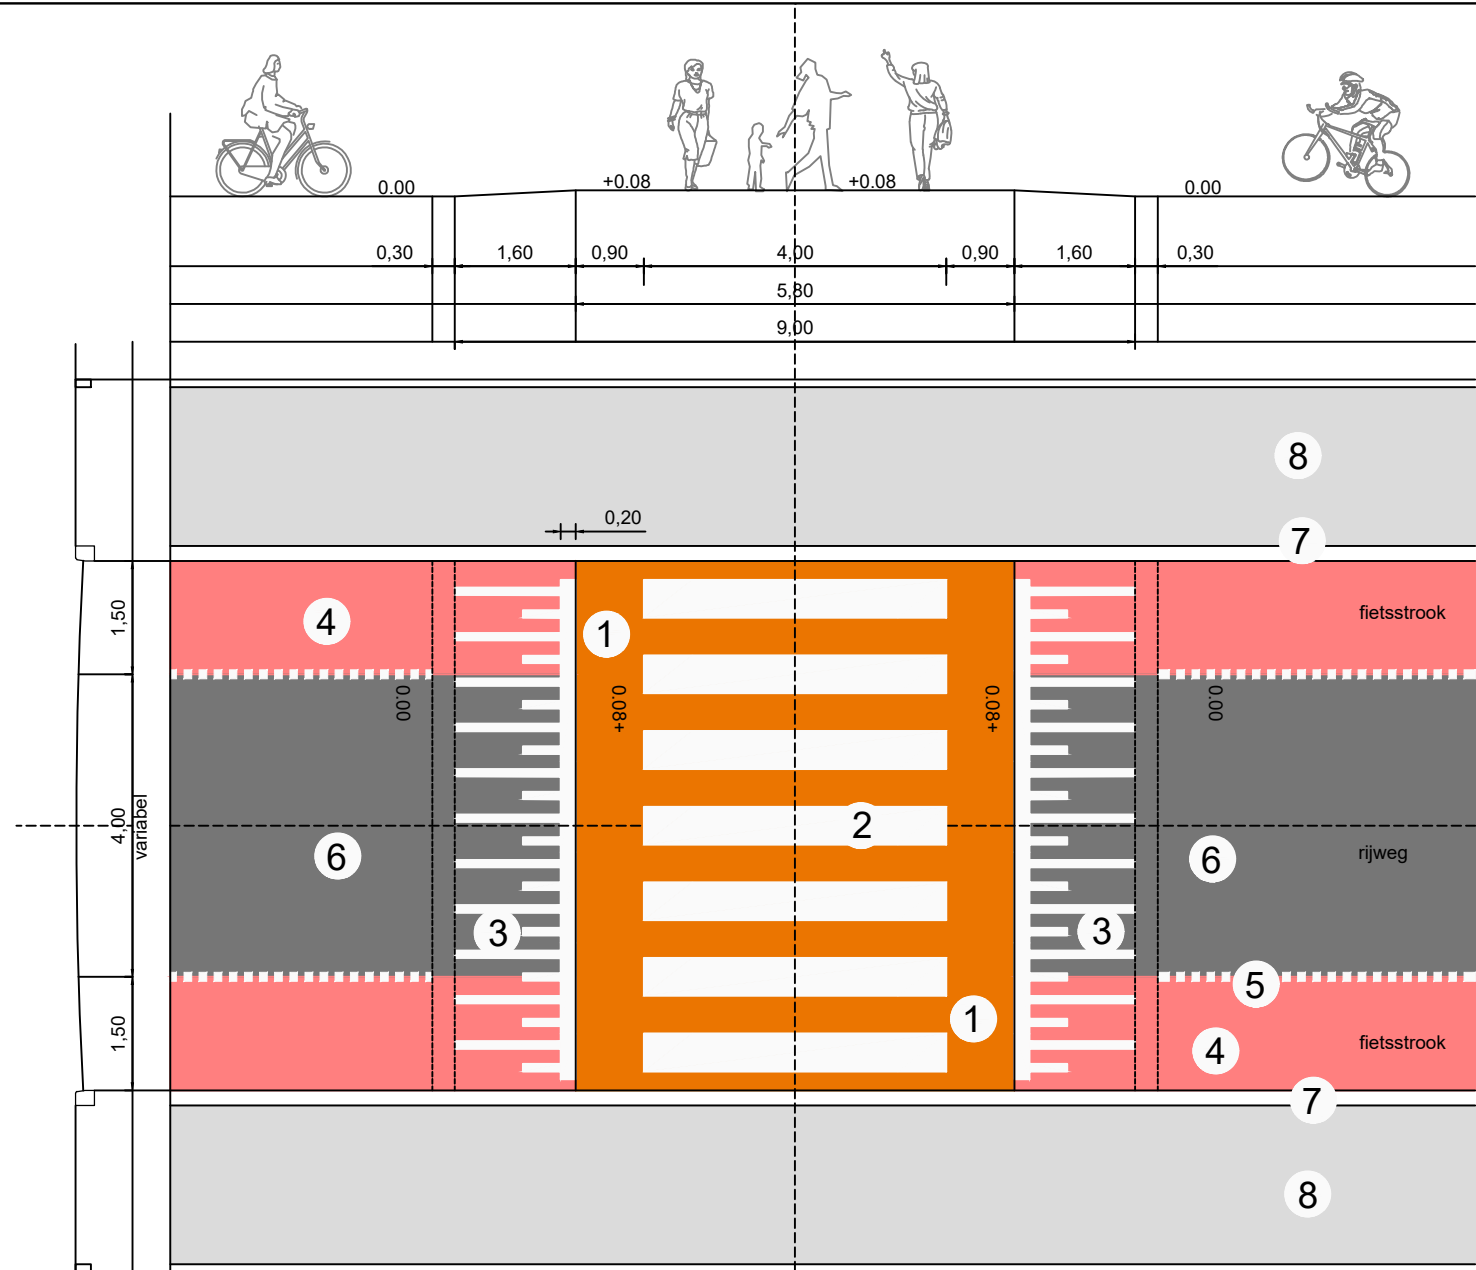

Legenda


- 1. premark, ondergrond, kleur oranje RAL 2009.
- 2. zebra kleur wit.
- 3. taludmarkering, kleur wit.
- 4. fietsstrook, asfalt rood.
- 5. witte belijning 1.00 - 1.00 (0.10).
- 6. rijweg, asfalt.
- 7. trottoirband 18/20x25x100.
- 8. voetpad tegels 0.30x0.30.
- 9. doorgetrokken streep, kleur wit.
- 10. tekst schoolzone, kleur wit in hoofdletter, teksthogte 1.00m.

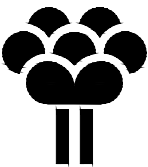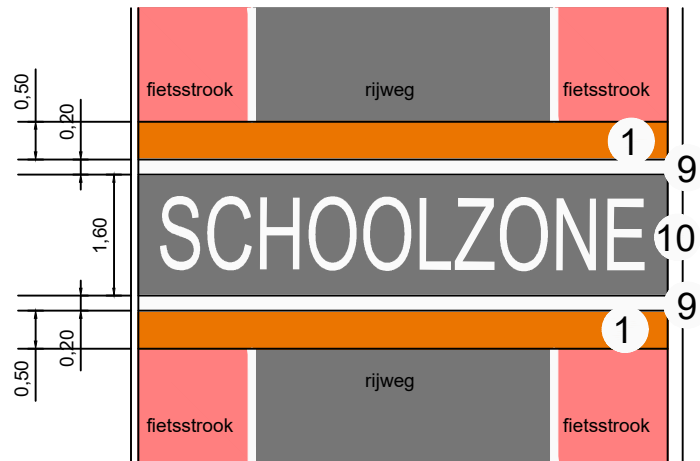


Gemeente
Zoetermeer
Maatregelen bij schoolzone

getekend: Gemeente Zoetermeer
gewijzigd: 3-4-2026
datum: formaat: A3
schaal: 1:100
volnummer: 3-16

Stadsbeheer 2026

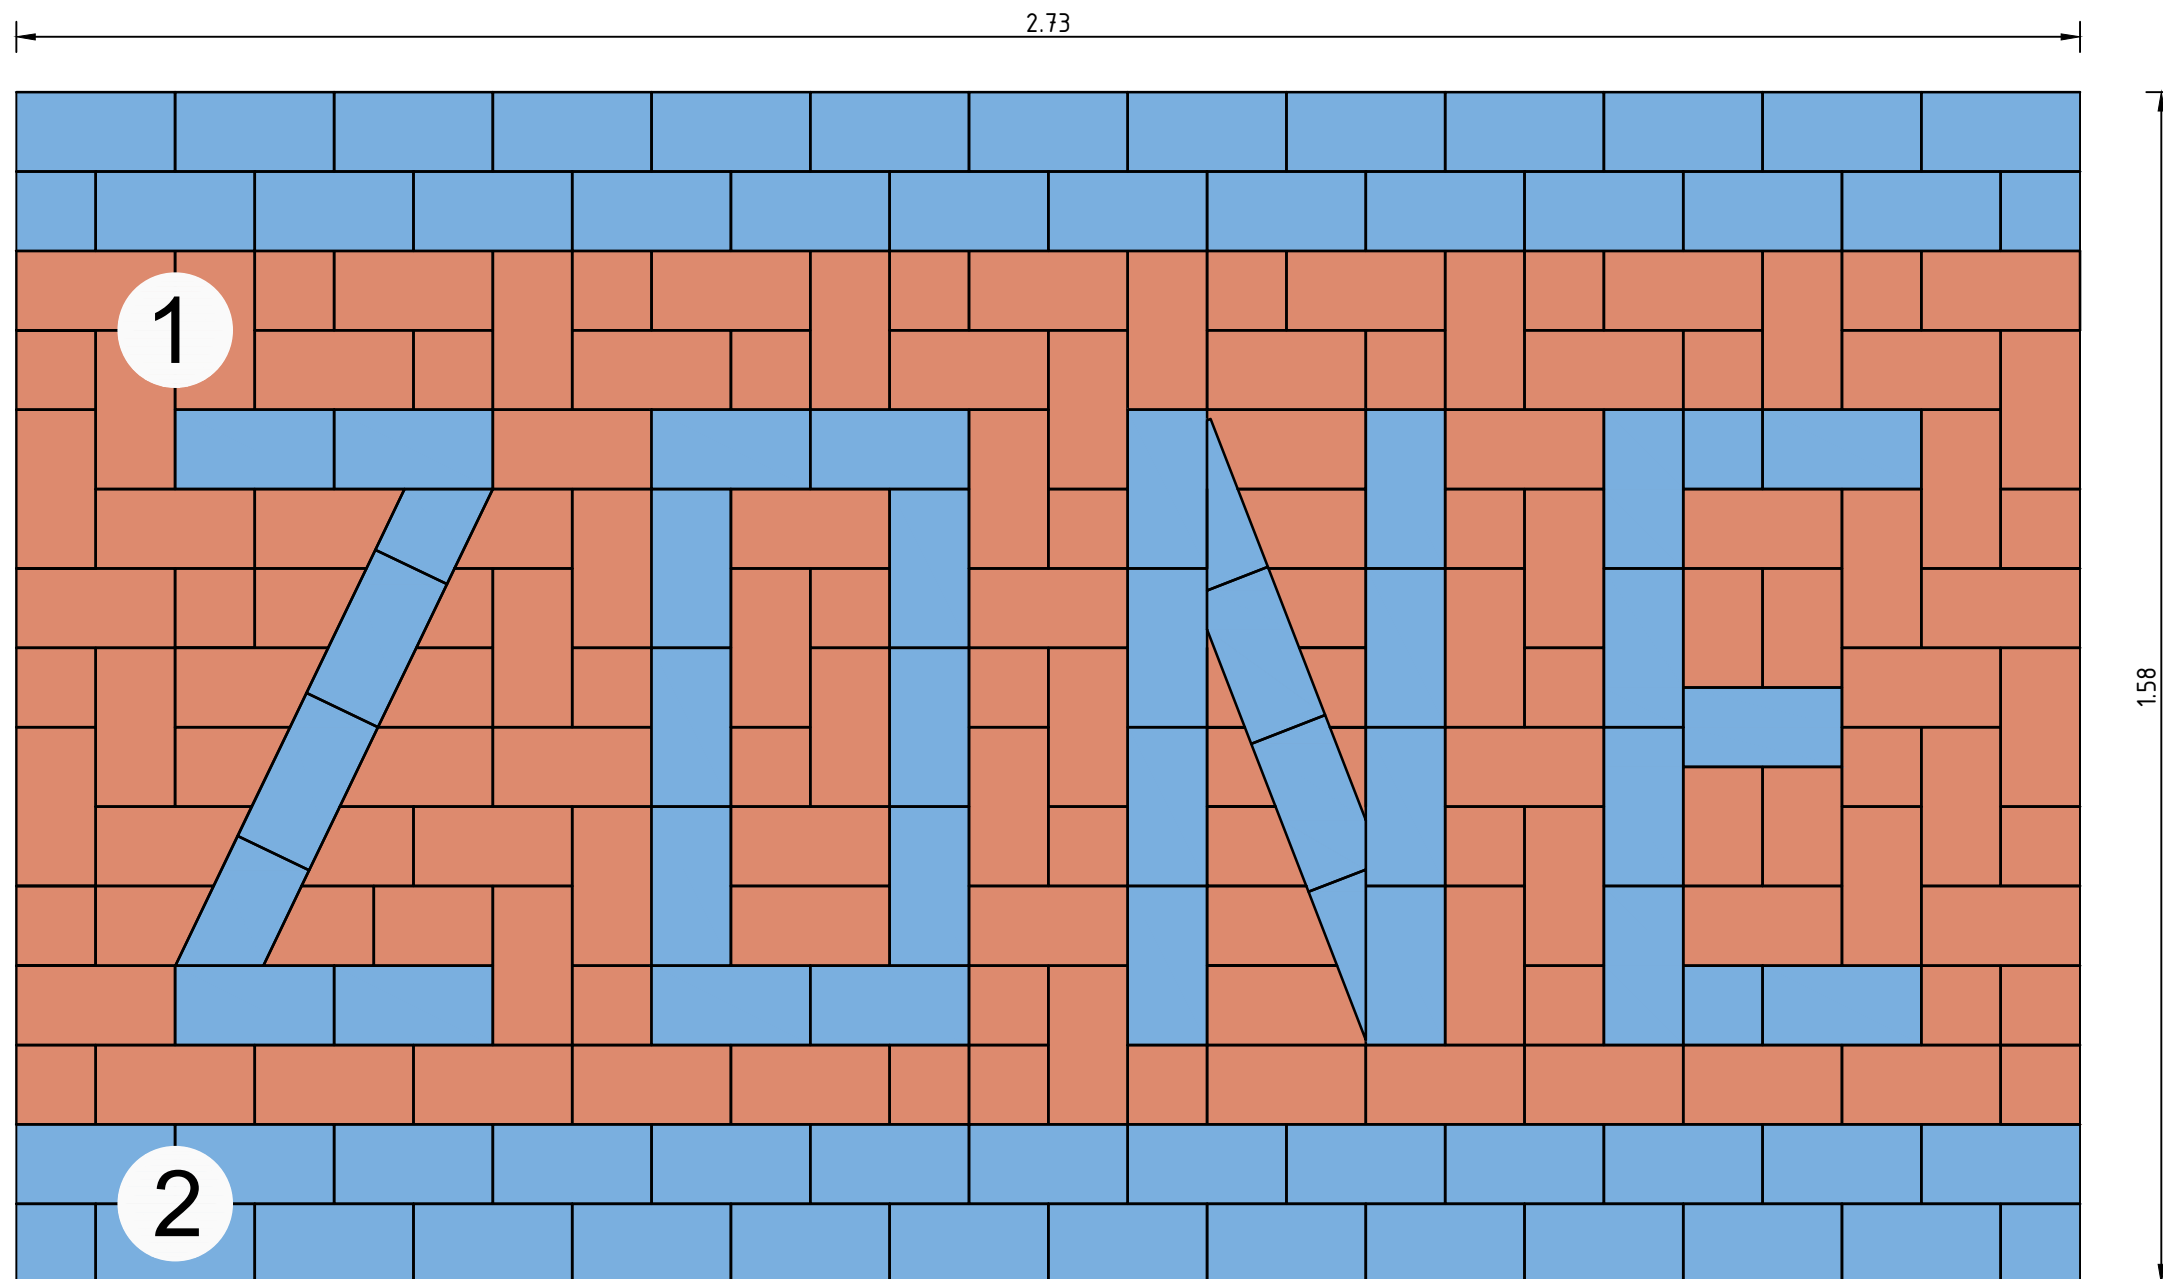

1. markering parkeerzone bss 211x105x80, kleur blauw
2. bss 211x105x80, kleur mobo bruin

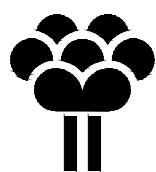


Gemeente
Zoetermeer
Blauwe zone

getekend: Gemeente Zoetermeer
gewijzigd:
datum: 3-4-2026


formaat: A3
schaal: 1:10
volnummer: 3-17

Stadsbeheer 2026

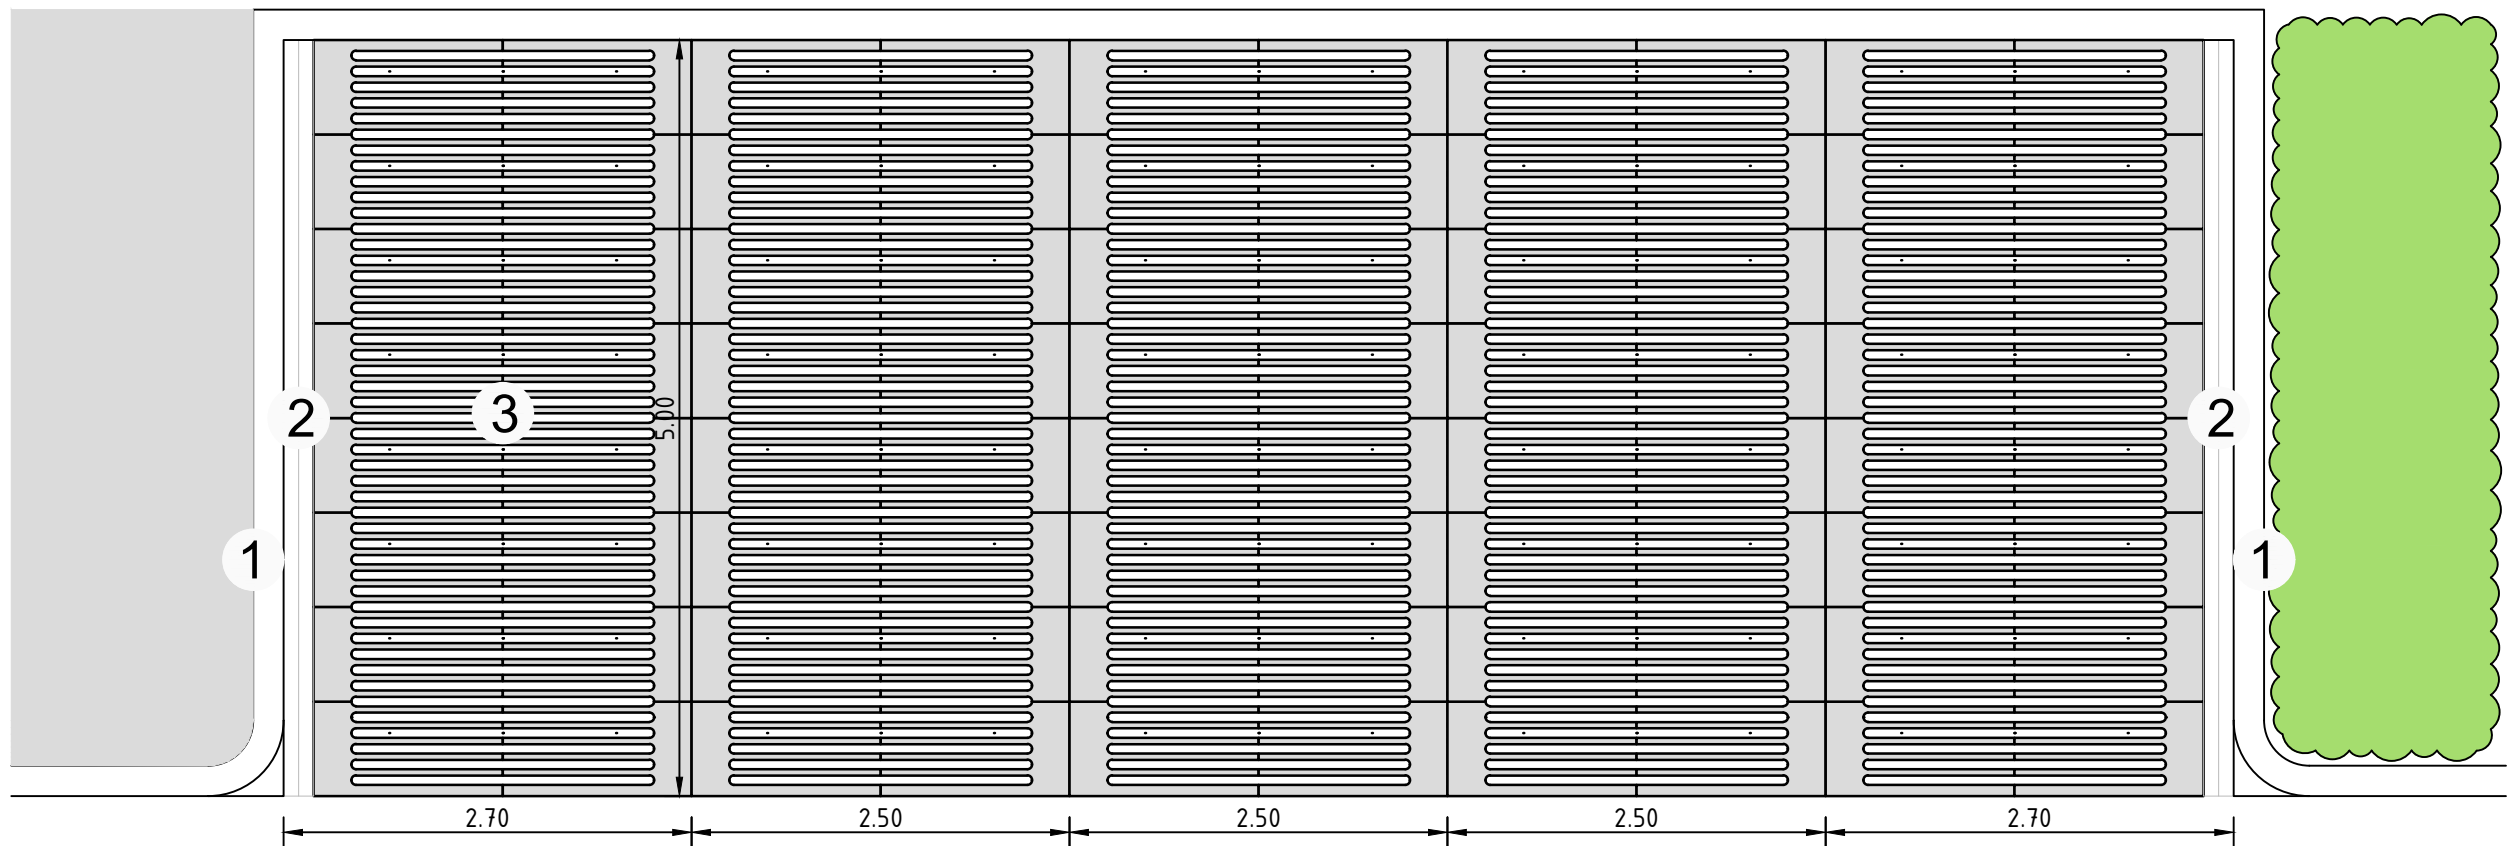

Principe detail: haaksparkeren grasbetontegels 1:50

1. trottoirband 18/20x25x100, kleur grijs
2. streklaag bss 211x105x80, kleur grijs (parkeren 2,70 breed)
3. solidgreen grasbetontegels

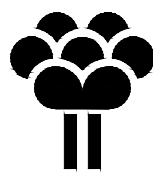

Gemeente
Zoetermeer


Haaksparkeren grasbetontegels

getekend: Gemeente Zoetermeer
gewijzigd:
datum: 3-4-2026


formaat: A3
schaal: 1:10
volgnummer: 3-18

Stadsbeheer 2026


Boomkronen snoeien/snoeimaatregelen treffen om te zorgen dat boomkronen niet tegen de gevels groeien. Minimaal 3.00 meter, soortspecifieke eigenschappen doorslaggevend.

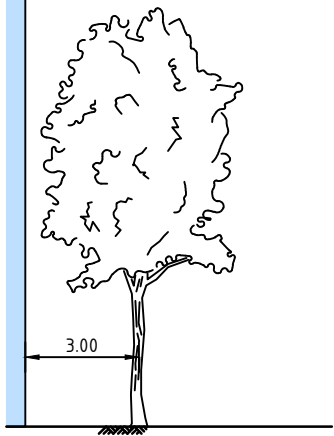


Afstand 1e grootte boom tot gevel
Schaal 1:200

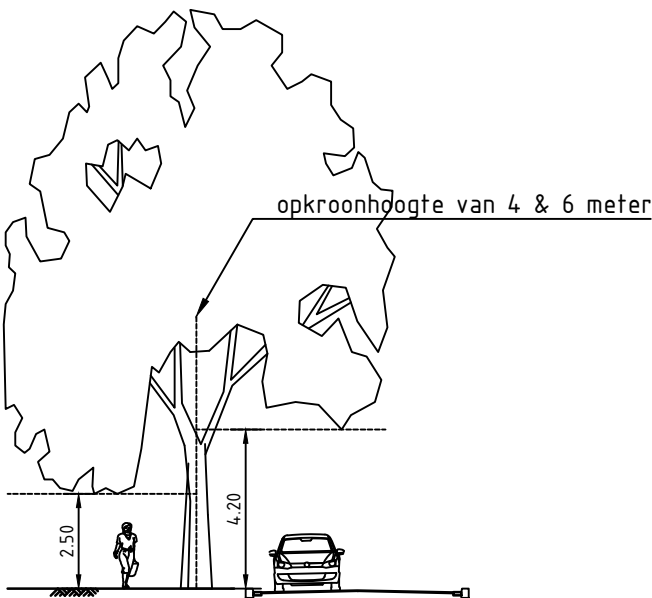


Profiel van vrije ruimte bij autoweg
Schaal 1:200

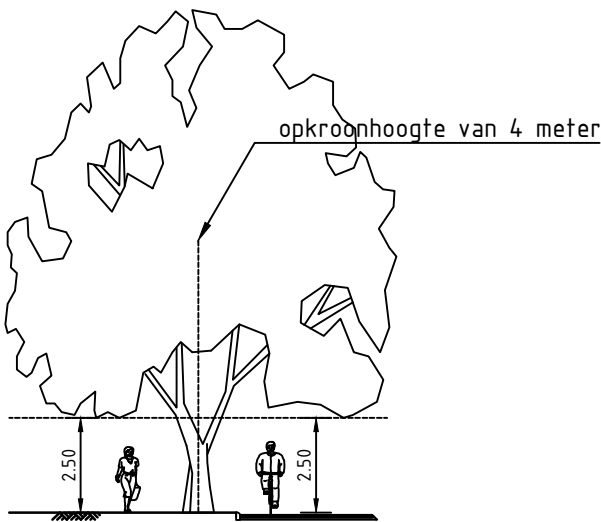



Profiel van vrije ruimte bij fietspad, trottoir en parkeervak
Schaal 1:200

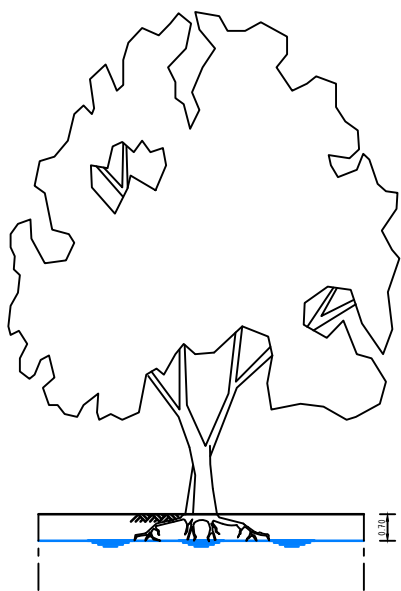

Wortelkluitontwikkeling bij grondwaterprofiel
Schaal 1:200

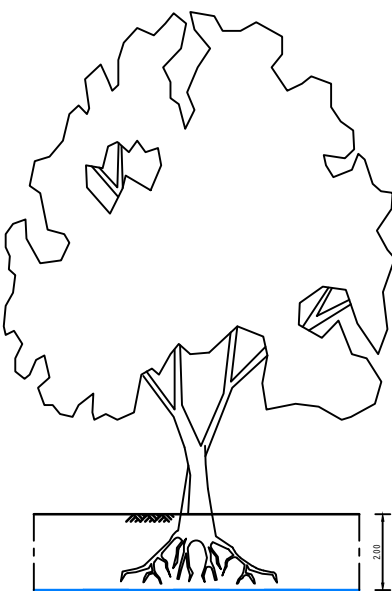


Wortelkluitontwikkeling bij hangwaterprofiel
Schaal 1:200

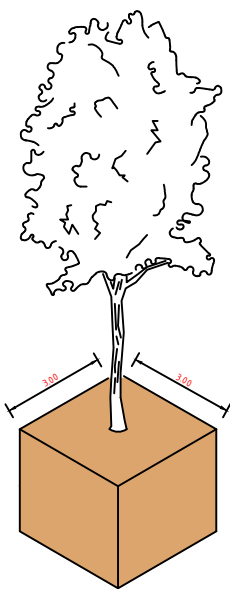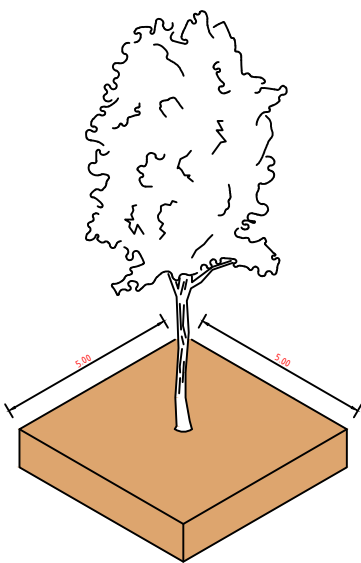

Zelfde m3 doorwortelbaar volume, verschillende vormen
Schaal 1:200

Afmetingen doorwortelbaar volume afhankelijk van beschikbare ruimte, hoogte grondwater en storende lagen

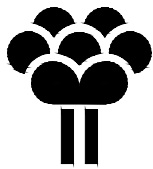






Gemeente
Zoetermeer

Bomendetails algemeen - afstanden en afmetingen


getekend: Gemeente Zoetermeer
gewijzigd: 3-4-2026
datum:

formaat: A3
schaal: 1:100
volgnummer: 4-1

Stadsbeheer 2026

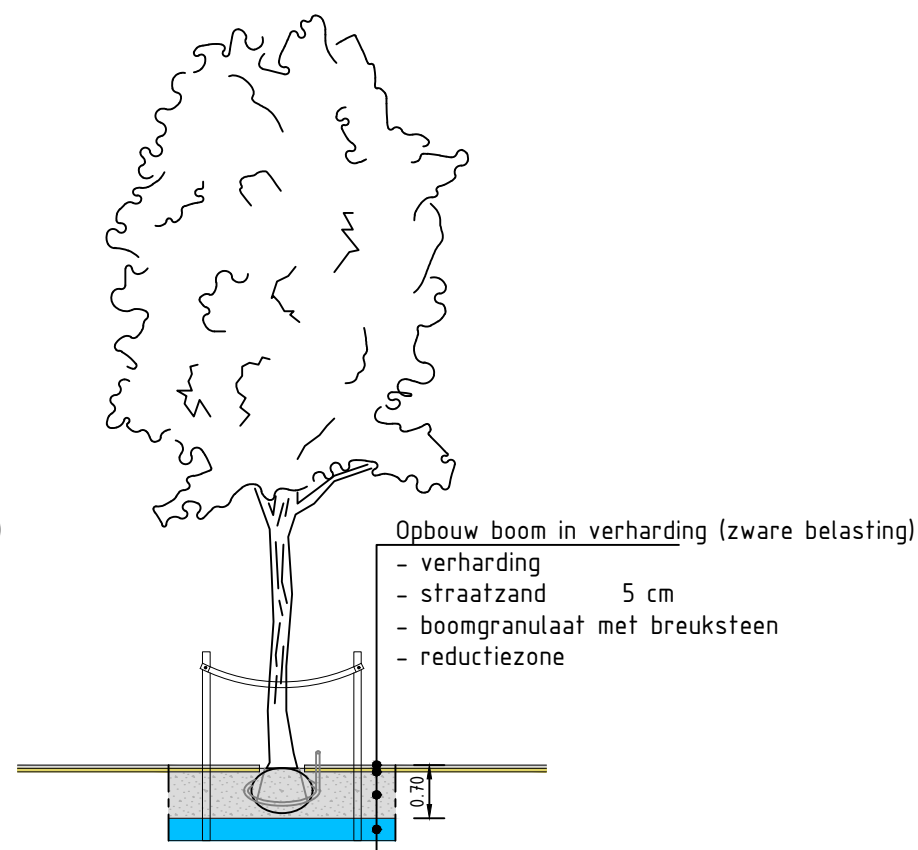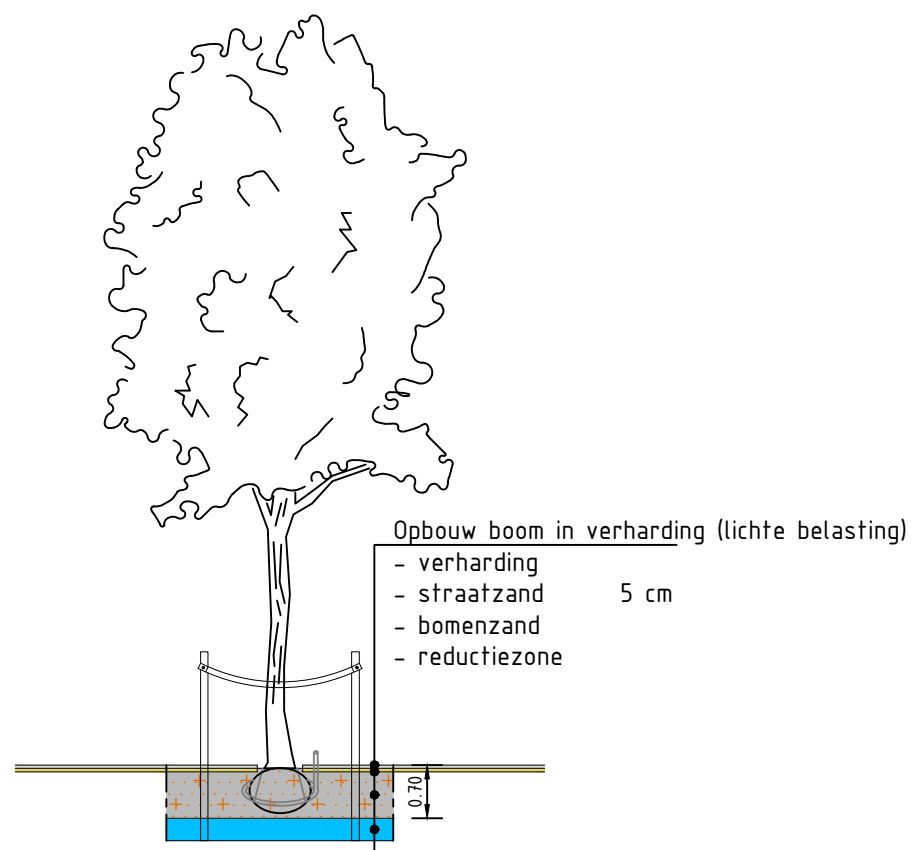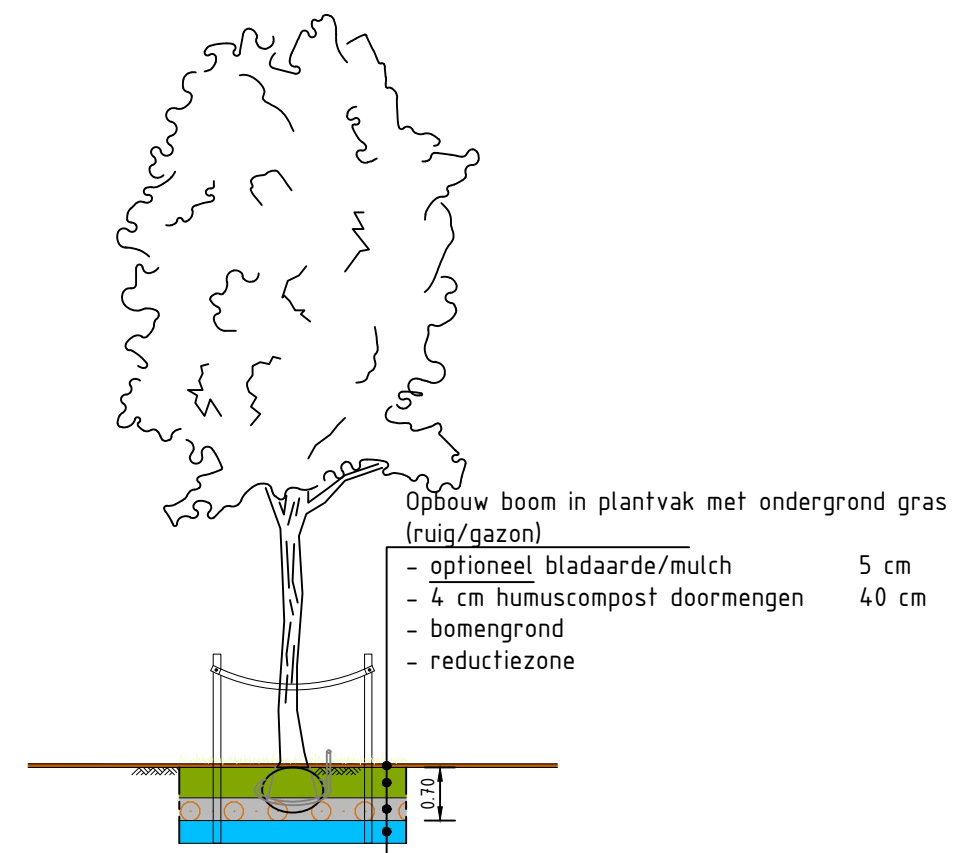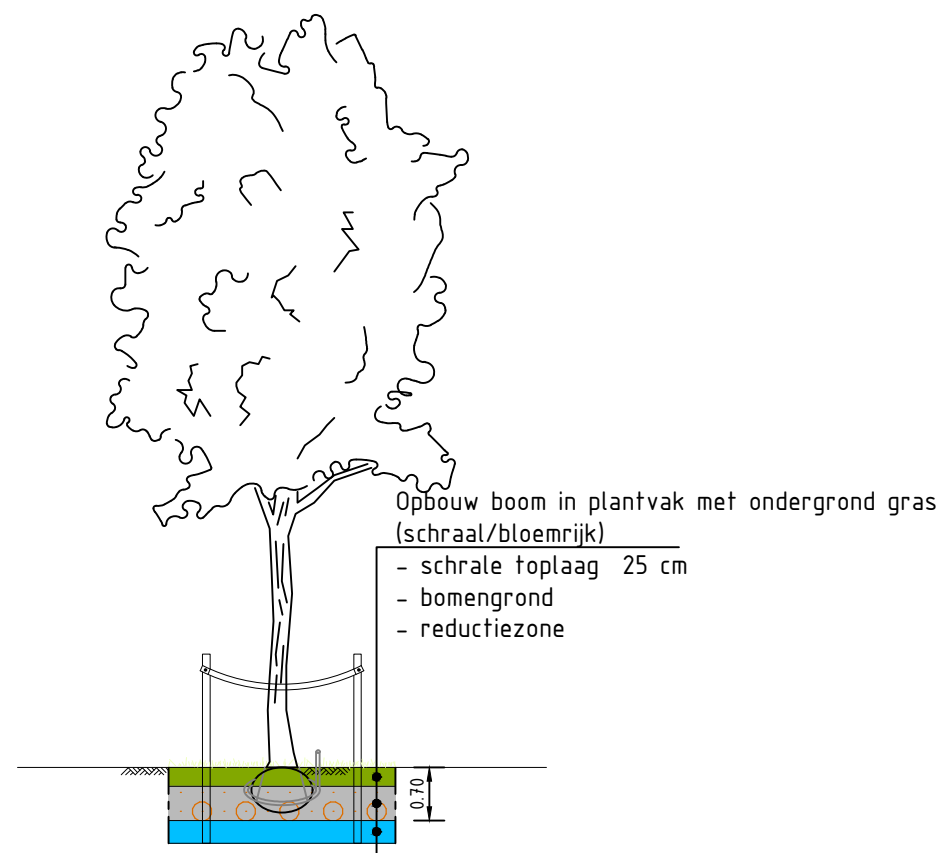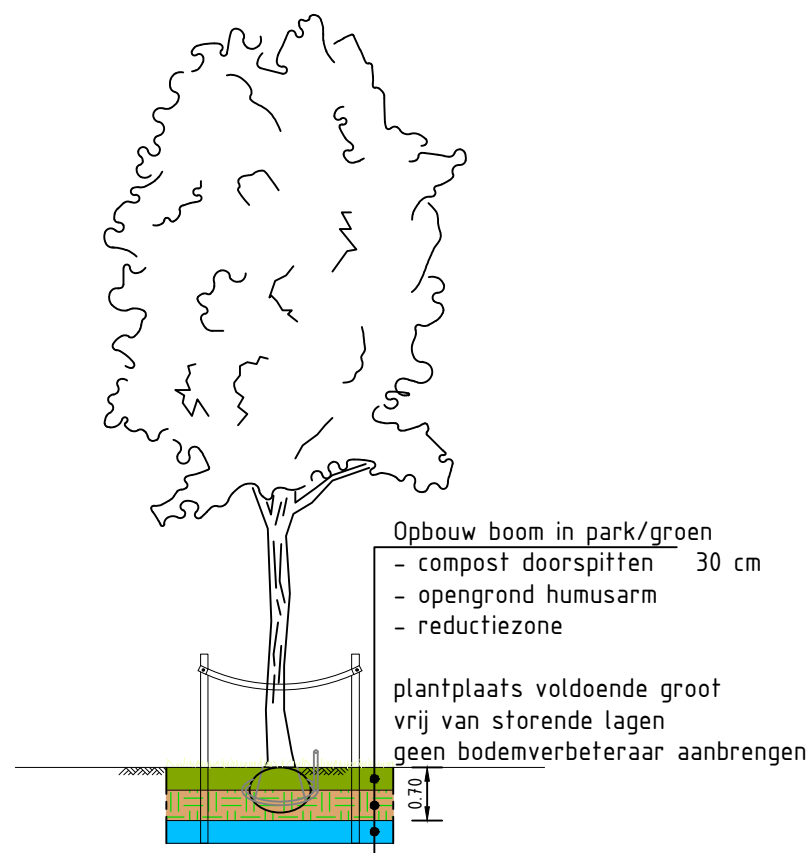

Afwijking Handboek Bomen: Voor de laagopbouw in Zoetermeer geldt de opbouw zoals in deze detailtekening is weergegeven. Toepassing van (extra) lagen zoals 10 cm drainagezand uit het Handboek Bomen is hierbij niet standaard vereist, tenzij projectspecifiek anders voorgeschreven.

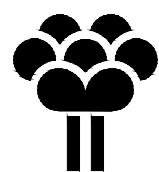



Gemeente
Zoetermeer

Laagopbouw aanplant bomen in diverse situaties


getekend: Gemeente Zoetermeer
gewijzigd: 3-4-2026
datum:

formaat: A3
schaal: 1:100
volgnummer: 4-2

Stadsbeheer 2026

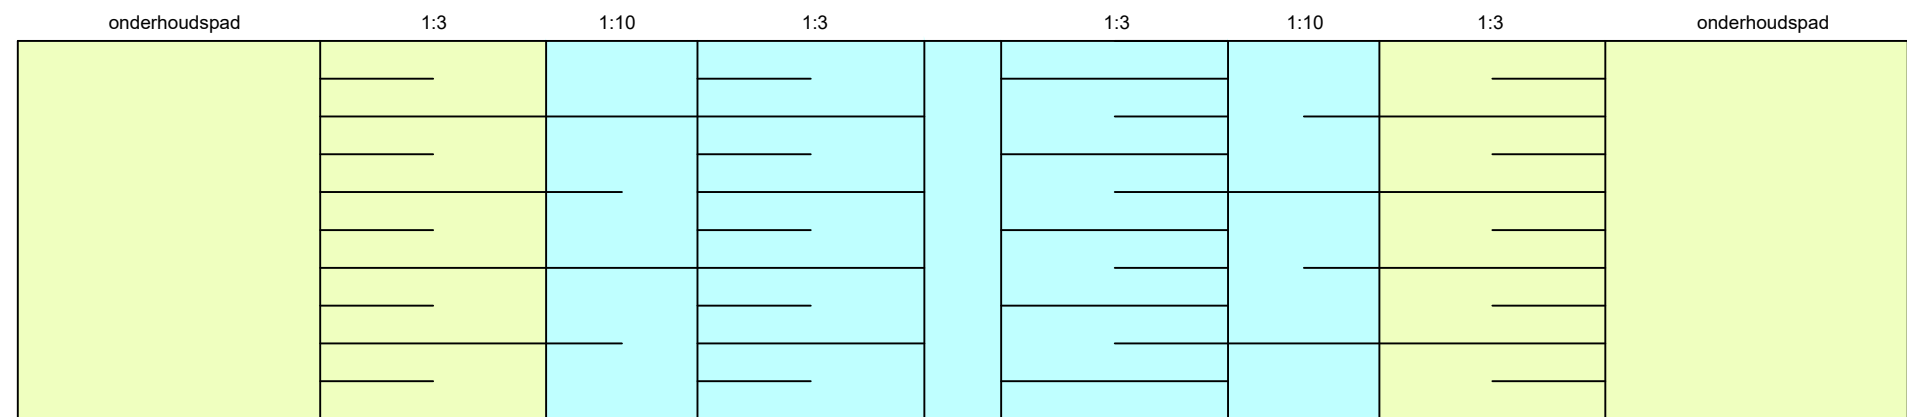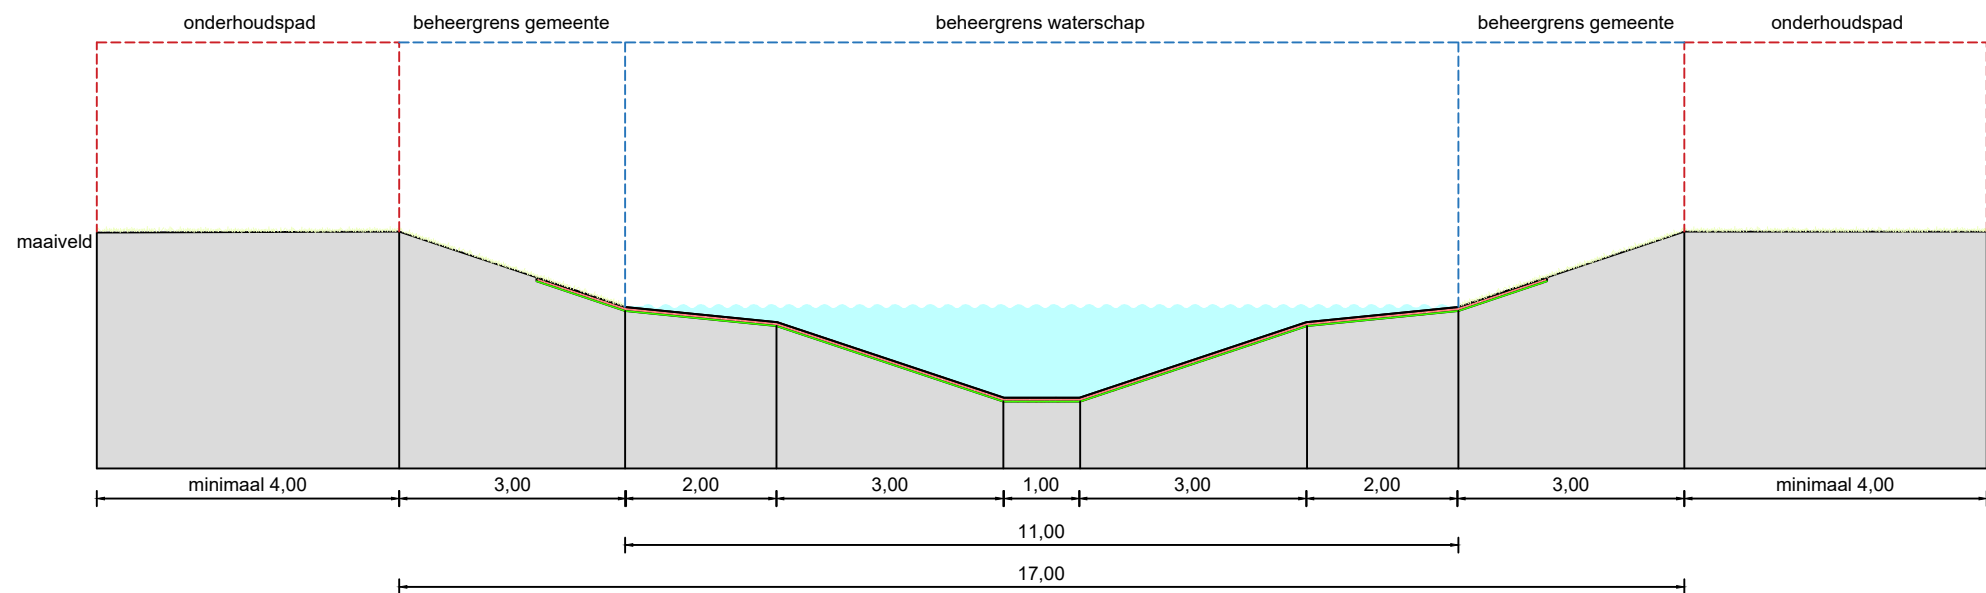

Watergang
Schaal 1:100


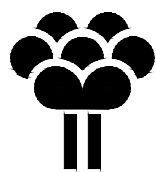


Gemeente
Zoetermeer
Watergang

getekend: Gemeente Zoetermeer
gewijzigd: 3-4-2026
datum:

formaat: A3
schaal: 1:100
volnummer: 5-1

Stadsbeheer 2026

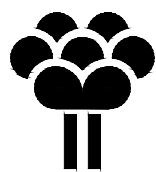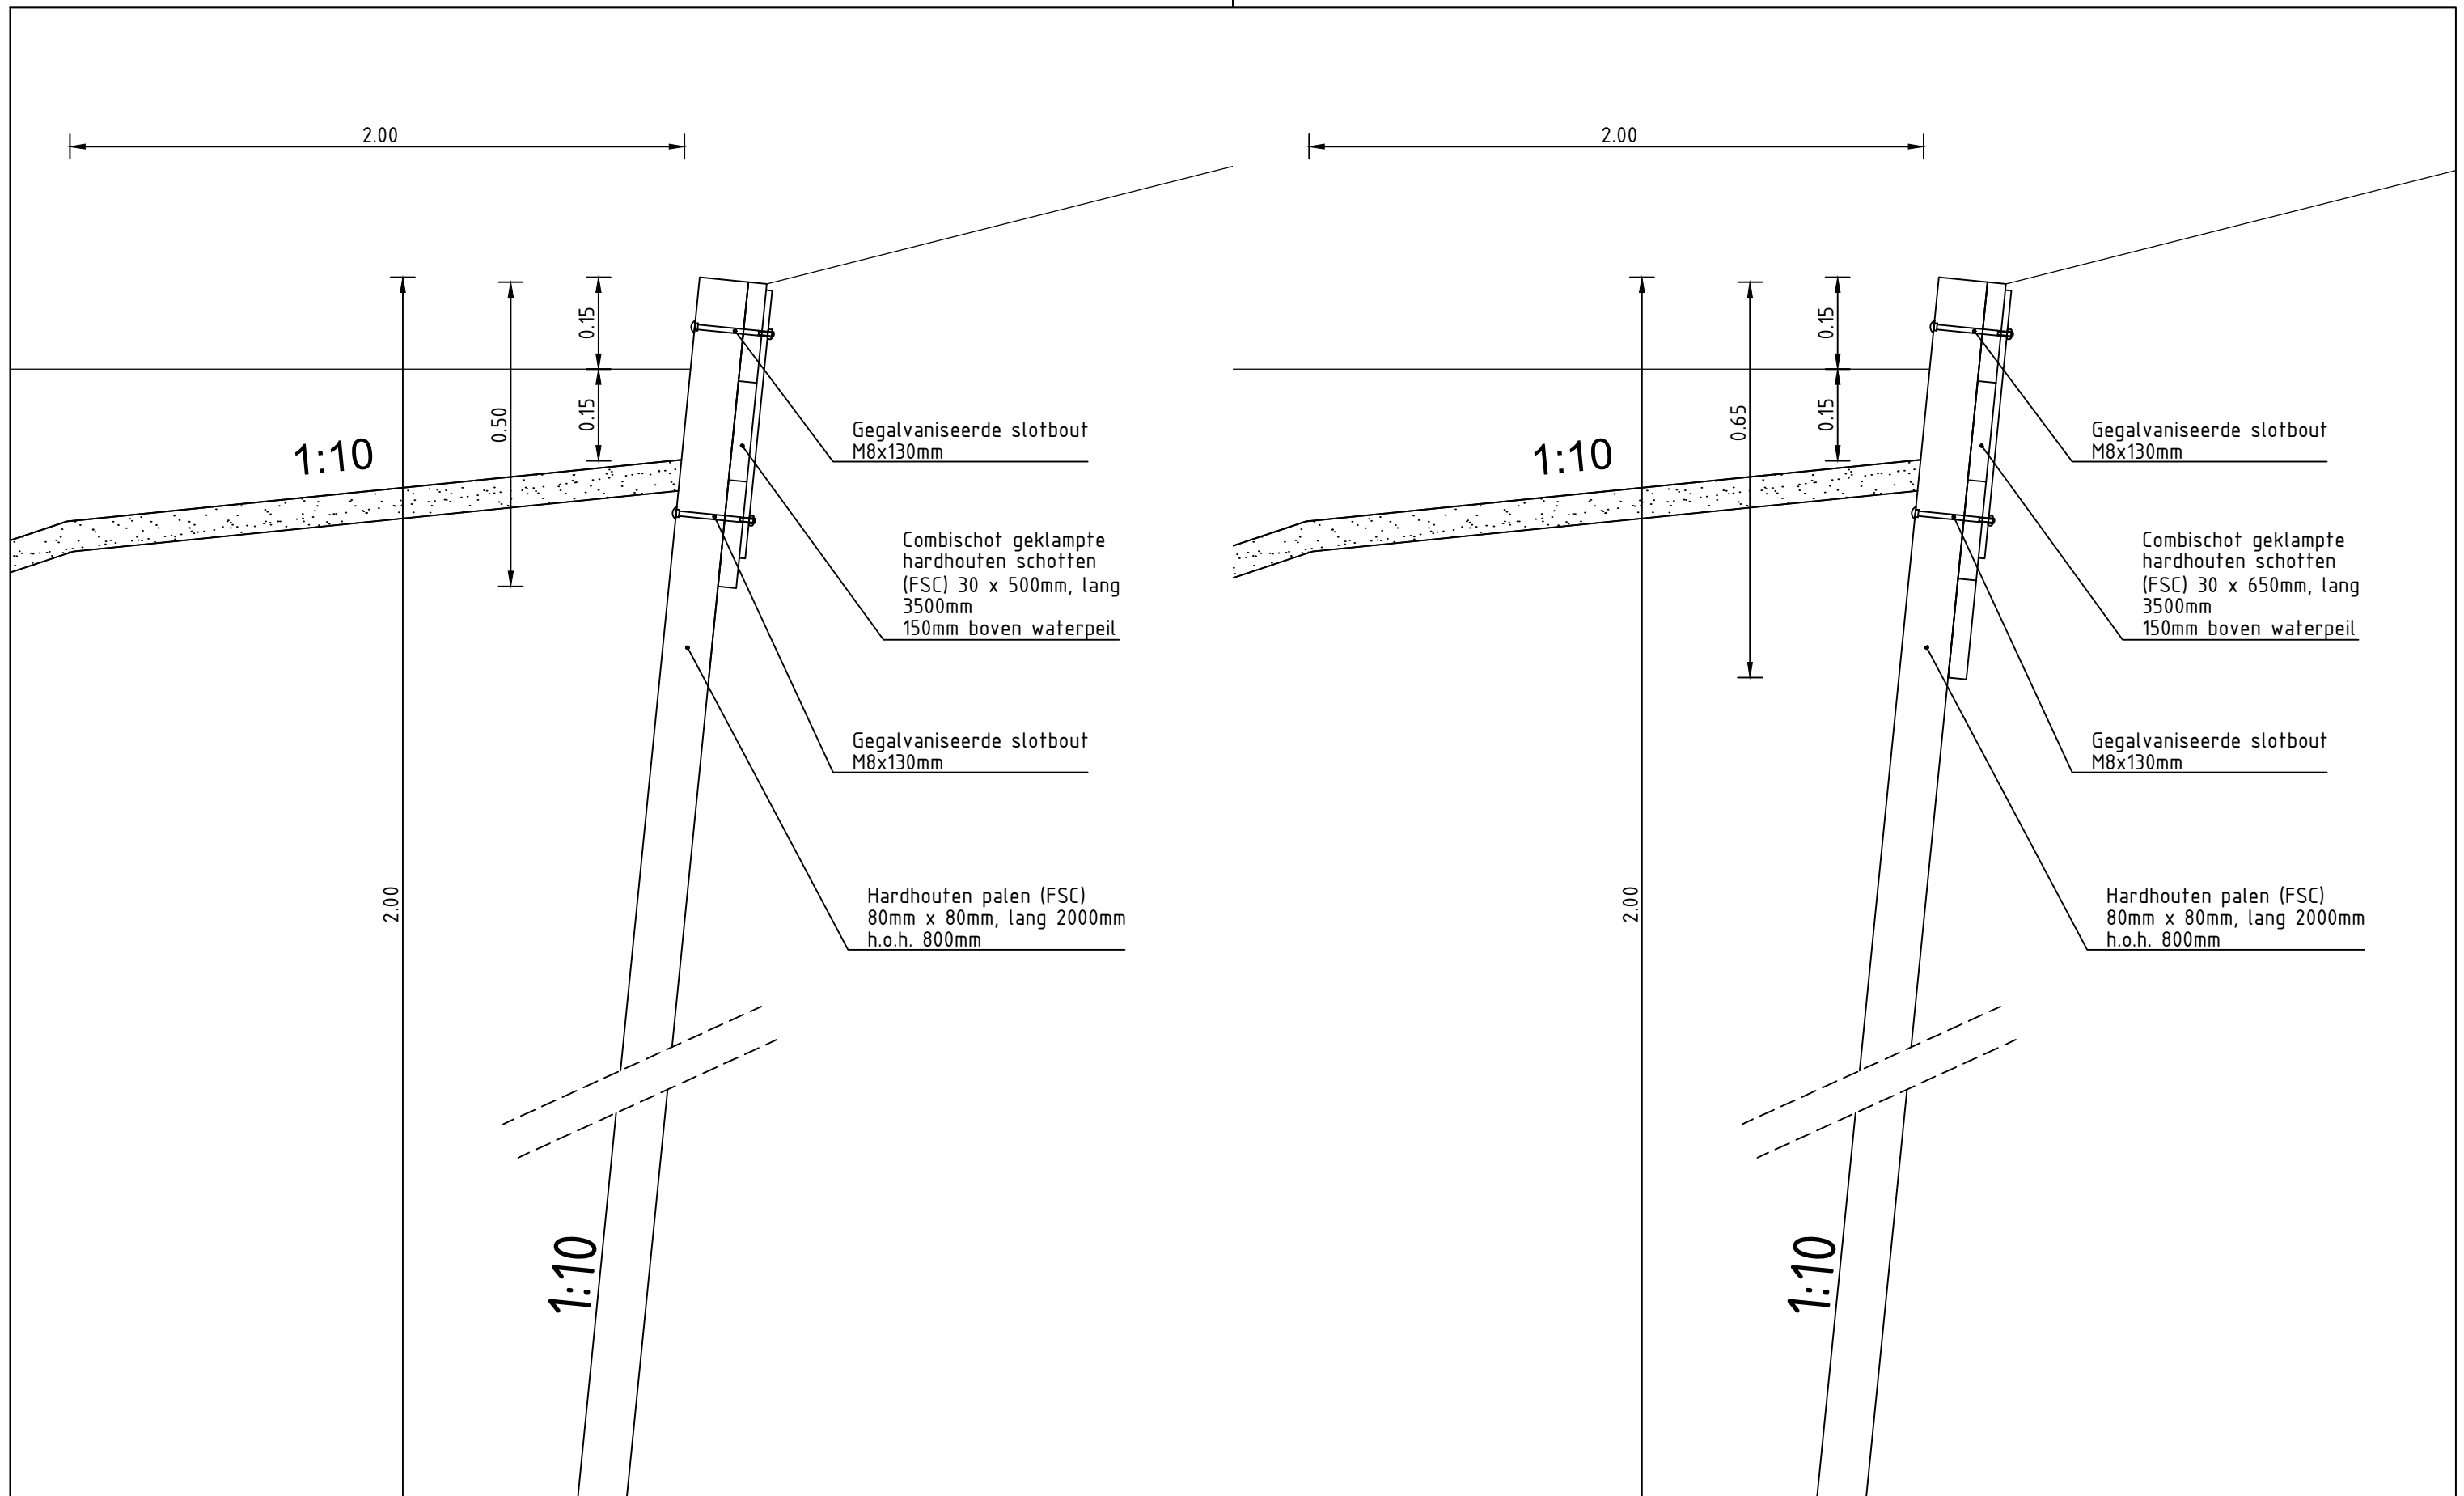




Gemeente
Zoetermeer
Beschoeide oever

getekend: Gemeente Zoetermeer
gewijzigd:
datum: 3-4-2026

formaat: A3
schaal: 1:10
volgnummer: 5-3

Stadsbeheer 2026

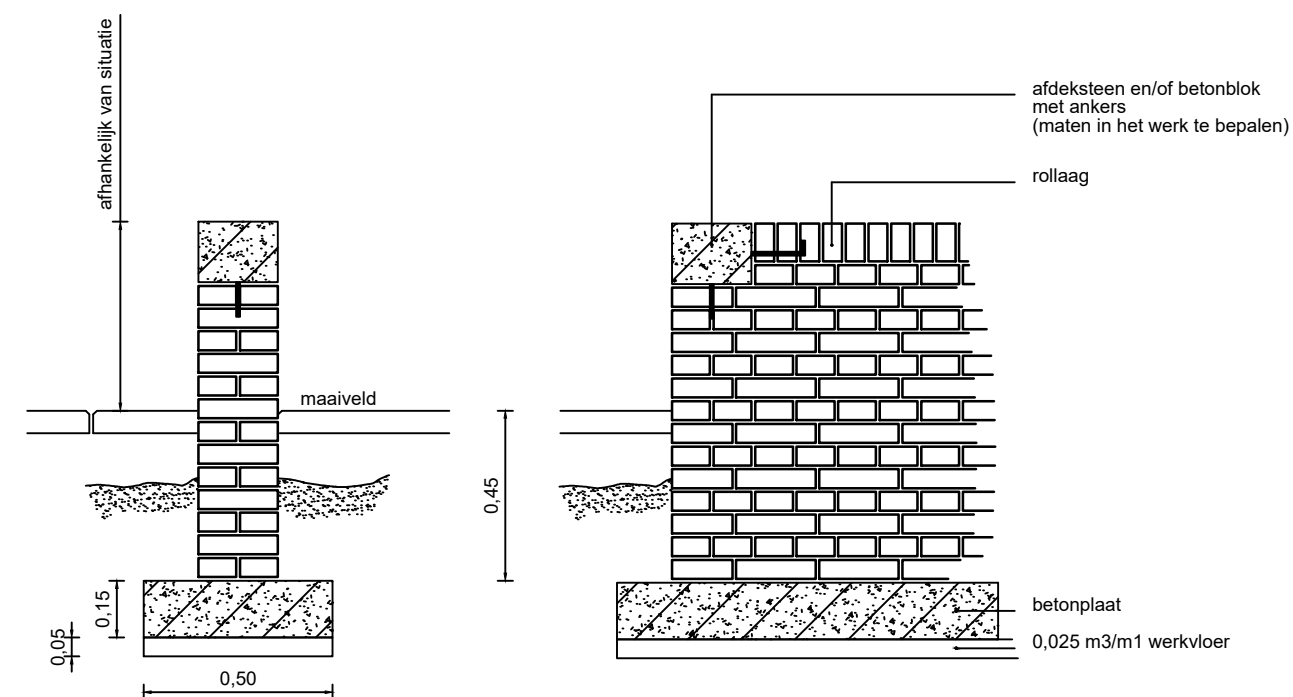

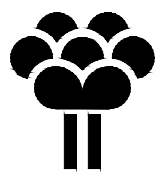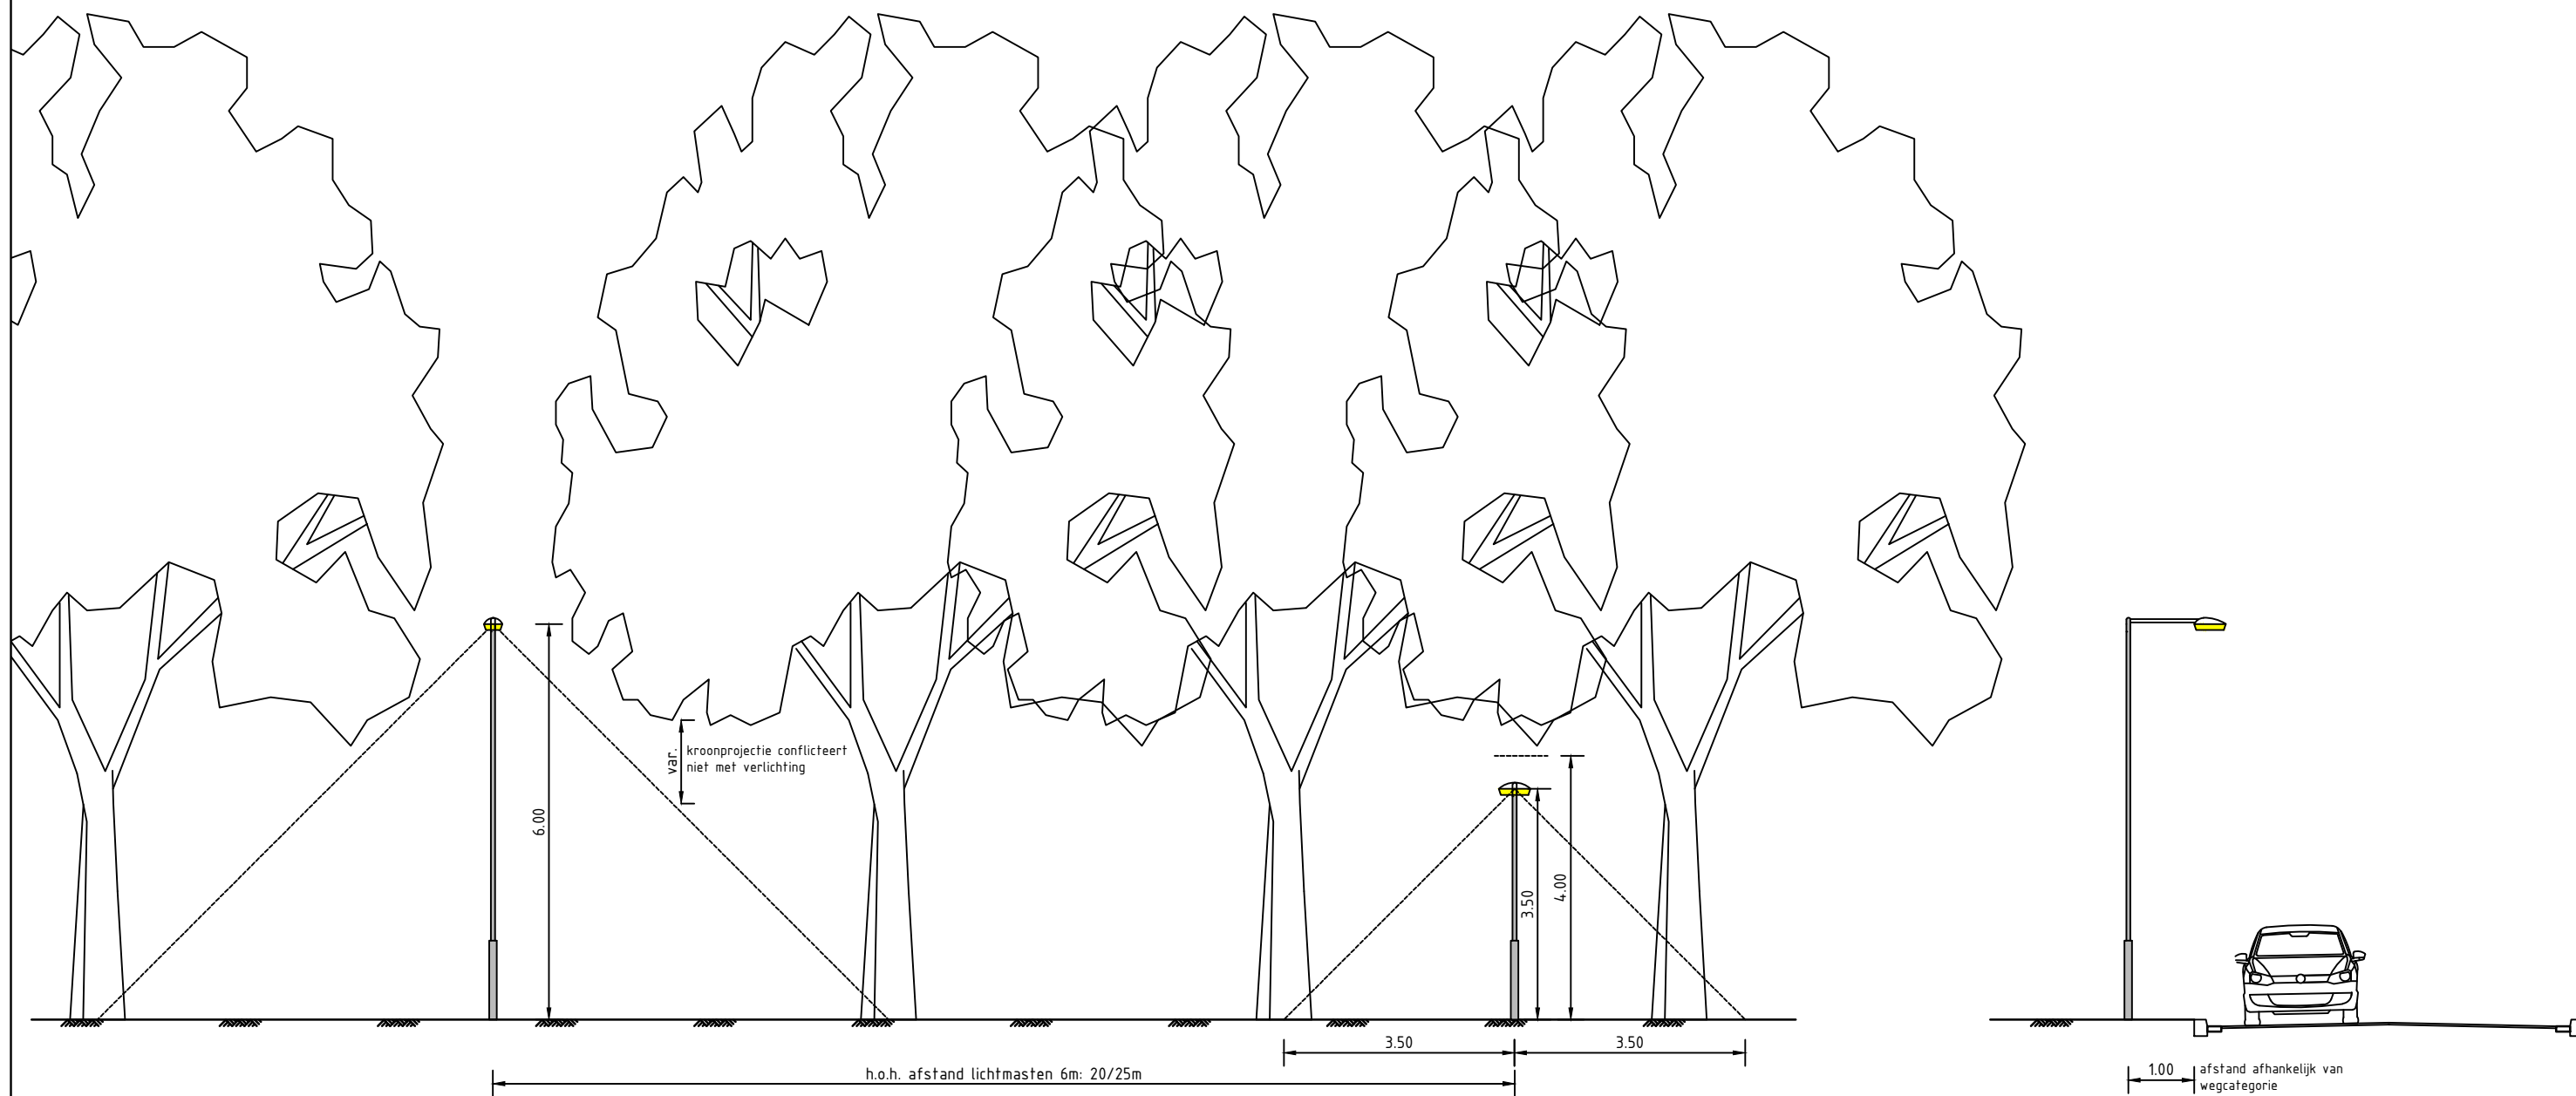

Gemeente
Zoetermeer


Bomen en verlichting

getekend:
gewijzigd:
datum:


Gemeente Zoetermeer
3-4-2026

formaat: A3
schaal: 1:100
volnummer: 7-1


Stadsbeheer 2026

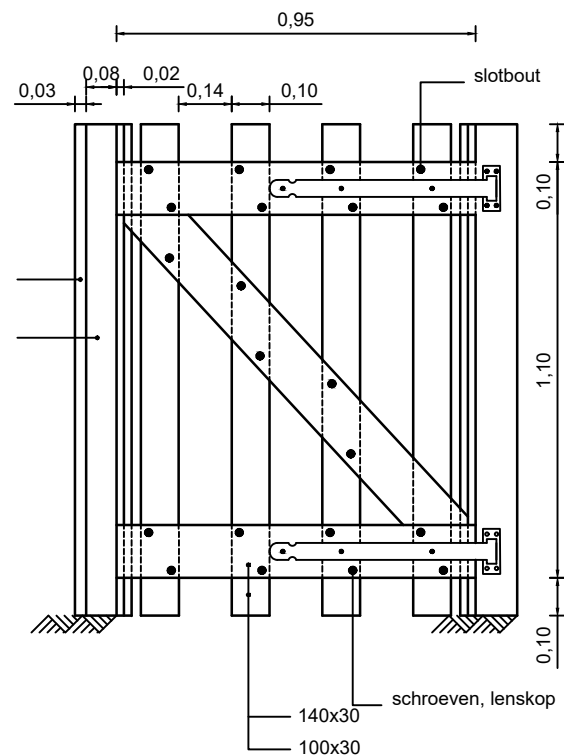

Klaphek vooraanzicht
Schaal 1:20

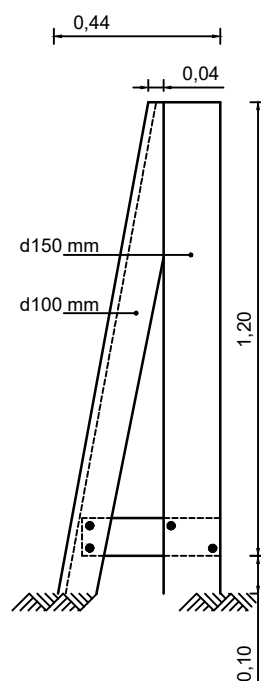


Klaphek zijaanzicht
Schaal 1:20

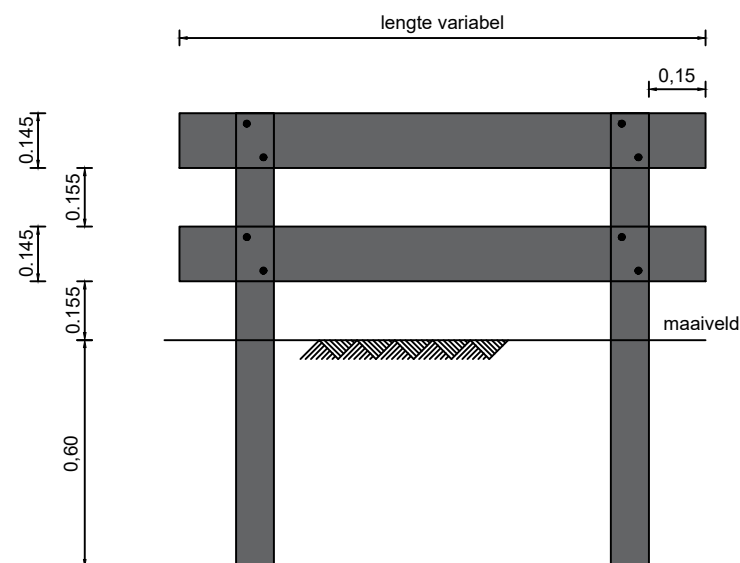

materiaal: recycled kunststof
staanders 1200x100x100
liggers 145x40 (lengte variabel)
bevestigen d.m.v. gegalvaniseerde
slotbouten M10 met volgplaat

Fietssluis - vaststaand type
Schaal 1:20

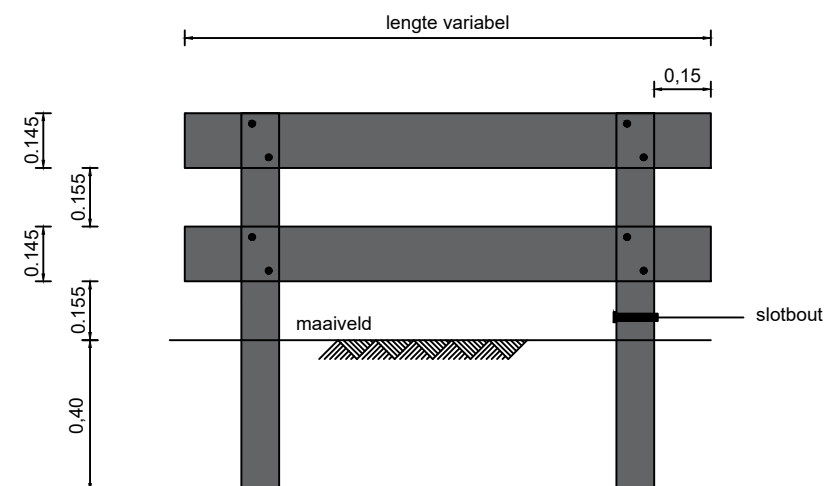


materiaal: recycled kunststof
staanders 1000x100x100
liggers 145x40 (lengte variabel)
bevestigen d.m.v. gegalvaniseerde
slotbouten M10 met volgplaat


hek plaatsen in een gegalvaniseerd
kokerprofiel, wanddikte 4
gelast op een gegalvaniseerde plaat 400x40

50 mm van bovenrand 2x20 mm gat boren
voor het aanbrengen van een pen met slot

Fietssluis - opneembaar
Schaal 1:20

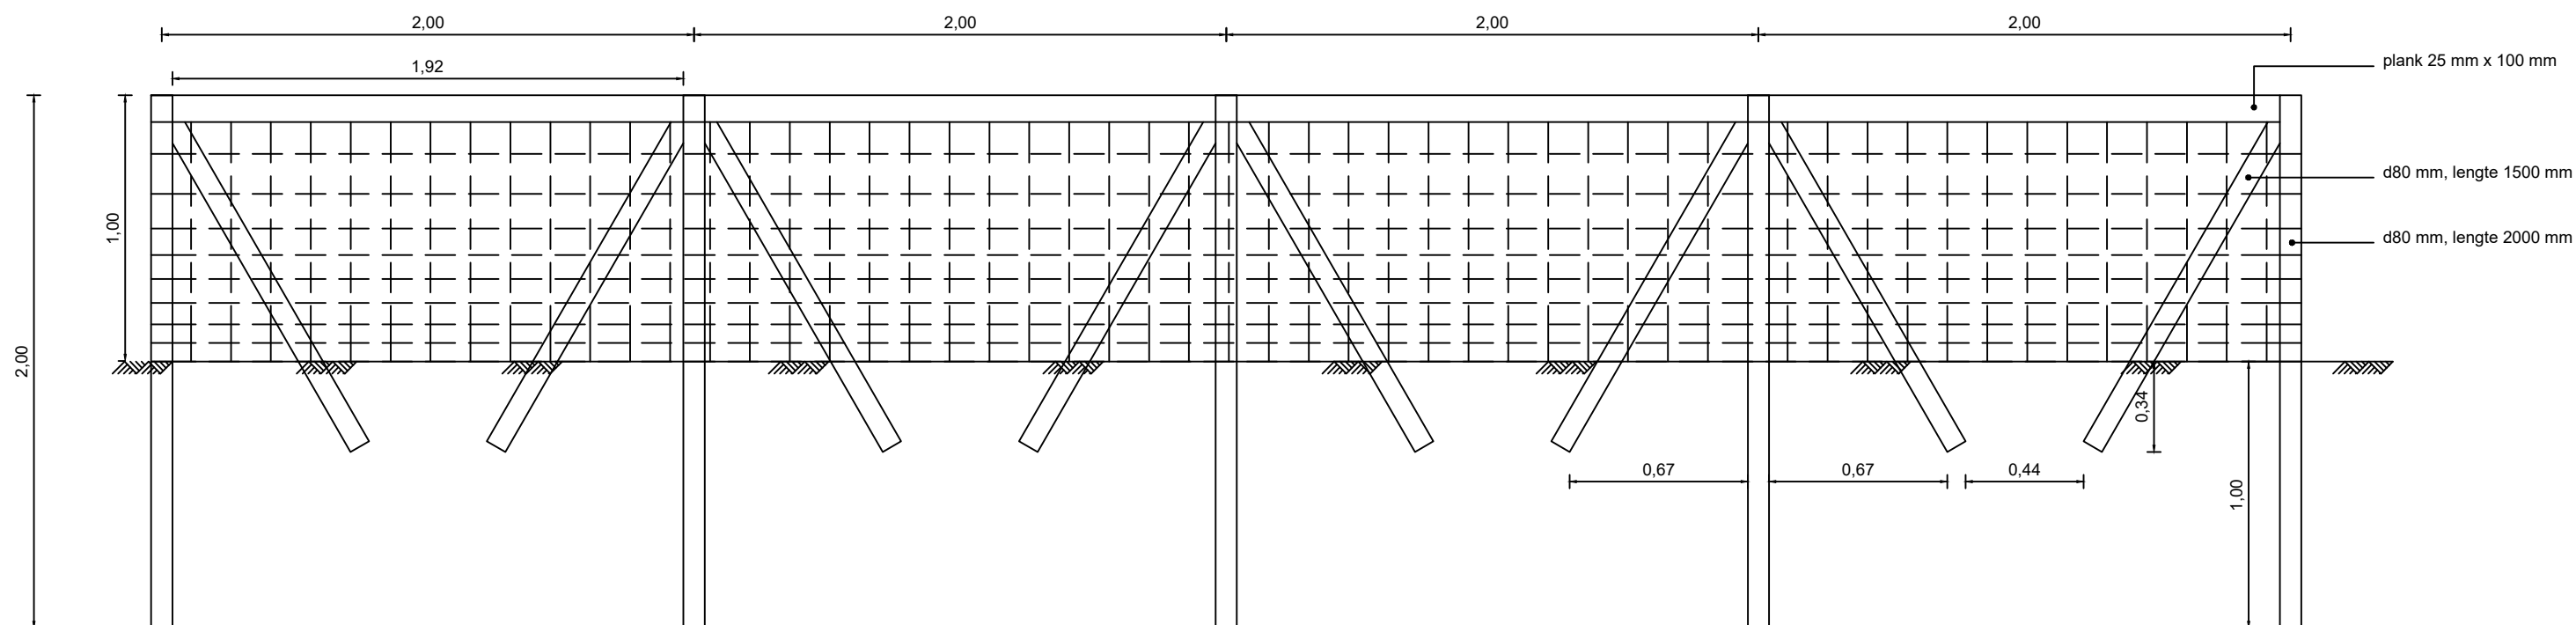

Hekwerk met schapengaas/harmonicagaas
vooraanzicht
Schaal 1:25

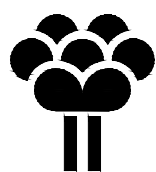


Gemeente
Zoetermeer
Hekwerken


getekend: Gemeente Zoetermeer
gewijzigd:
datum: 3-4-2026

formaat: A3
schaal: 1:20/1:25
volgnummer: 9-1




Stadsbeheer 2026

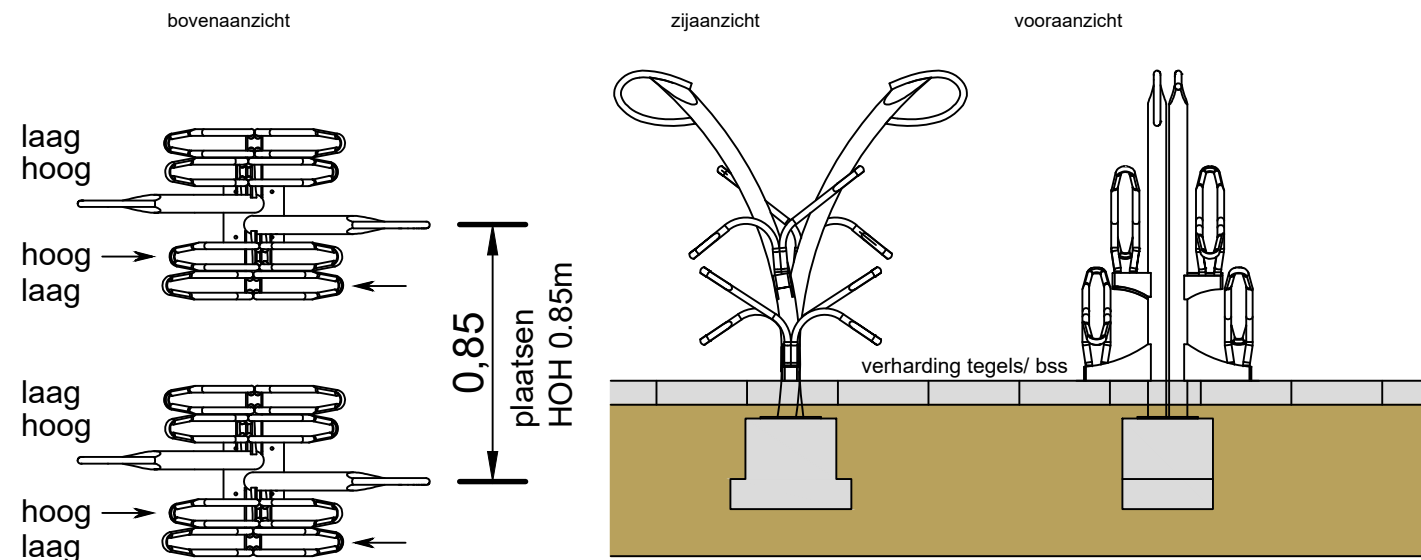

Fietsparkeren Twin Tulip

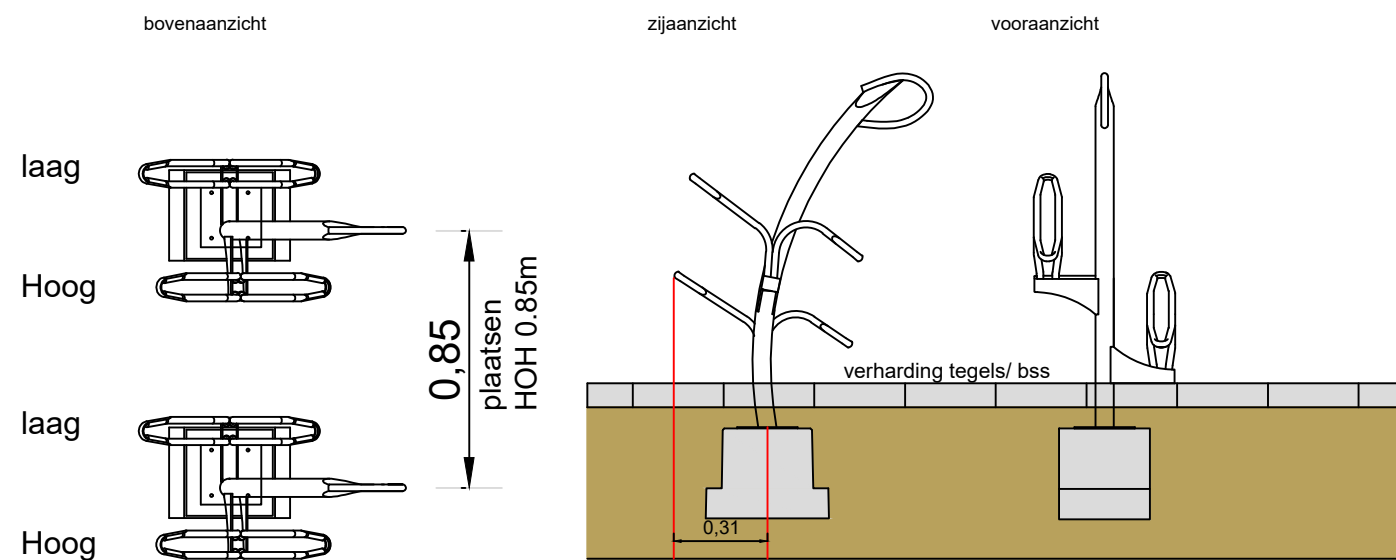

Fietsparkeren Tulip

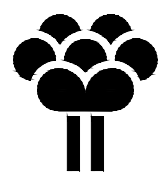
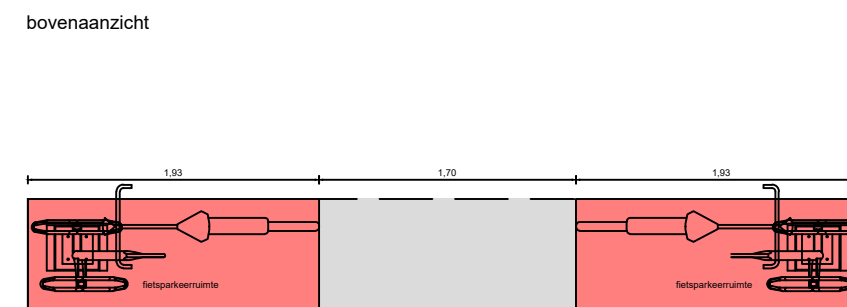
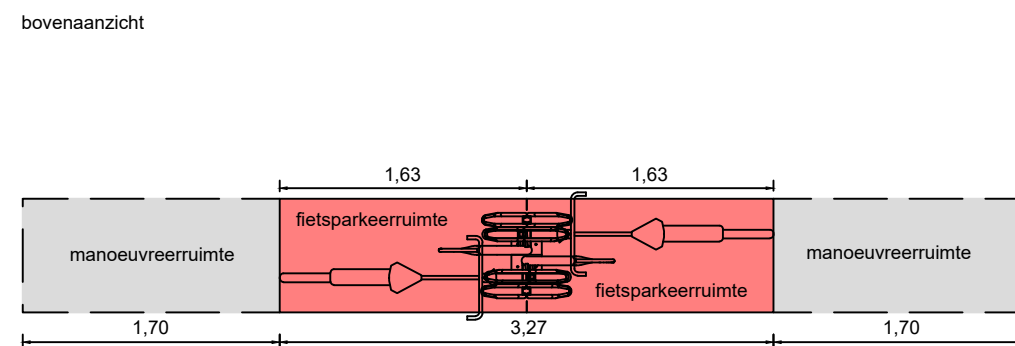


Gemeente
Zoetermeer
Fietsparkeren

getekend: Gemeente Zoetermeer
gewijzigd:
datum: 3-4-2026

formaat: A3
schaal: 1:25/1:50
volnummer: 9-2

Stadsbeheer 2026

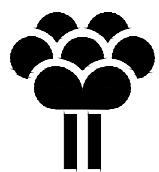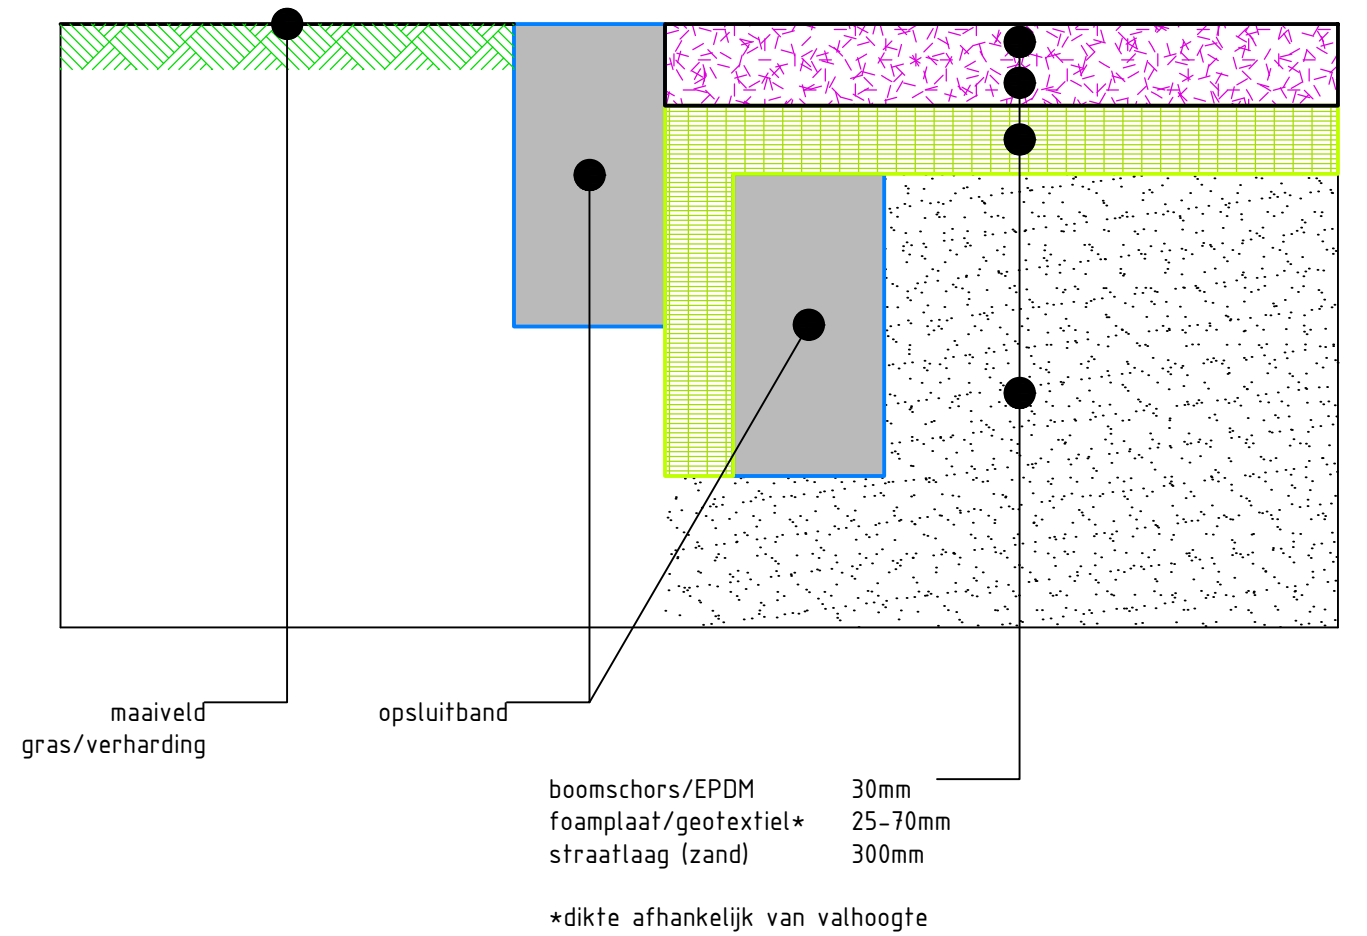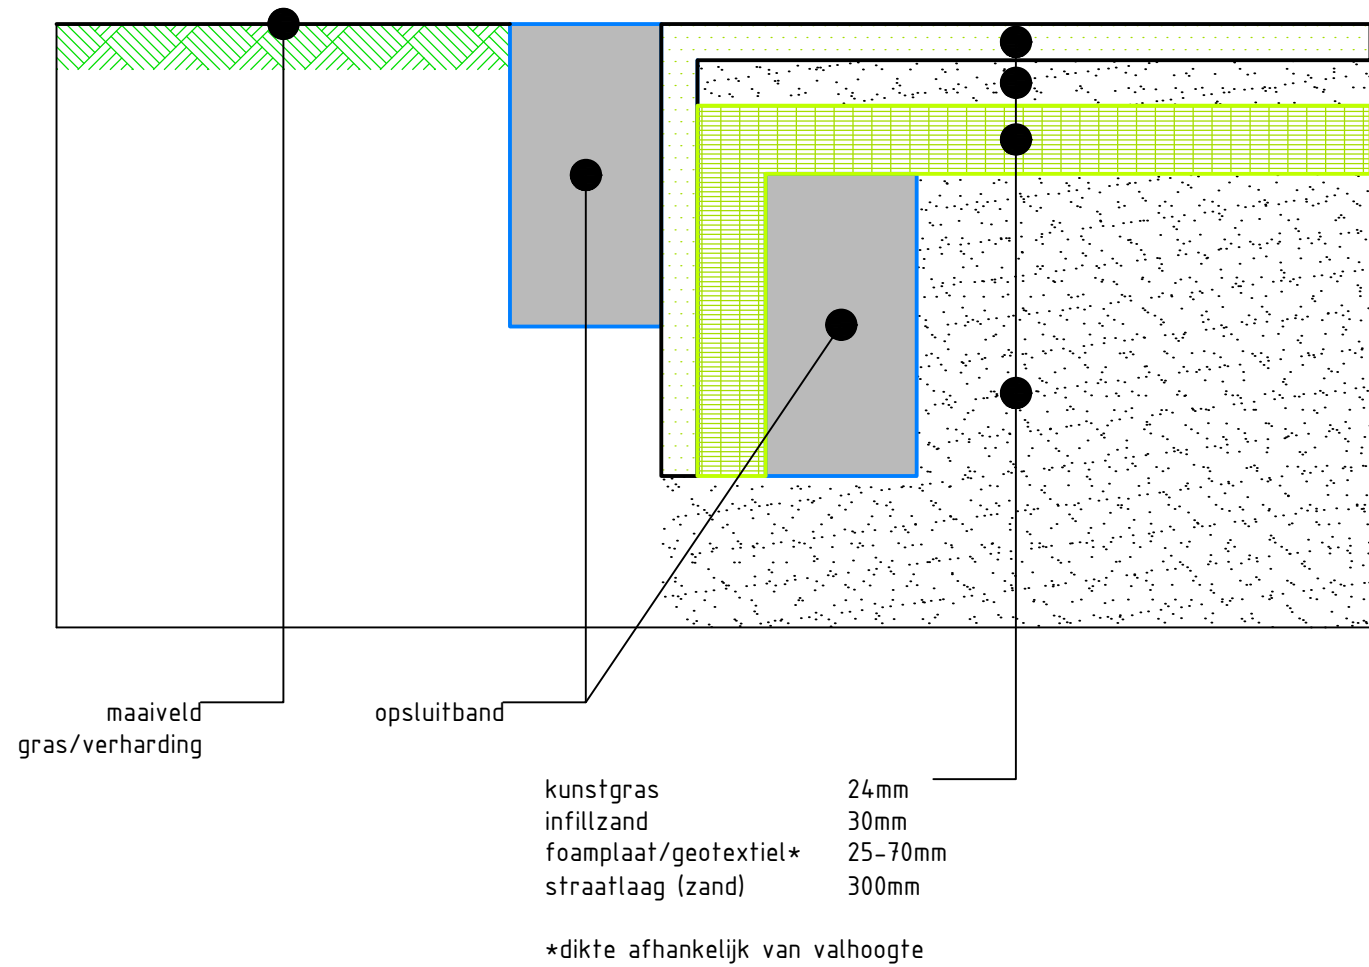

Gemeente
Zoetermeer

10 Spelen - Details valondergronden spelen

getekend: Gemeente Zoetermeer
gewijzigd:
datum: 3-4-2026



formaat: A3
schaal: 1:5
volgnummer: 10-1

Stadsbeheer 2026

Titel








Ontwerp X - Toelichting

Omschrijving speelplek

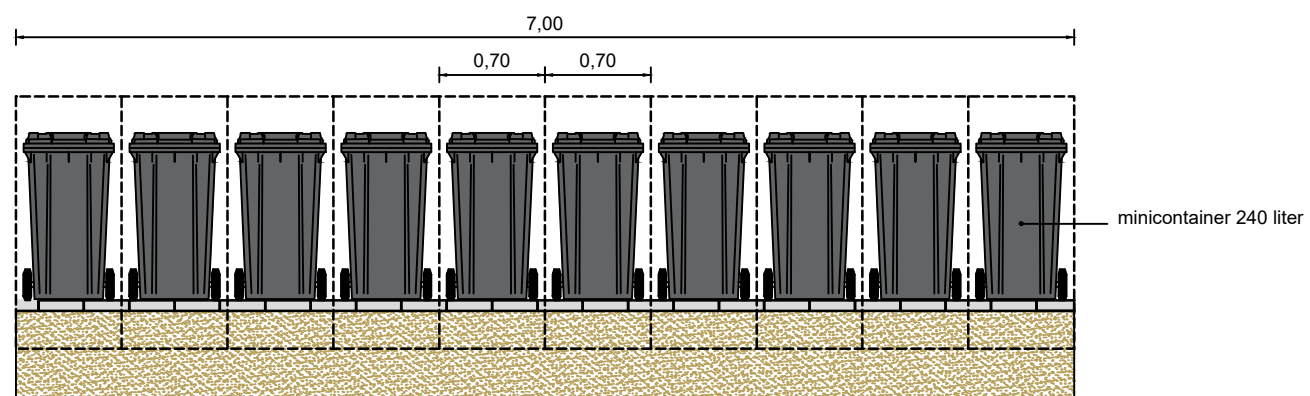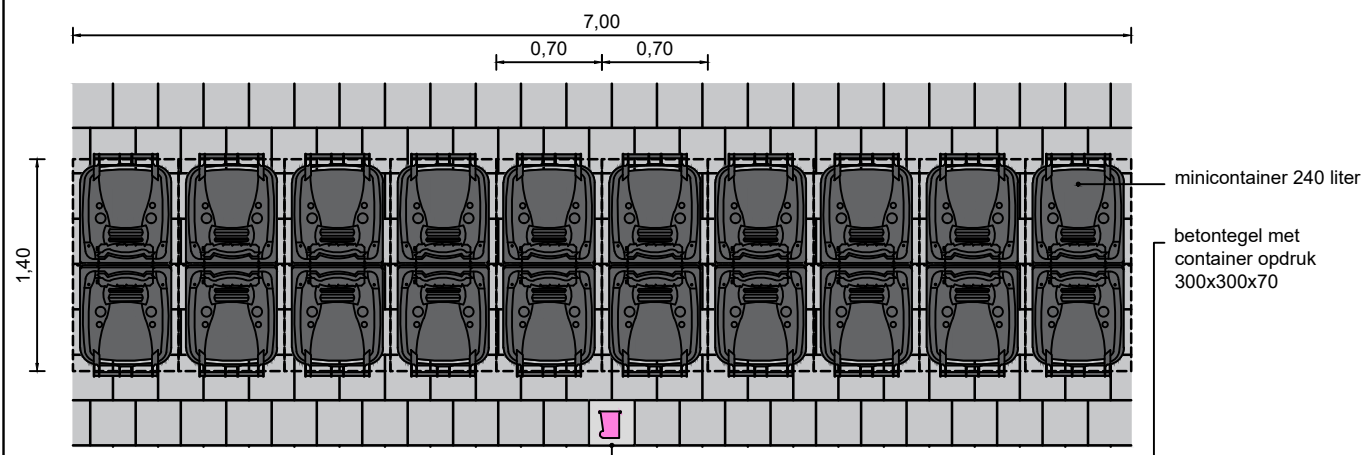

locatie ondergrondse afvalscheiding (zoals : Glas, Papier, kunststof, textiel)

locatie ondergrondse huisafval container (zoals: Rest en GFT)

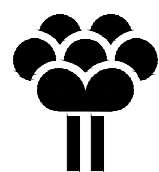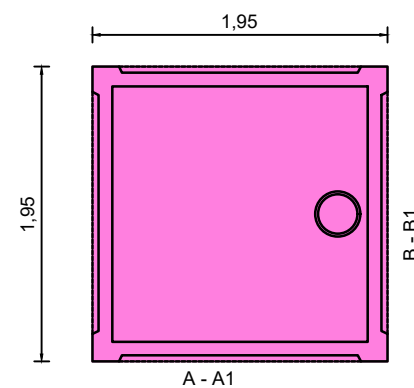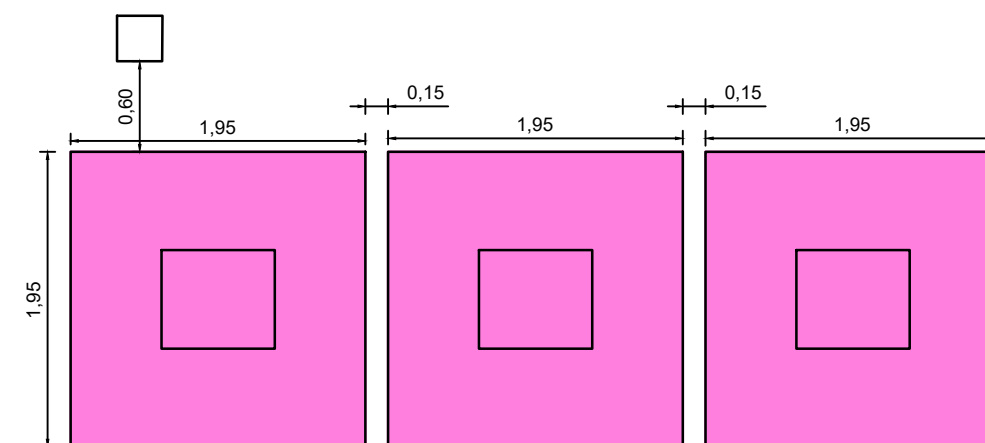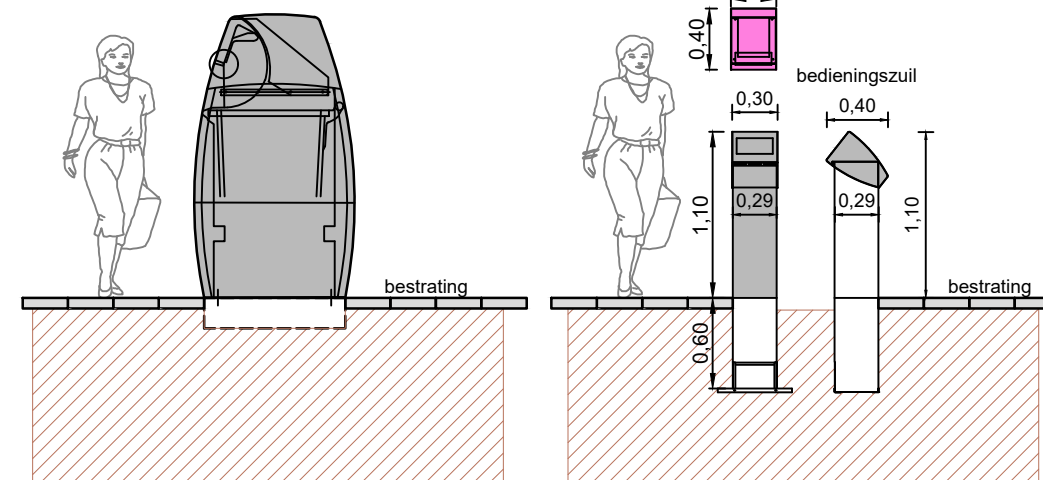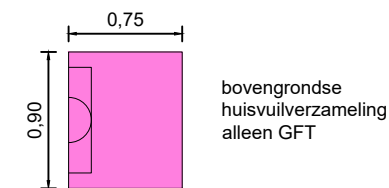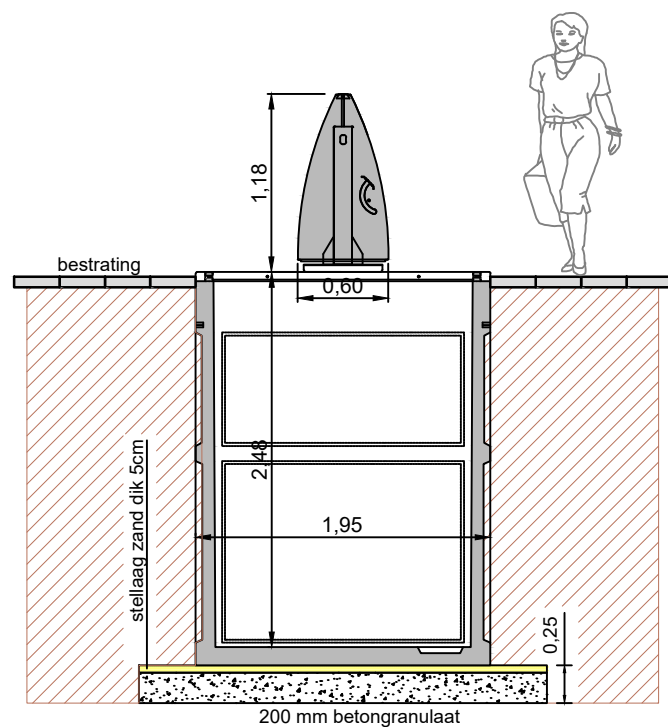
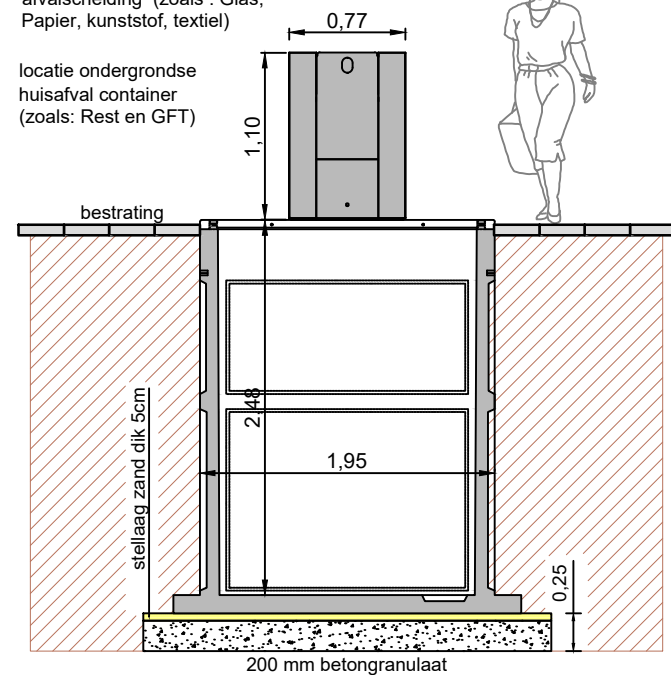


Gemeente
Zoetermeer
Huisafvalinzameling

getekend: Gemeente Zoetermeer
gewijzigd: 3-4-2026
datum:

formaat: A3
schaal: 1:50
volgnummer: 11-1

Stadsbeheer 2026

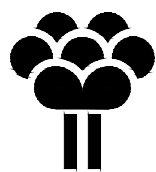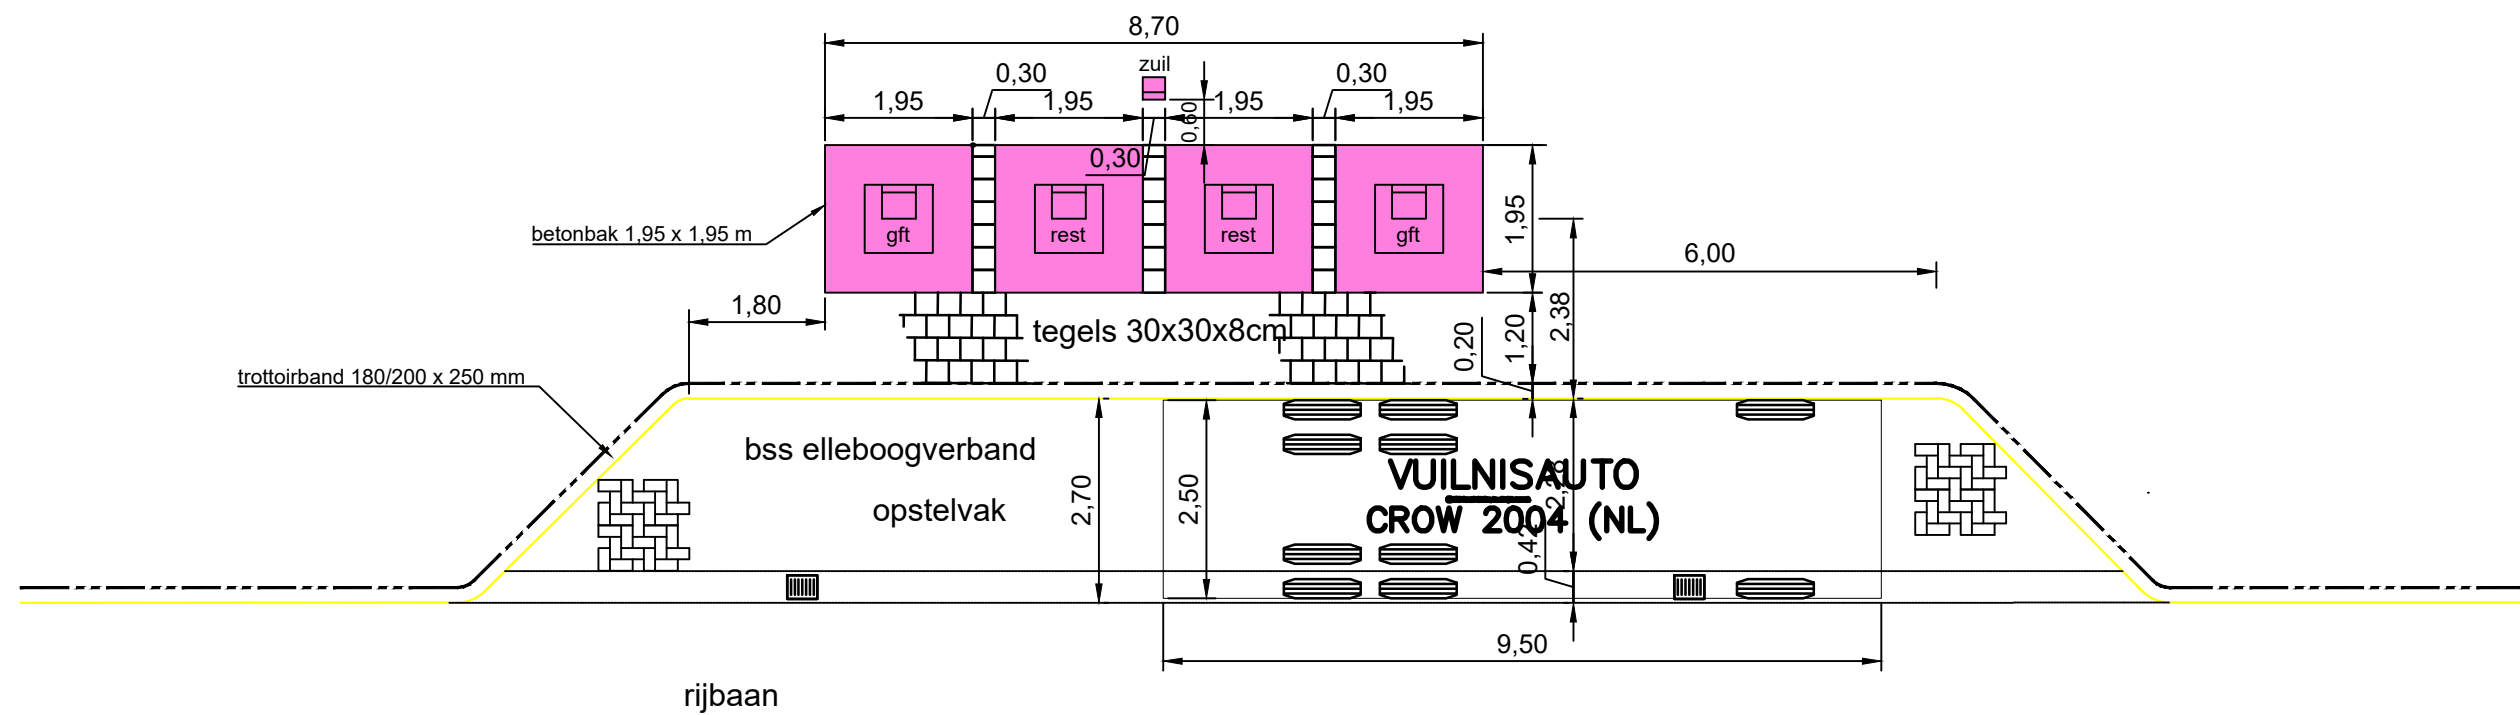

Gemeente
Zoetermeer

Opstelling ondergrondse perscontainers

getekend: Gemeente Zoetermeer
gewijzigd:
datum: 3-4-2026

formaat: A3
schaal: 1:100
volnummer: 11-2

Stadsbeheer 2026